

DRAWING


ITEM NO.	PART NUMBER	DESCRIPTION	QTY.
1	HWM UNIT WALKWAY-3 W 630X L 18790 MM LONG	MS SQ TUBE 30X30X2.6 MM THK	1
2	CHEQUERED_MS PLATE_W630 X L18790 X 3MM THK	MS CHEQURED PLATE - W630 X L 18790 X 3 MM THK	1

REV DESCRIPTION	DATE	REV NO
	28-08-2025	REV 00
1.		

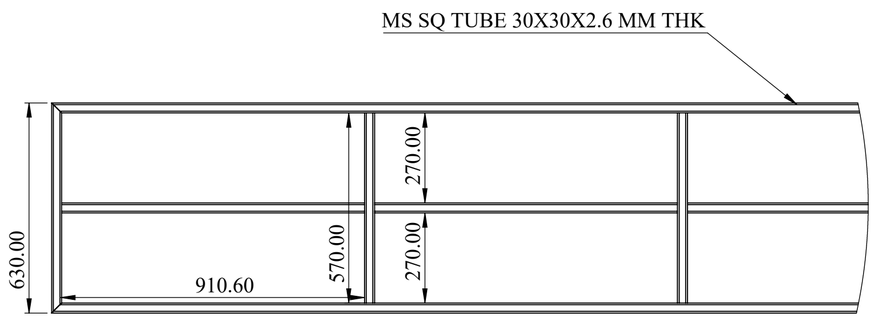

DETAIL C
SCALE 1 : 13

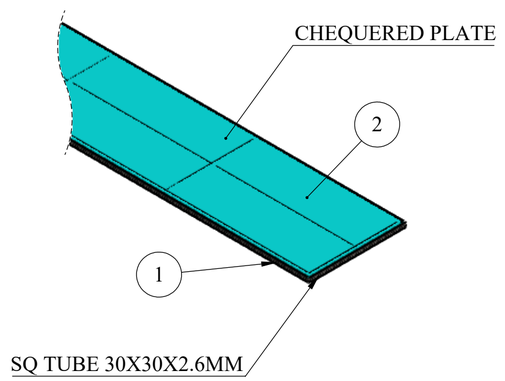

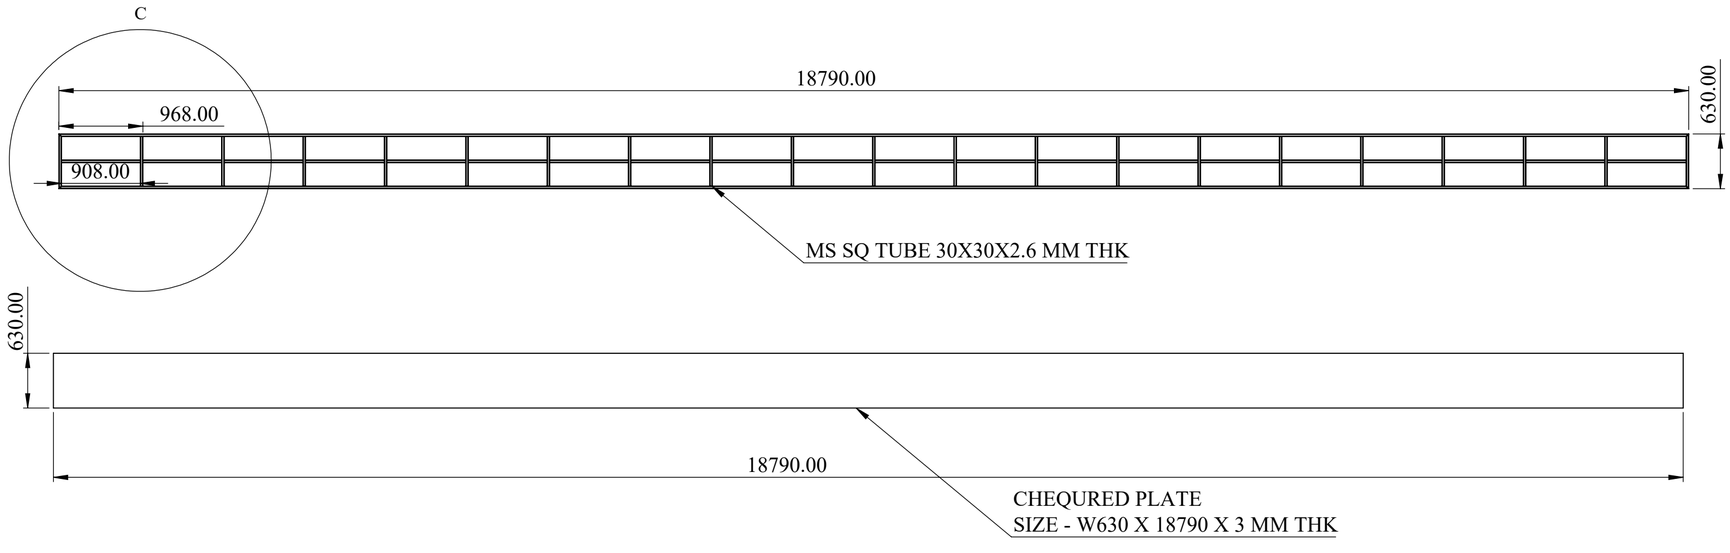

NOTE :

NAME: WALKWAY'S
SIZE : 630 x18790 MM LONG
MTL : MS
QTY : 01 NOS

SPECIAL INSTRUCTION'S :

TITLE - ROOF AUTOMATION

DWG NO - NTPL-244-PM-001-00-00-00

NIHVA TECHNOLOGIES PVT.LTD.PUNE
Website - www.nihva.com

	NAME	SIGNATURE	DATE
DRAWN	V.W.		28-08-2025
CHK'D	S.P.		04-09-2025
APPV'D	V.T.		05-09-2025

PRODUCT - RETRACTABLE ROOF
PROJECT NO - NTPL-244-PM
REVISION - 00
SITE LOCATION - GUJARAT
WEIGHT -
MATRIAL -
QTY - 1
If any queries contact - Design@nihva.com
PROJECTION METHOD:
SCALE :
ALL DIMENSION ARE IN mm
A2
SHEET 4 OF 4