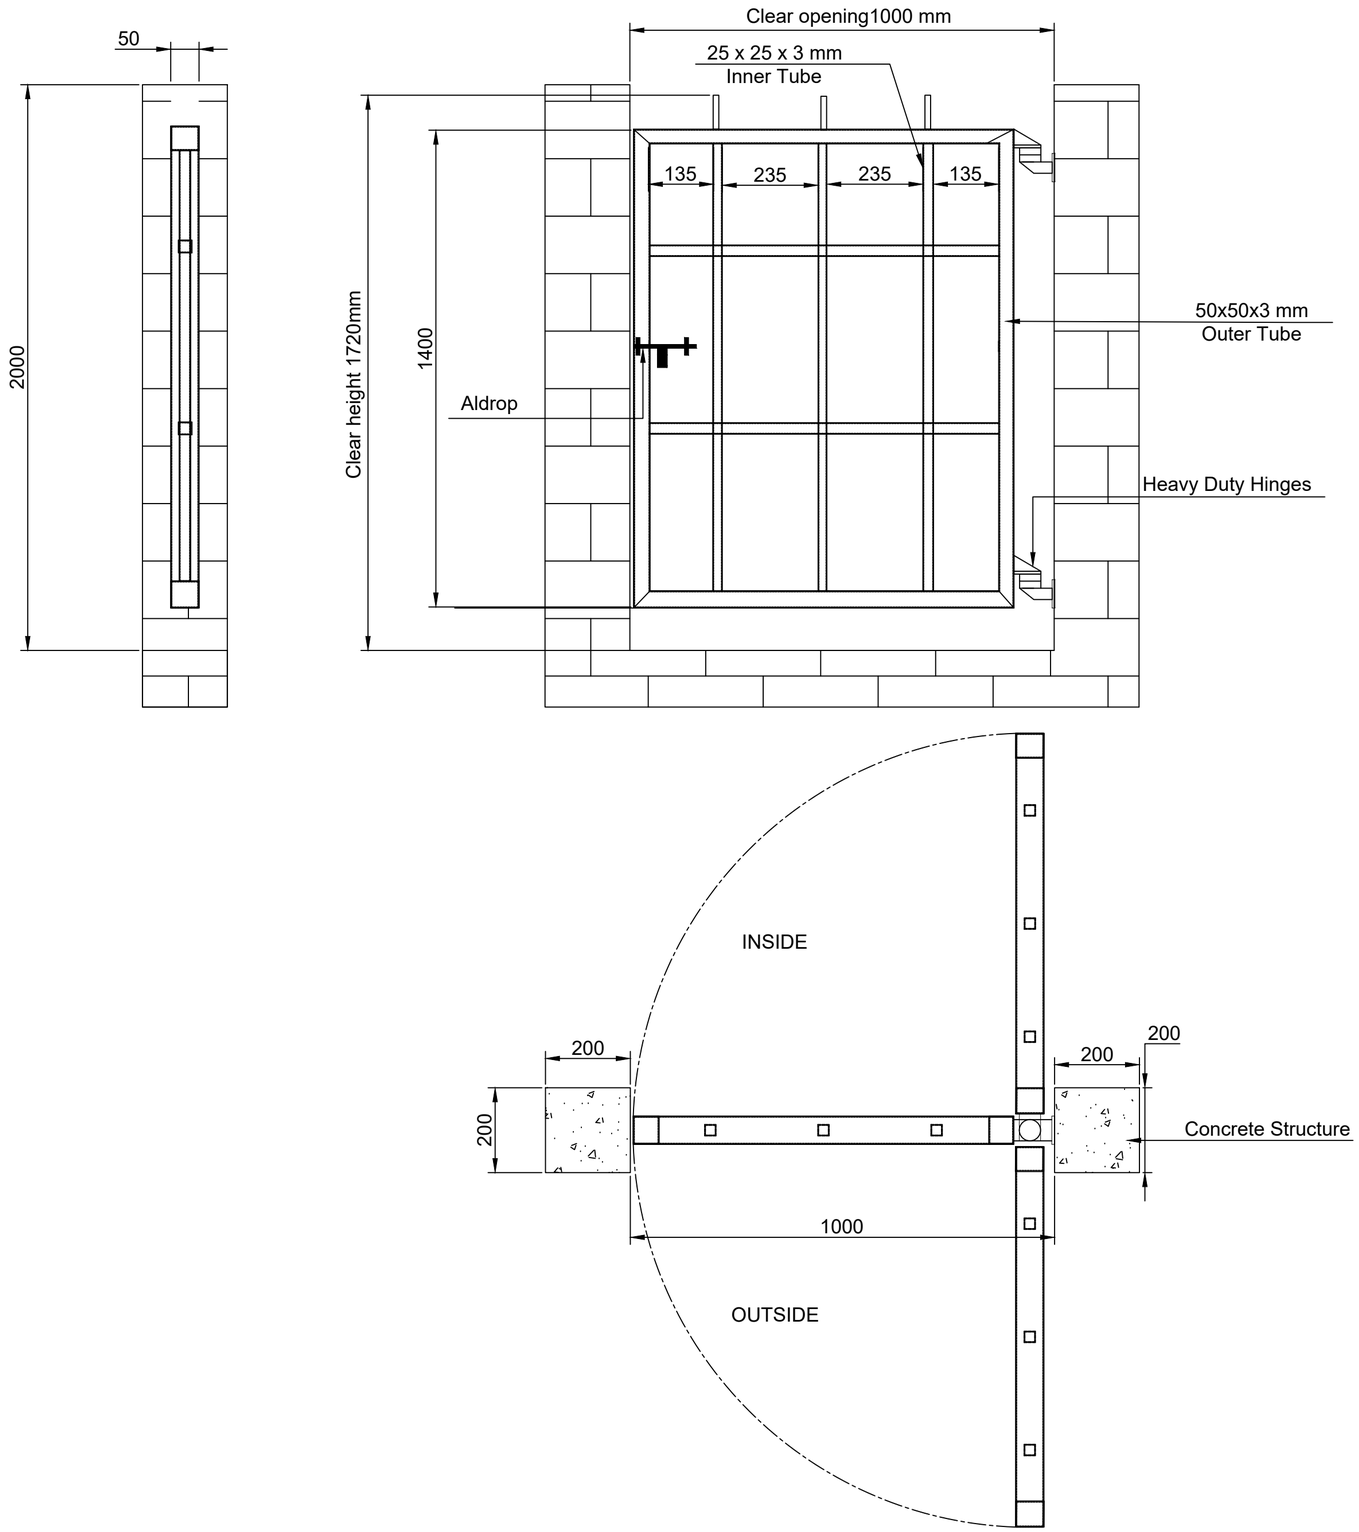


Technical Specs of Swing Gate

1. Opening Width - 1000mm
2. Gate Height - 1720mm
3. Outer tube size - MS SHS 50 x 50 x 3 mm
4. Inner tube size - MS SHS 25 x 25 x 3 mm
5. Operation - Manual

Note-

1. All dimension are in mm.
2. All civil work is under client scope.

Rev No.	Revision	Date	Revised By
CAD PATH:-			

This drawing & design is the property of NIHVA TECHNOLOGIES. Not to be sold or copied to any other concern.

TITLE:- WICKET GATE

NIHVA TECHNOLOGIES PVT. LTD.
NIHVA TECHNOLOGIES PVT. PUNE
Tel : 020 66304033
Email:- info@nihva.com
Website:- www.nihva.com

	NAME	DATE	SIGN
DRAWN	M.SUTAR	04-08-2022	
CHECK	M.SUTAR	04-08-2022	
APPRD.	A.KURHADE	04-08-2022	

CLIENT - GMR GOA INTERNATIONAL AIRPORT LIMITED

LOCATION - GOA

PRODUCT - WICKET GATE

If any queries contact : design@nihva.com

DWG NO:- NIHVA/22-23/CLT/0100 | REV- 0

ALL DIMENSION ARE IN mm

SCALE: NTS | SCALE:-- 1:1 | SHEET: 01 OF 01