

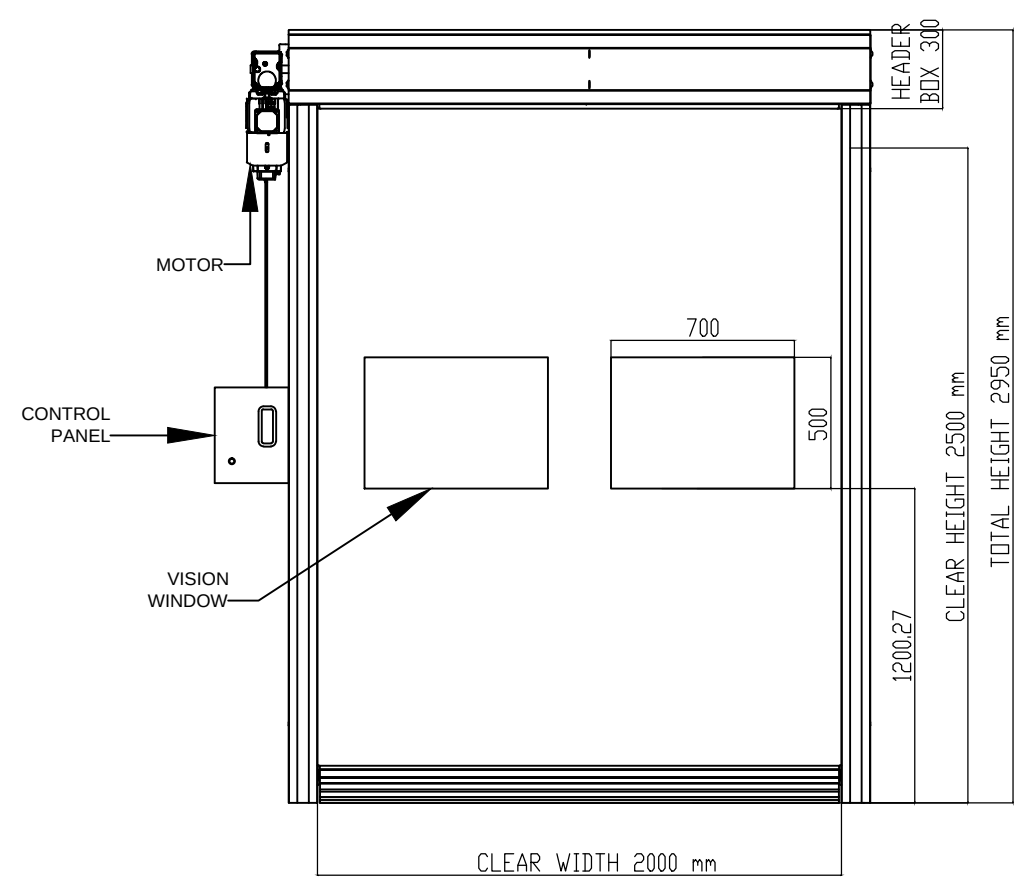


VIEW FROM OUTSIDE

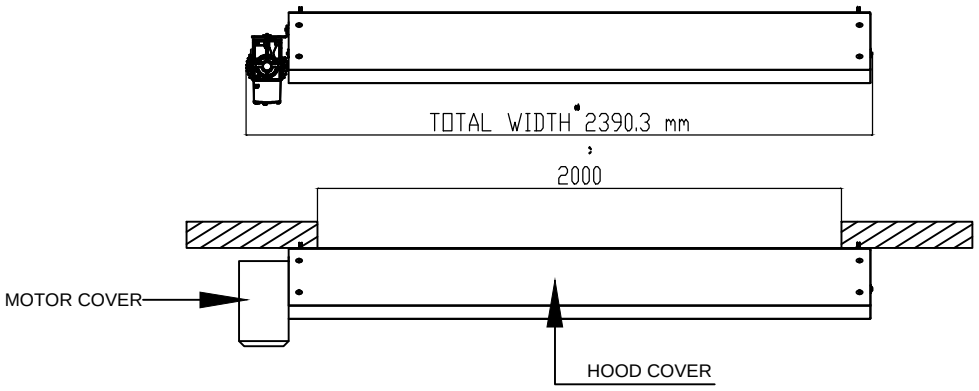

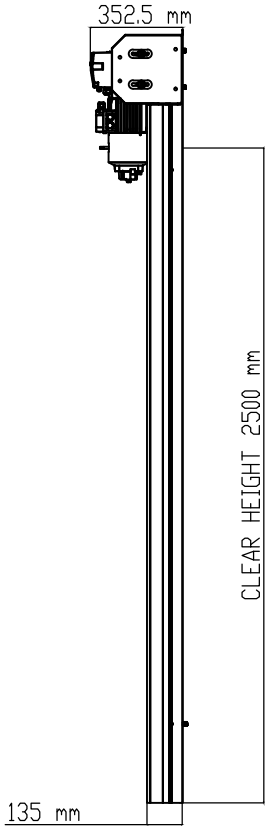

NOTE:

1. PVC CURTAIN 2 MM THICK IN BLUE (RAL 5002).
2. PUSH BUTTON WILL BE PROVIDED FROM BOTH THE SIDES(Inside & outside.)
3. DOOR WILL BE MOUNTED ON WALL.
4. ANY CIVIL WORK OR STRUCTURE REQUIRED FOR DOOR MOUNTING IS IN CLIENT SCOPE.
5. 500 MM HEIGHT REQUIRED ABOVE CLEAR OPENING FOR HEADER MOUNTING.
6. Required covers for Motor and Electrical panel will be provided.
7. Pull cod will be provided by NIHVA

REVISION-01

* Motor cover and Electric panel cover to be shown

This drawing & design is the property of NIHVA TECHNOLOGIES. Not to be sold or copied to any other concern.

TITLE	HIGH SPEED DOOR			NIHVA TECHNOLOGIES PVT. LTD. PUNE Tel : 020 66304033 Email:- info@nihva.com Website:- www.nihva.com	
	NAME	SIGN	DATE		
DRAWN	G.P.		23.09.21	CLIENT :- COLD AIR SOLUTIONS	
CHECK	A.K.		23.09.21	PROJECT :-	
APPV'ED	V.T		23.09.21	LOCATION :- AURANGABAD	
If any queries contact : design@nihva.com				DWG. NO. :- NIHVA/21-22/0234	REV :- R01
ALL DIMENSION ARE IN mm				SCALE: NTS	WT: SHEET: 01 OF 02