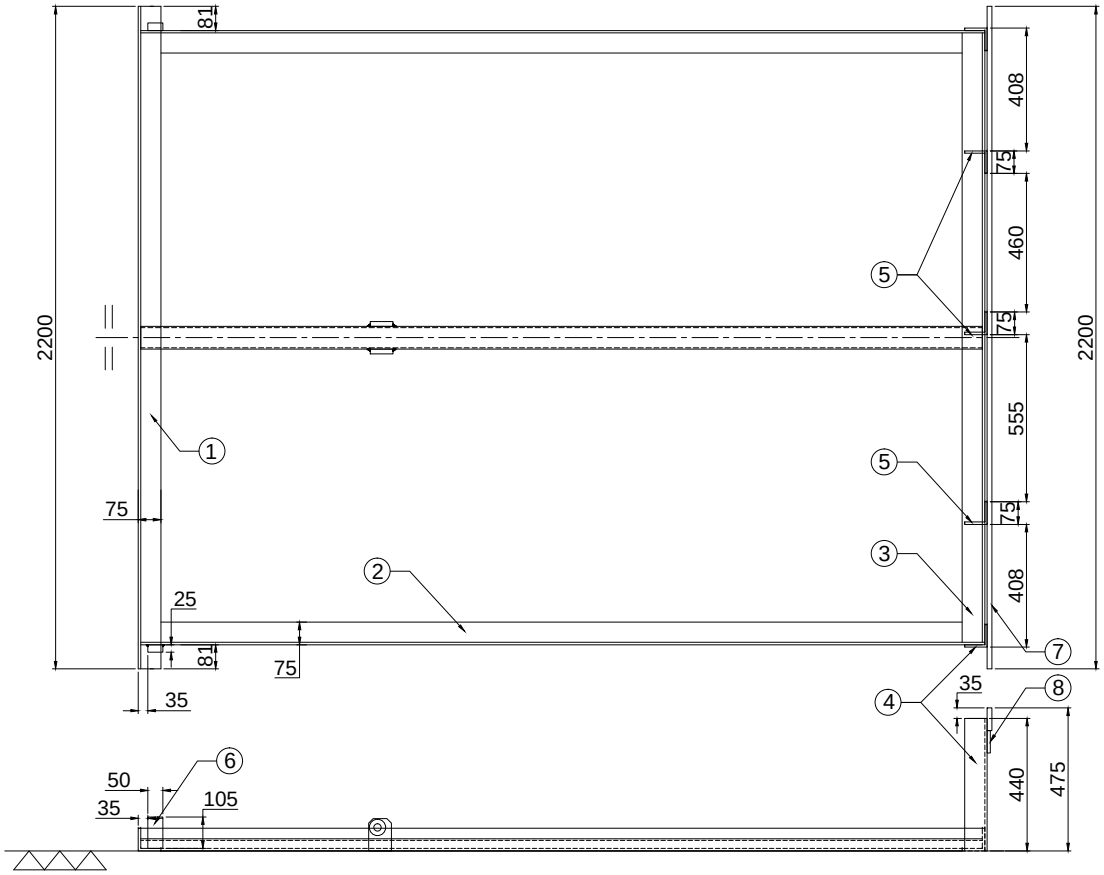

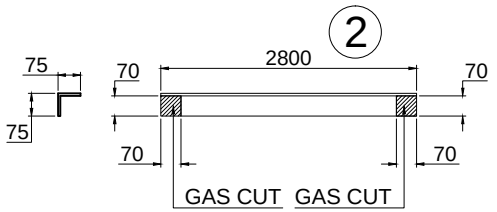

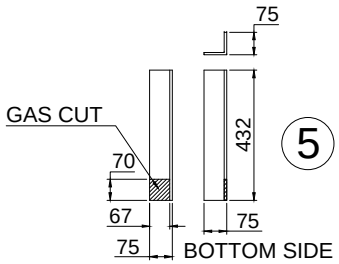

NOTE:~ MTL : MS

1. ISA 75 X 75 X 8 THK X 2200L = 1 NO
2. ISA 75 X 75 X 8 THK X 2800L = 2 NOS (NOTCH)
3. ISA 75 X 75 X 8 THK X 2025L = 1 NO
4. ISA 75 X 75 X 8 THK X 440L = 2 NOS
5. ISA 75 X 75 X 8 THK X 432L = 3 NOS (NOTCH)
6. FLAT 50 X 25 X 105L = 2 NOS (STOPPER)
7. FLAT 75 X16 X 2200L = 1 NO
8. FLAT 75 X10 X 75L = 5 NOS

This drawing & design is the property of NIHVA TECHNOLOGIES. Not to be sold or copied to any other concern.

TITLE: BOTTOM FRAME			NIHVA TECHNOLOGIES PVT. LTD. PUNE Tel : 020 66304033 Email:- info@nihva.com Website:- www.nihva.com
NAME	SIGN	DATE	
DRAWN P.A			CLIENT -
CHECK SHEKHAR			PROJECT - DLBJ1001
APPRD. SHEKHAR			SITE LOCATION -
If any queries contact : design@nihva.com			DWG. NO. : NIHVA/17-18/ REV- 0
ALL DIMENSION ARE IN mm			SCALE: NTS WT: SHEET: 01 OF 01