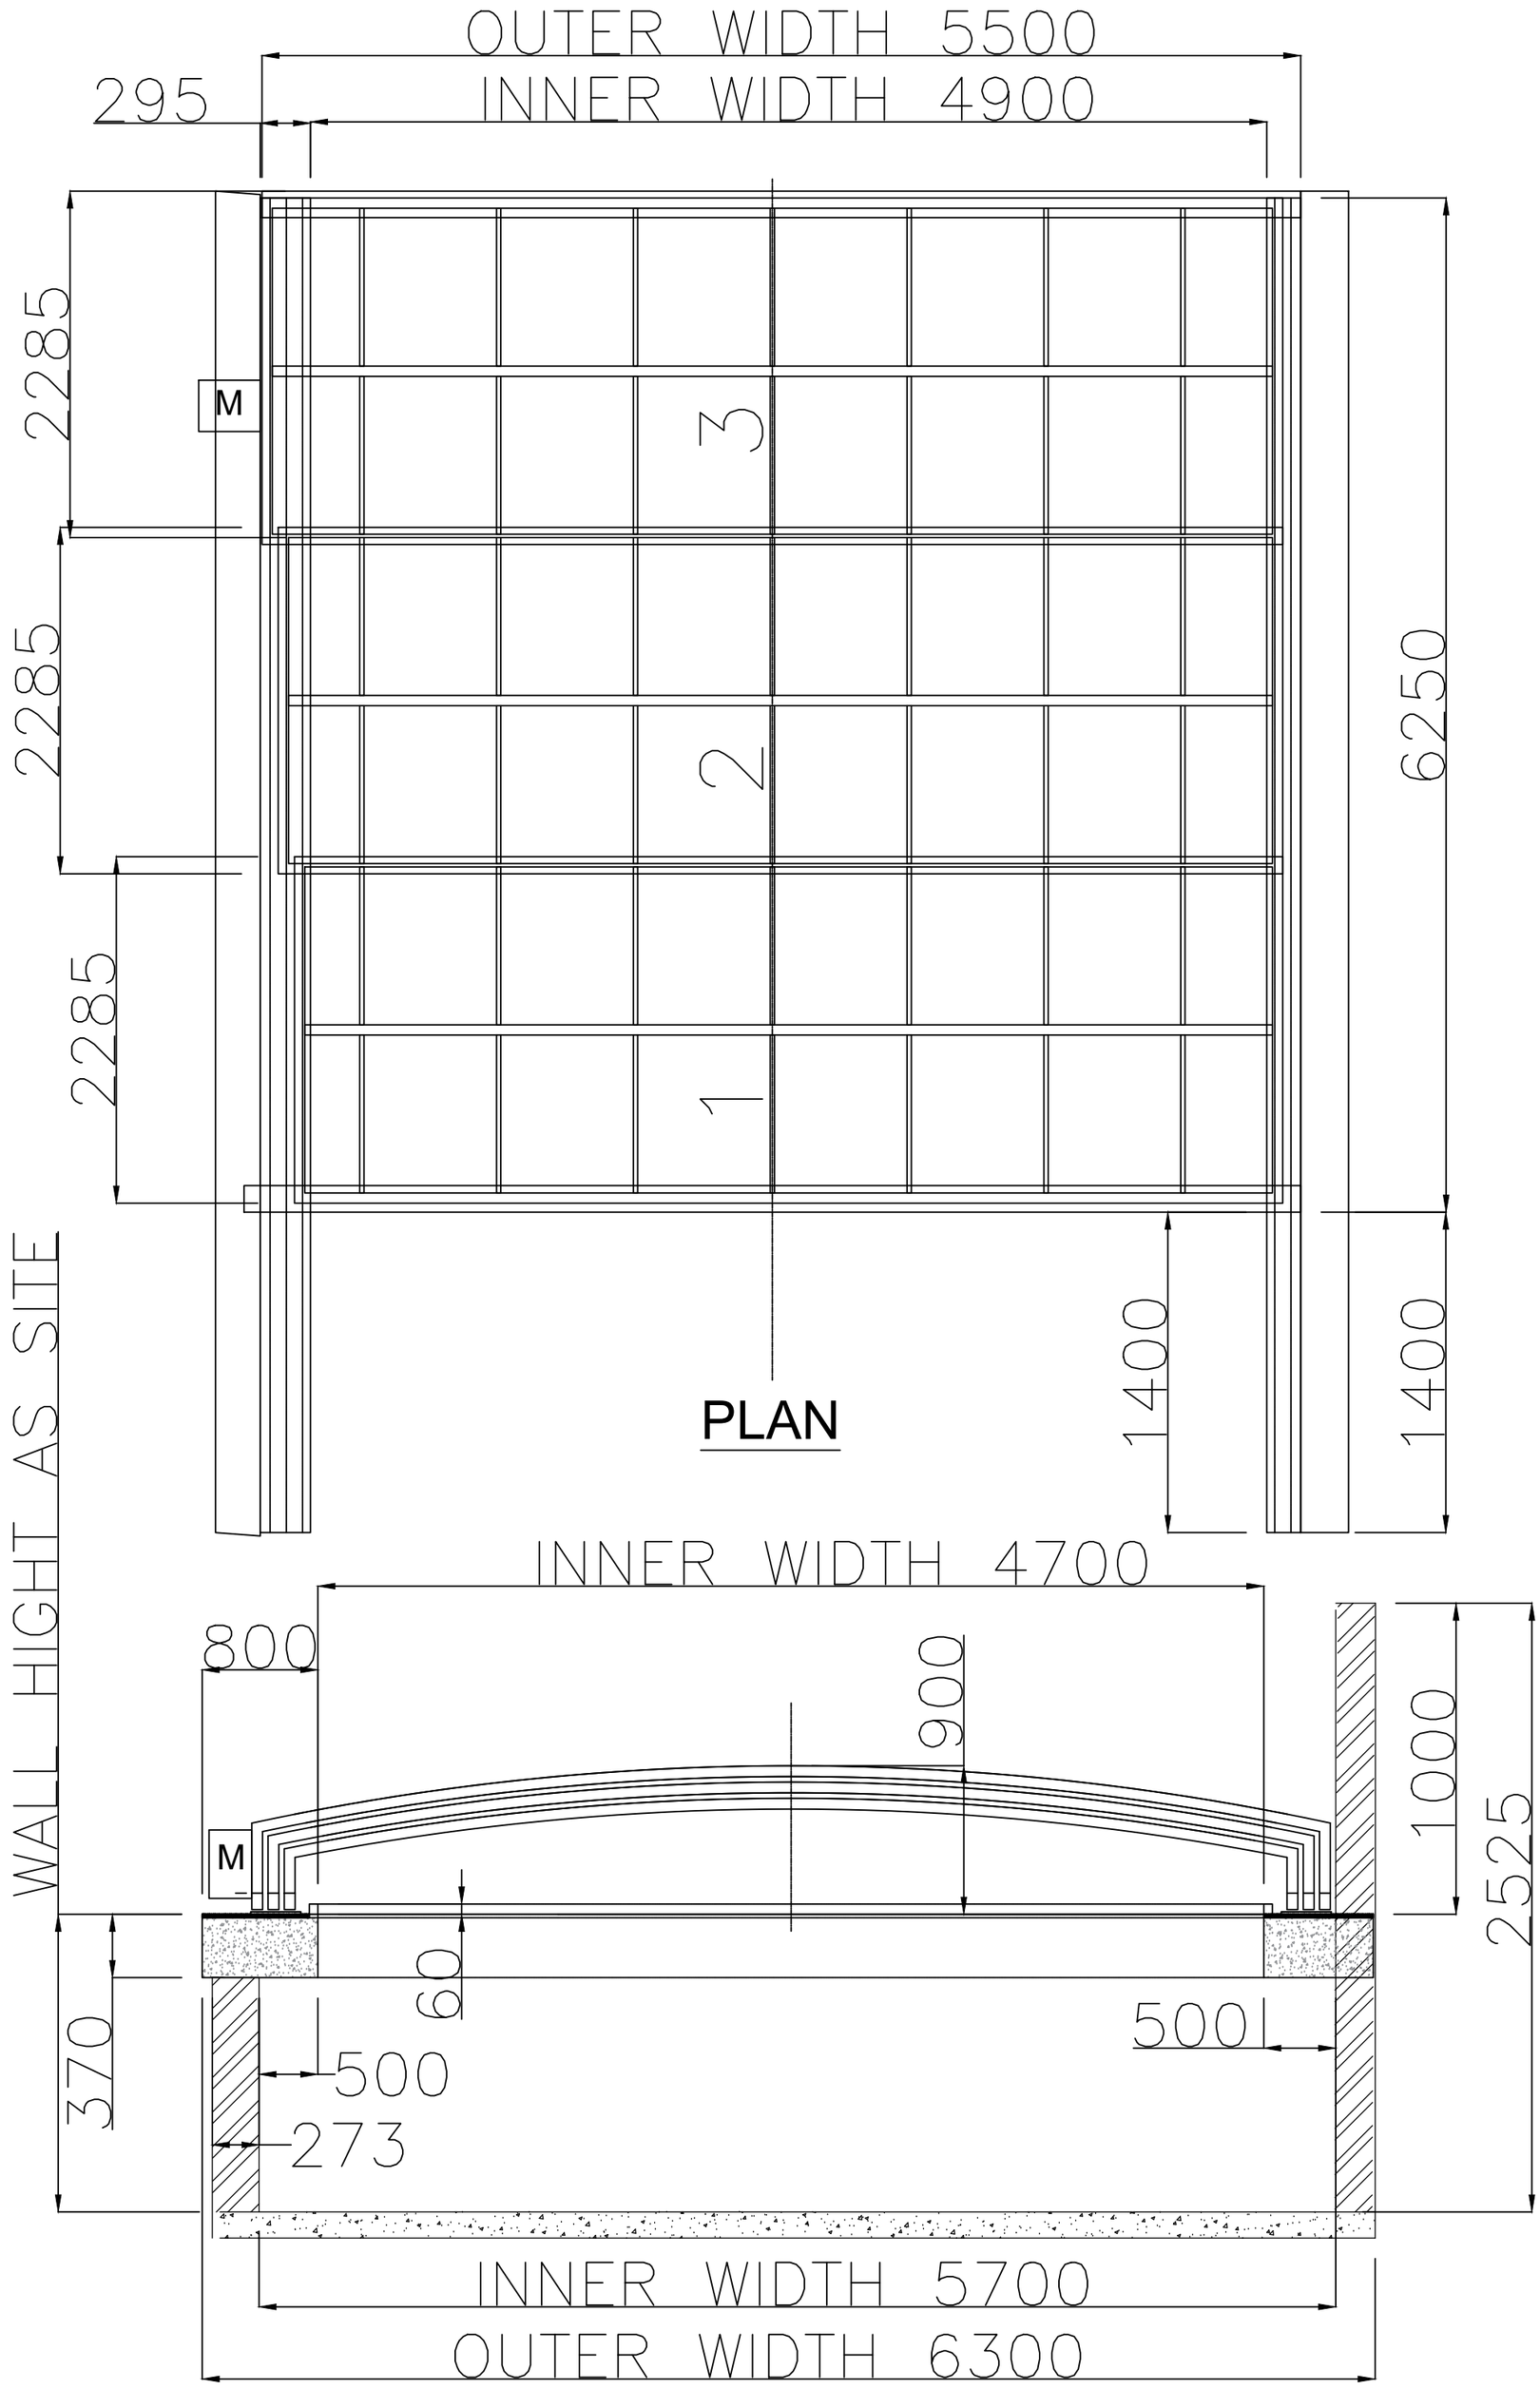


REV.	DESCRIPTION.	REVISED BY	SIGN	DATE
002	CHANGED TOP DIMENSIONS AS PER CLIENT REQUESTED: GROUND-MOUNT	MAHESH S.		19.11.22
000	RELEASED GA DWG FOR APPROVAL	MAHESH S.		27.10.22
001	CHANGED ROOF TYPE PER CLIENT: GROUND-WALLMOUNT TO BOTH GROUND	MAHESH S.		14.11.22

This drawing & design is the property of NIHVA TECHNOLOGIES. Not to be sold or copied to any other concern.

TITLE
ROOF LAYOUT

NIHVA
NIHVA TECHNOLOGIES PVT. LTD.

	NAME	SIGN	DATE
DRAWN	MAHESH S.		27.10.22
CHECK	MAHESH S.		27.10.22
APPRD.	VIJAY T.		27.10.22

CLIENT - AMIRUDEENZ

LOCATION - TIRUCHIRAPALLI

PRODUCT - RETRACTABLE ROOF

If any queries contact : projectsautomation@nihva.com

NIHVA\22-23\02XX

REV- 0

ALL DIMENSION ARE IN mm

SCALE: NTS

SHEET: 01 OF 01