


ELEVATION 01 - SLIDING GATE - 01

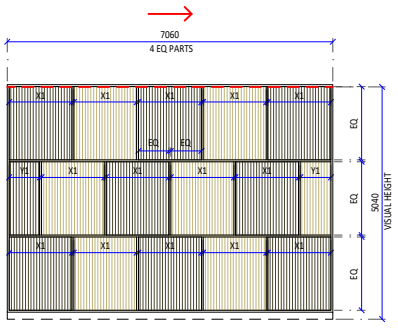


ELEVATION 01 - SLIDING GATE - 02

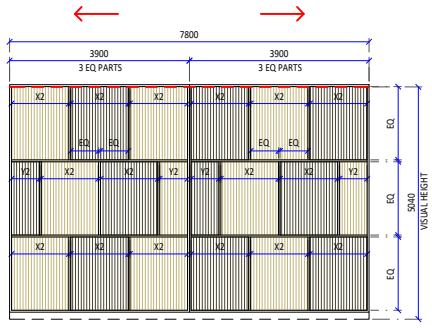


ELEVATION 01 - SLIDING GATE - 03

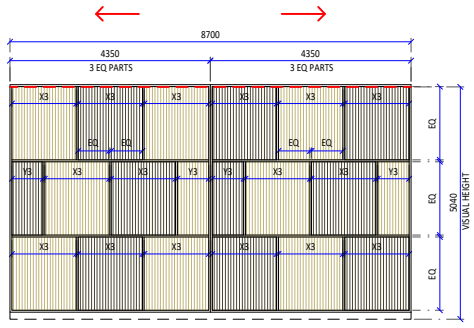


ELEVATION 01 - SLIDING GATE - 04

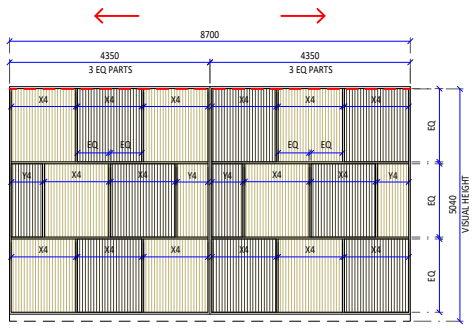


ELEVATION 01 - SLIDING GATE - 05

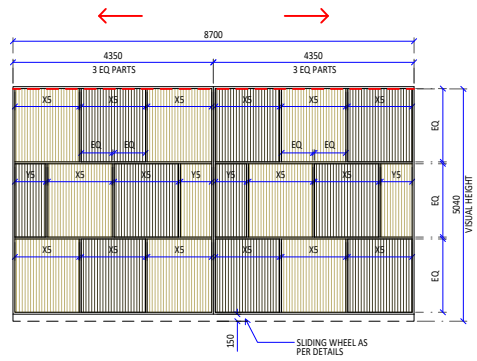


ELEVATION 01 - SLIDING GATE - 06

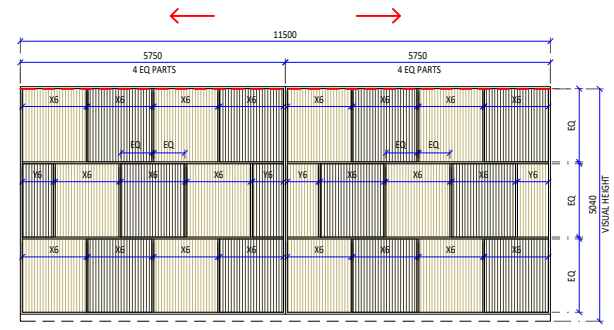


ELEVATION 01 - SLIDING GATE - 07

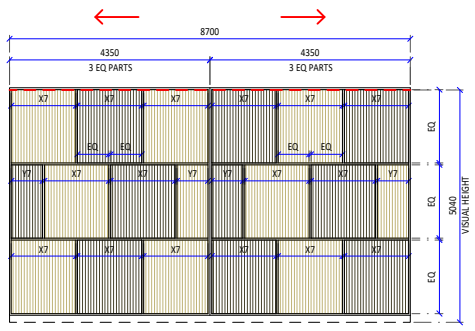


ELEVATION 01 - SLIDING GATE - 08

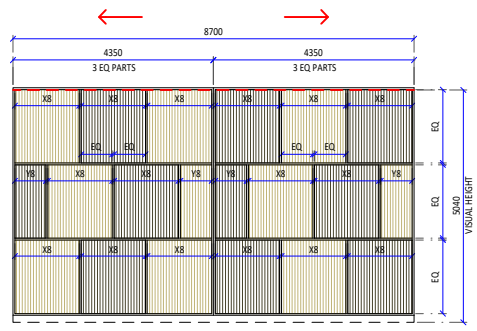


ELEVATION 01 - SLIDING GATE - 09

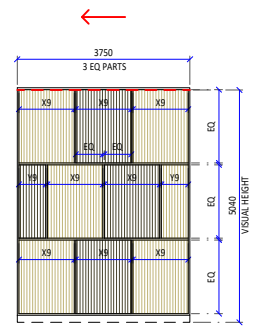

SECTION AA

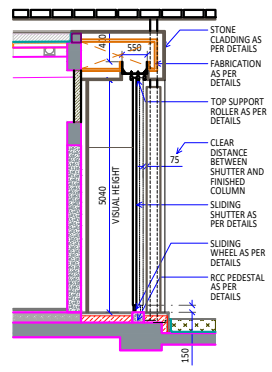

SLIDING GATE - PLAN SC - 1:150

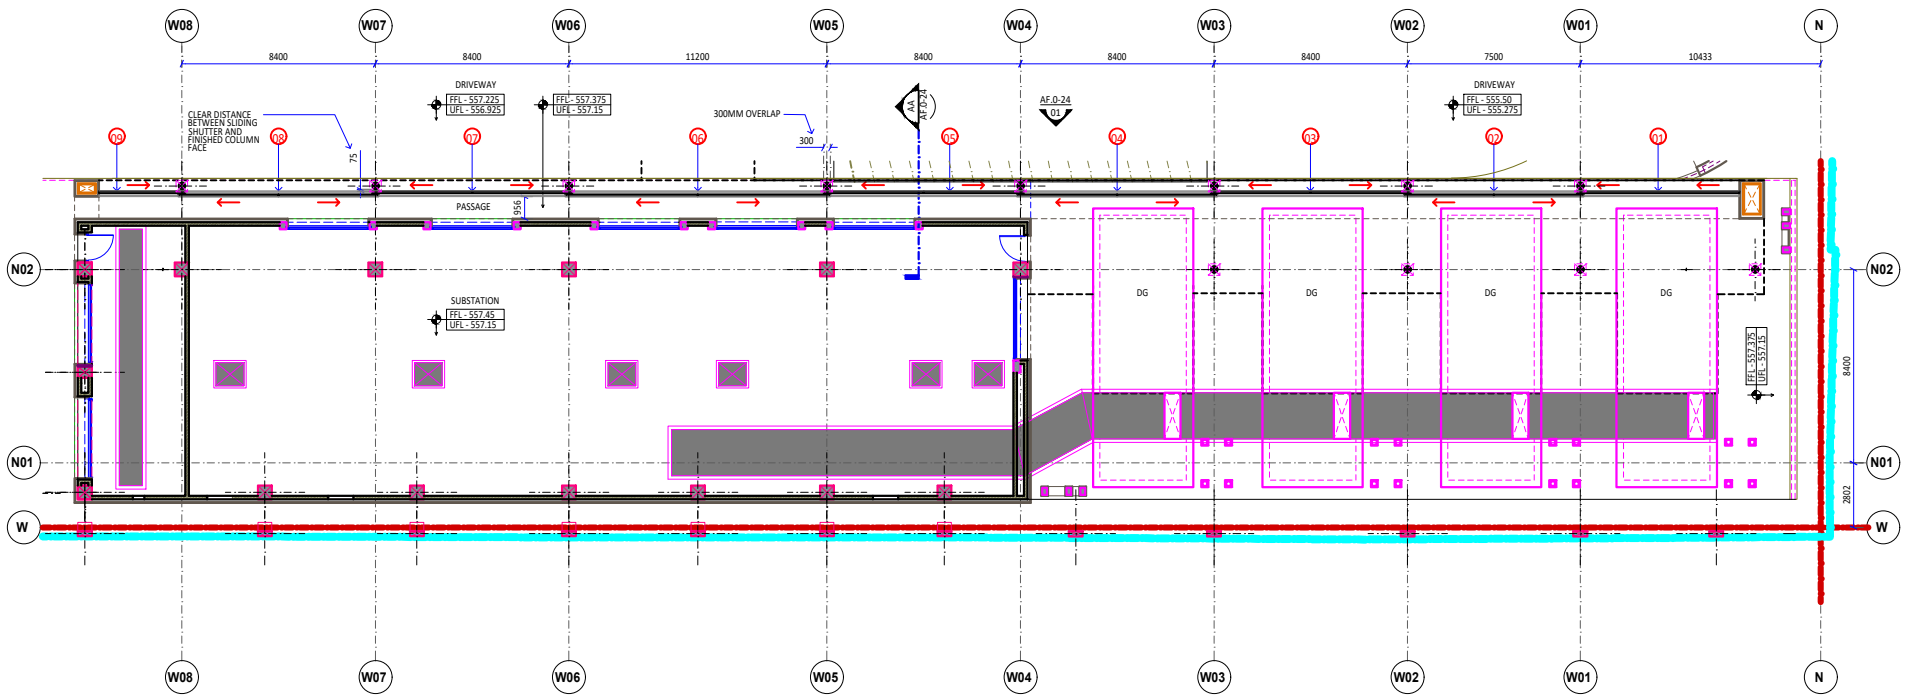

GENERAL NOTES :

1. ONLY WRITTEN DIMENSION TO BE FOLLOWED
2. ALL DIMENSIONS ARE IN MILLIMETER AND LEVELS ARE IN METERS UNLESS SPECIFIED.
3. ALL LEVELS ARE FROM UNFINISHED SURFACES.
4. FOR STRUCTURAL, SERVICES, LANDSCAPE AND INTERIOR, REFER RESPECTIVE CONSULTANT DRAWINGS.
5. DISCREPANCIES IF ANY TO BE BROUGHT TO THE NOTICE OF ARCHITECTS BEFORE EXECUTION.
6. THIS DRAWING IS THE PROPERTY OF A2Z ONLINE SERVICES/ PANCHSHIL AND IS NOT TO BE REPRODUCED, COPIED OR HANDED OVER TO THIRD PARTY OR NOT TO BE USED FOR ANY OTHER PURPOSE OTHER THAN FOR WHICH T HAS BEEN LOANED.

REFER THIS DRAWING ONLY FOR SLIDING SHUTTER ARCHITECTURAL DETAILS

PLEASE CONSIDER 300MM OVERLAP BETWEEN TWO SLIDING SHUTTERS


REFER VENDORS SHOP DRAWINGS FOR DETAILS

CONSULTANT'S DWG:

SR. NO	CONSULTANT	DRAWING NAME/ NO.	DATE OF DRAWING	
01	SLIDING GATE VENDOR			
02	STRUCTURAL CONSULTANT			

NOTE:
READ THIS DRAWING IN CO-ORDINATION WITH THE ABOVE DRAWINGS

KEY PLAN :

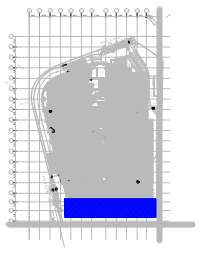

LEGEND :

LOUVERS OPENING IN EAST DIRECTION

LOUVERS OPENING IN WEST DIRECTION

01 SLIDING GATE NUMBER

SLIDING DIRECTION

DRAWING STATUS :

FOR INFORMATION ONLY

PANCHSHIL REALTY
Pune: Tech Park One, Tower "E", 191 Yerwada, Pune 411 006

REVISIONS

REV.NO.	DATE	DESCRIPTION	DRN BY	CHKD BY

REVISIONS

REV.NO.	DATE	DESCRIPTION	DRN BY	CHKD BY

DATE: 02-09-24

DEALT : K.M.

DRAWN BY: N.D.

N

SCALE: 1:75

PROJECT : 40-KHARADI

DRAWING TITLE : DG AND SUBSTATION SLIDING SCREEN DETAILS

JOB NO. PAN-2024

DRAWING NO. 2024- AF.0-24

REVISION NO. D0