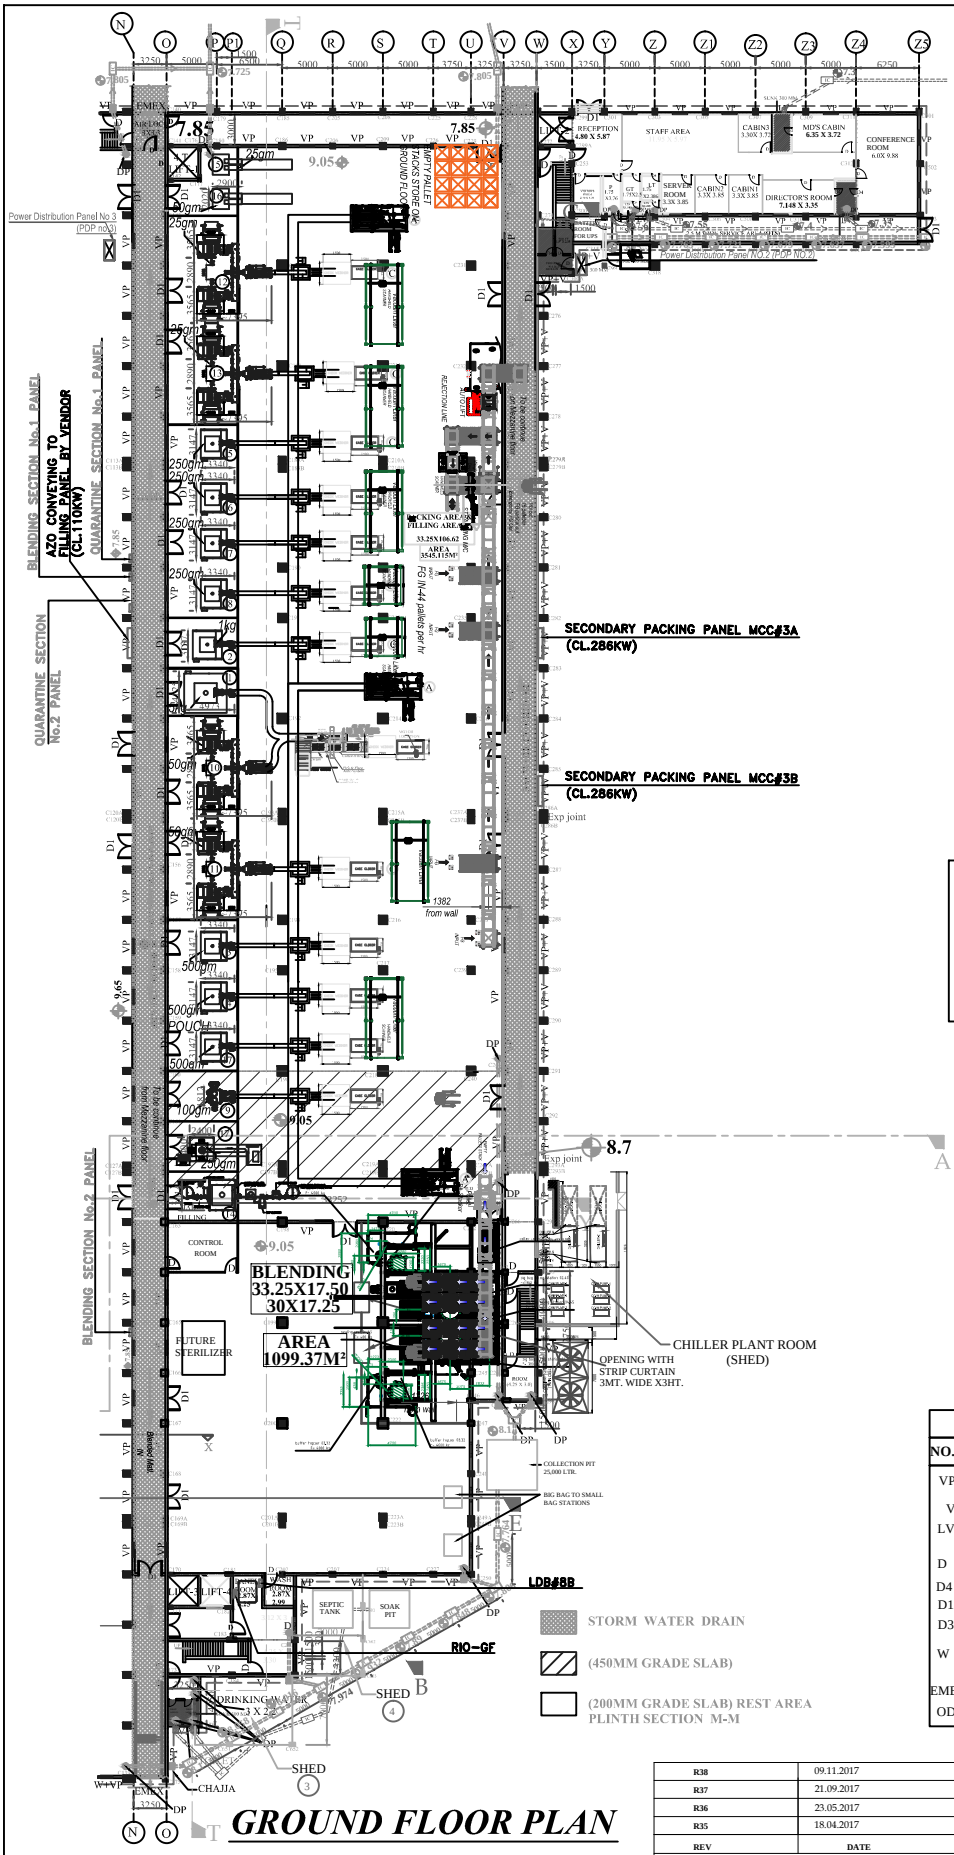


GROUND FLOOR PLAN

LEGEND


LT = LADIES TOILET
GT = GENTS TOILET
SA = SERVICE AREA
P = PANTRY
T = TOILET

LEGEND

GULLY TRAP-GT
INSPECTION CHEMBER-IC
DOMESTIC LINE SHOWN
EFFLUENT LINE SHOWN

LEGEND

EFFLUENT DRAIN
DOMESTIC DRAIN

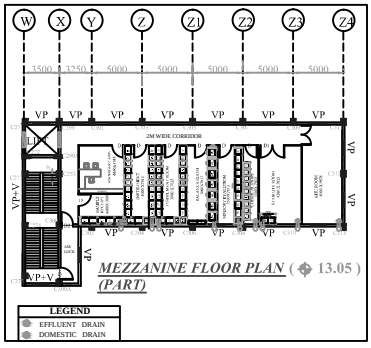

DOOR WINDOW SCHEDULE

NO. M	DESCRIPTION	SIZE (M)
VP	FIXED DOUBLE FLUSH AL.VIEW PANEL	1.95X1.2
V	FIXED DOUBLE FLUSH AL.VIEW PANEL	1.95X1.5
LV	LOUVERED VENTILLATOR (OPENABLE) WITH NETION NET	0.6X0.9
D	FLUSH ALUMINIUM SINGLE DOOR	1.2X3.0
D4	FLUSH ALUMINIUM SINGLE DOOR	0.9X3.0
D1	FLUSH ALUMINIUM DOUBLE DOOR	2.4X3.0
D3	FLUSH ALUMINIUM DOUBLE DOOR	3.0X3.0
W	SLIDING WINDOW AL. WINDOW WITH NETION NET	1.95X1.5
EMEX	EMERGENCY EXIT	1.2X2.5
OD	AUTO VERTICAL SLIDING DOOR	3.0X3.0

REV	DATE	DESCRIPTION
R38	09.11.2017	CHANGE MACHINERY IN FILLING PACKING, PANEL ADDED
R37	21.09.2017	CHANGE MACHINERY
R36	23.05.2017	MARK LEAN TO SHED
R35	18.04.2017	CHANGE MACHINERY & CHANGE BLENDING AREA MACHINERY

D R G NO - DTS/272/11(38)
DATE - 29.04.2015
SCALE - 1:100
DRNBY - NSP
JOB TITLE - PROPOSED WORK FOR M/S AMAR FOOD & BEVARAGES A DIV OF AMER TEA PLANTATION Pvt ltd
OWNER - M/S AMAR TEA PLANTATION PVT LTD
TITLE OF DRG - ARCH. GROUND FLOOR PLAN

NORTH

ARCHITECT
MINAL MEHTA
COUNCIL OF ARCHITECTURE. (GOVT. OF INDIA) REGN.NO -CA/93/16194

PROJECT MANAGEMENT CONSULTANTS
DEV TECHNOSKILLS
413, HILL VIEW IND.PREMISES
AMRUTNAGAR RD
GHATKOPAR (W)
MUMBAI 86