



TOP VIEW

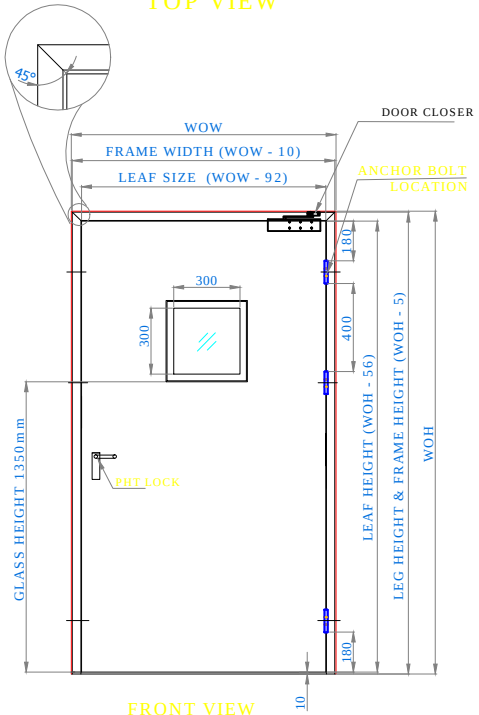

FRONT VIEW




SIDE VIEW
SECTION A-A'

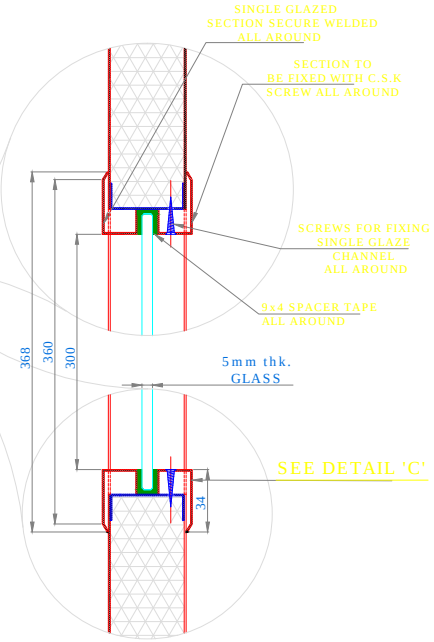


SINGLE GLAZE FIXING DETAIL

NOTE :
1. DOOR HINGES : GEZE MAKE.
2. DOOR CLOSER : GEZE MAKE.
3. DOOR EXTERNAL TRIM : YELE MAKE.

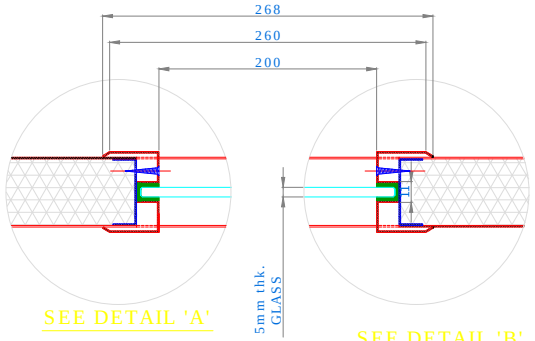



SEE DETAIL 'A'

SEE DETAIL 'B'

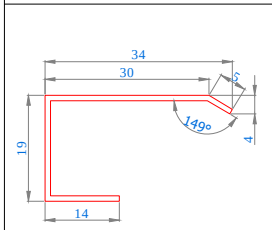


SEE DETAIL 'C'

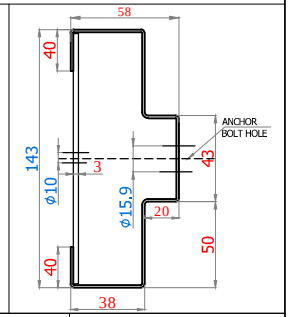

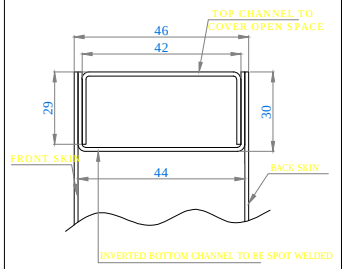

DOOR TOP SECTION DETAIL

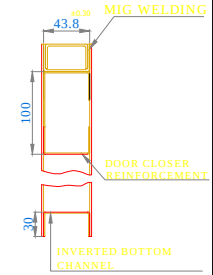

DOOR BOTTOM & TOP DETAIL

NOTE :
1. Up to 2 hours fire resistance in accordance with BS 476 part 22, UL 10B & UL 10C dependent on construction.
2. CORES : Honeycomb Paper.

SR. NO	WALL OPENING WIDTH	WALL OPENING HEIGHT	QTY	RAL	HARDWARE
01	1000	2400	07	9002	Single leaf metal door with Vision Panel, Hinges , Door closer ,with external trim

TOLERANCE - ±05mm

This drawing & design is the property of NIHVA TECHNOLOGIES. Not to be sold or copied to any other concern.

TITLE: SINGLE LEAF FIRERATED STEEL DOOR

NIHVA TECHNOLOGIES PVT. LTD.

NIHVA TECHNOLOGIES PVT. LTD. PUNE
Tel : 020 66304033
Email:- info@nihva.com
Website:- www.nihva.com

	NAME	SIGN	DATE
DRAWN	P.V.A		25.03.2019
CHECK	V.M.T		25.03.2019
APPRD.			

CLIENT - UNITED ARCHITECT
PROJECT - A RAYMOND
SITE LOCATION - CHAKAN
If any queries contact : design@nihva.com
DWG. NO. : NIHVA/18-19/0312
REV- R00
ALL DIMENSION ARE IN mm
SCALE: NTS
WT:
SHEET: 01 OF 01