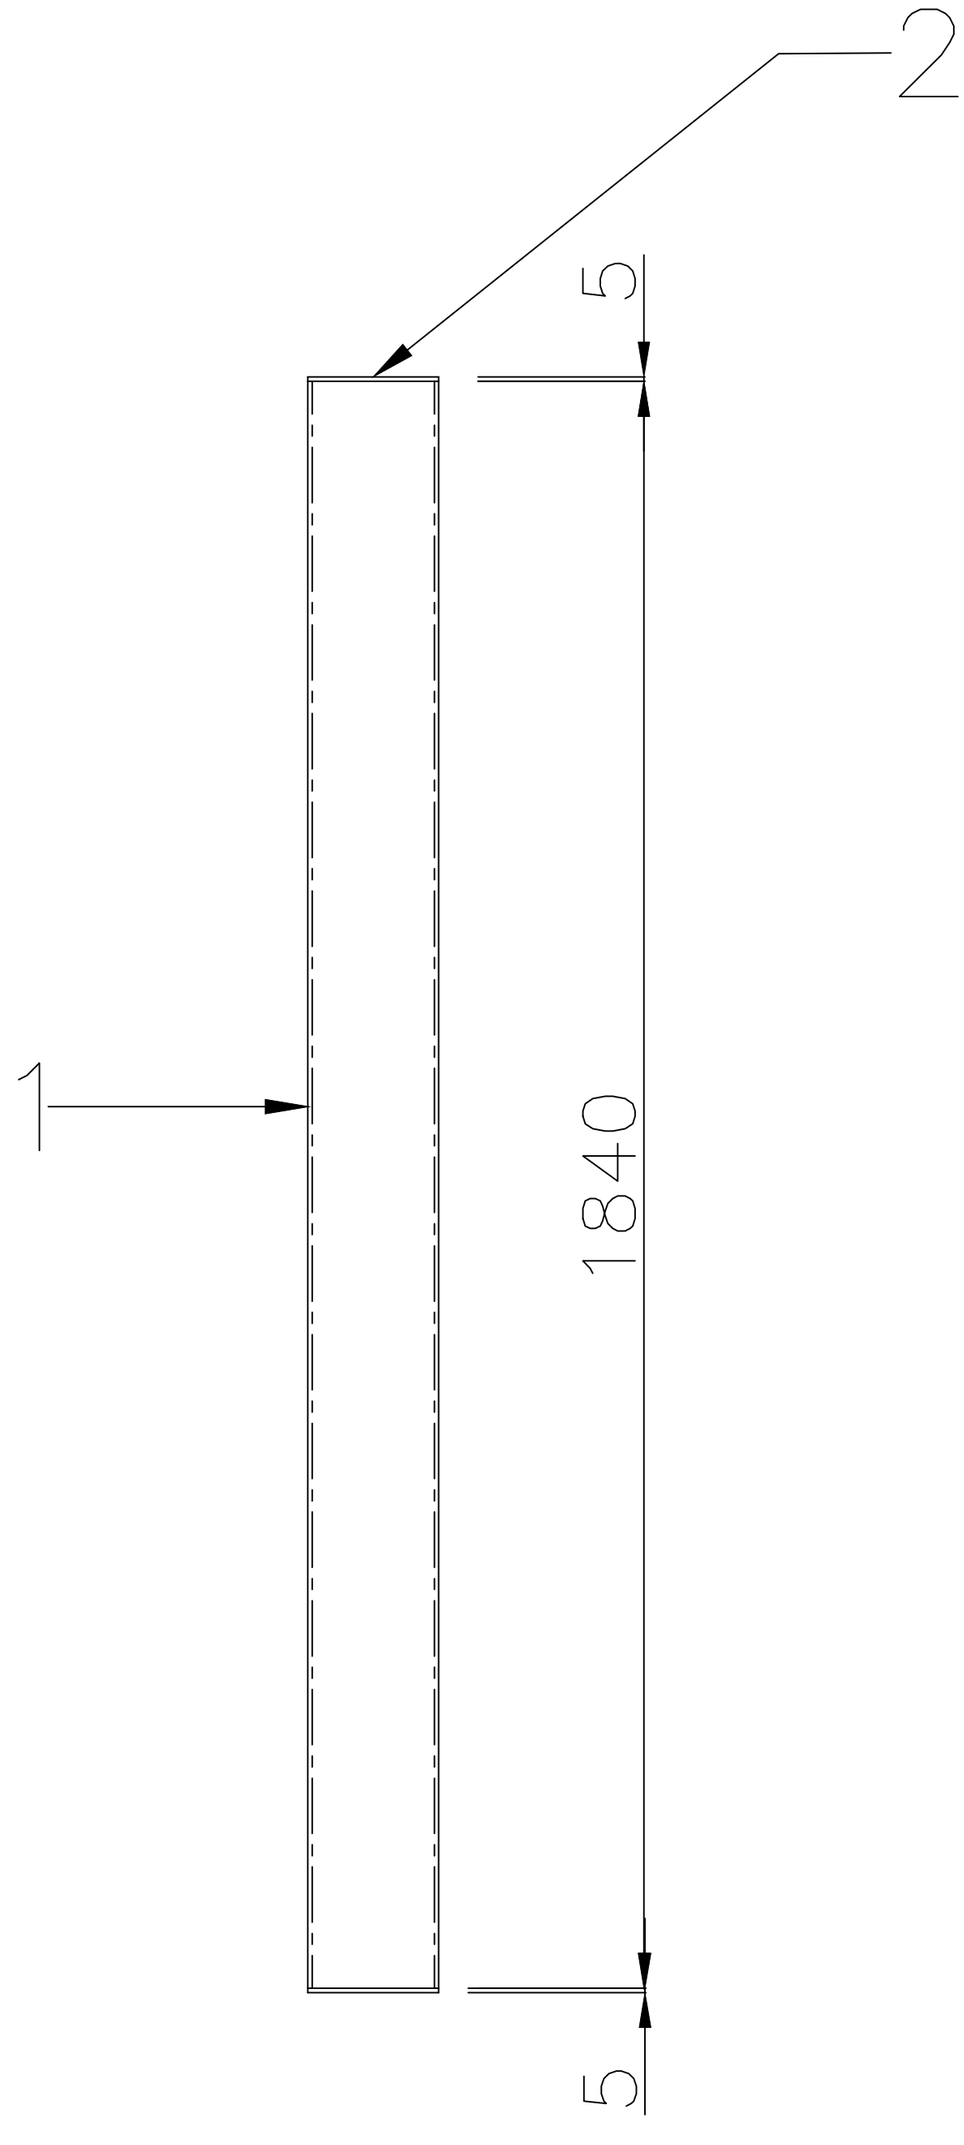

SR. NO.	DESCRIPTION	SPECIFICATION	QTY
1	SQ. TUBE	150 X 150 X5, 1840 LENGTH	1 NOS
2	SQ. plate	150 X 150 X5 thk	2 NOS

This drawing & design is the property of NIHVA TECHNOLOGIES. Not to be sold or copied to any other concern.

TITLE
Sliding gate extension tube

NIHVA TECHNOLOGIES PVT. LTD.

NIHVA TECHNOLOGIES PVT. LTD. PUNE
Tel : 020 66304033
Email:- info@nihva.com
Website:- www.nihva.com

	NAME	SIGN	DATE
DRAWN	G.P.		03.02.22
CHECK	A.K.		03.02.22
APPRD.	V.T.		03.02.22

CLIENT -HAIMAVATHY PROPERTIES PVT. LTD.

LOCATION - MUMBAI

PRODUCT -

If any queries contact : design@nihva.com

NIHVA\21-22\MFG\018 REV- 00

ALL DIMENSION ARE IN mm

SCALE: NTS

SHEET: 01 OF 01