


ELEVATION


SCALE 1:50

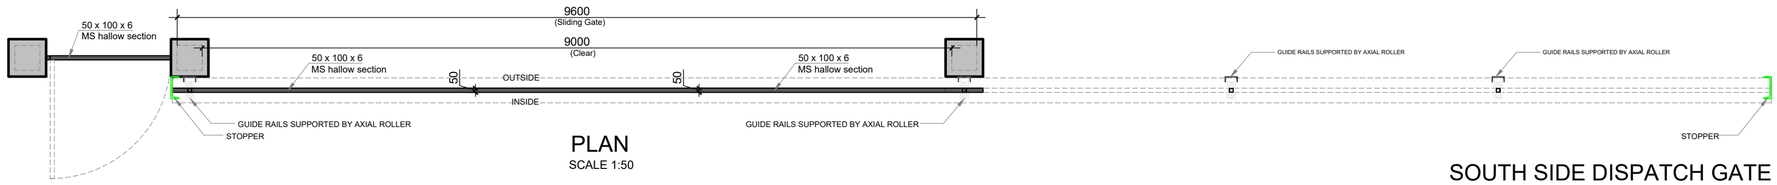

PLAN


SCALE 1:50

SOUTH SIDE DISPATCH GATE

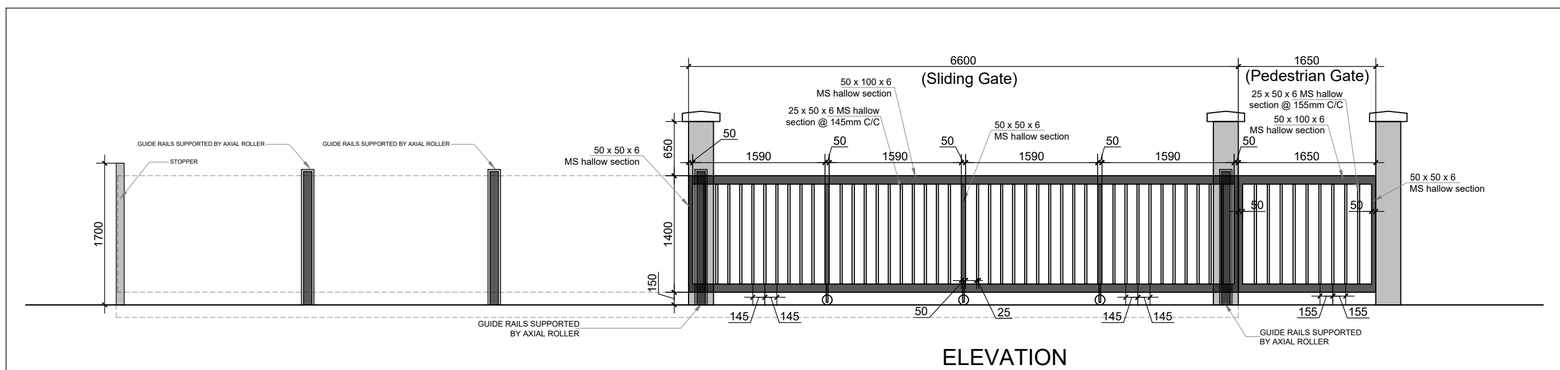

ELEVATION


SCALE 1:50

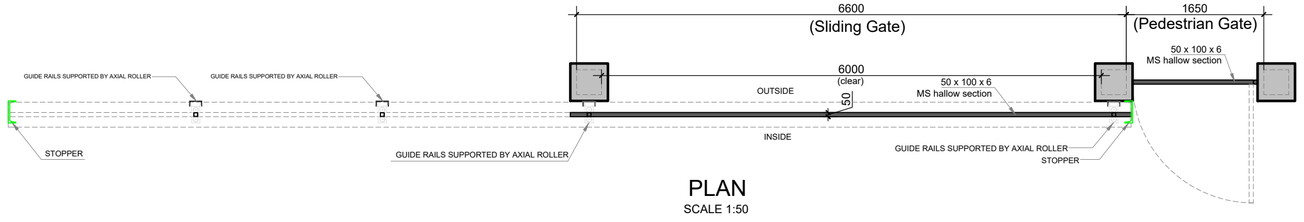

PLAN

SCALE 1:50

WEST SIDE ENTRANCE GATE

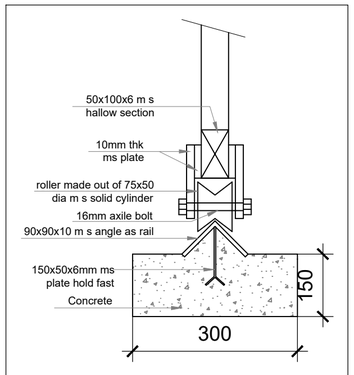

DETAIL AT A

Rev.No.	Date	Revision Description
R0	11.11.2025	Released for Approval

Standard Notes :

1. All dimensions are in Millimeters. Drawing shall not be scaled.
2. All dimensions shall be verified on site before executing on site & follow the written dimensions only.
3. Any discrepancy shall immediately be brought to notice of Architect.
4. This drawing shall be read in conjunction with all the other technical/ structural/ electrical & services drawings & details.
5. This drawing shall only be used after its plans are approved by local authority/ municipal corporation / T.P. office / any other concern authority.
6. The copyright of design & its drawing remains with M/s. RASS Project Consultant Pvt.Ltd.

STAMP & SIGN

CLIENT :

M/s. LESER India Private Limited
(formerly as Fainger LESER Valves Private Limited)
Plot no. D -3 & D-2/2, MIDC, Paithan,
Chatrapati Sambhajinagar - 431148.
Maharashtra, India.

DESIGN CONSULTANTS :

RASS Project Consultants Private Limited
Office No. 01 & 16, 1st Floor, KJ Tower,
Wing A, above Meera Hyundai,
Pune - Bangalore Highway, Warje, Pune 411058
Maharashtra, India.

DESCRIPTION OF PROPOSAL & PROPERTY :

Proposed Expansion of Factory on Plot No. D-3, MIDC,
Paithan, Chatrapati Sambhajinagar - 431148.
Maharashtra, India.

CONTENT OF SHEET :

SLIDING GATE GA DRAWING

DRG.NO : LIPL_GA_ARCH_SLIDING GATE_R0

Released By:	AAN			
Checked By:		11.11.2025	A2-1:50	LIPL/24-25/04
Drawn By:	AAN	DATE	SCALE	JOB.NO.
Design By:				