

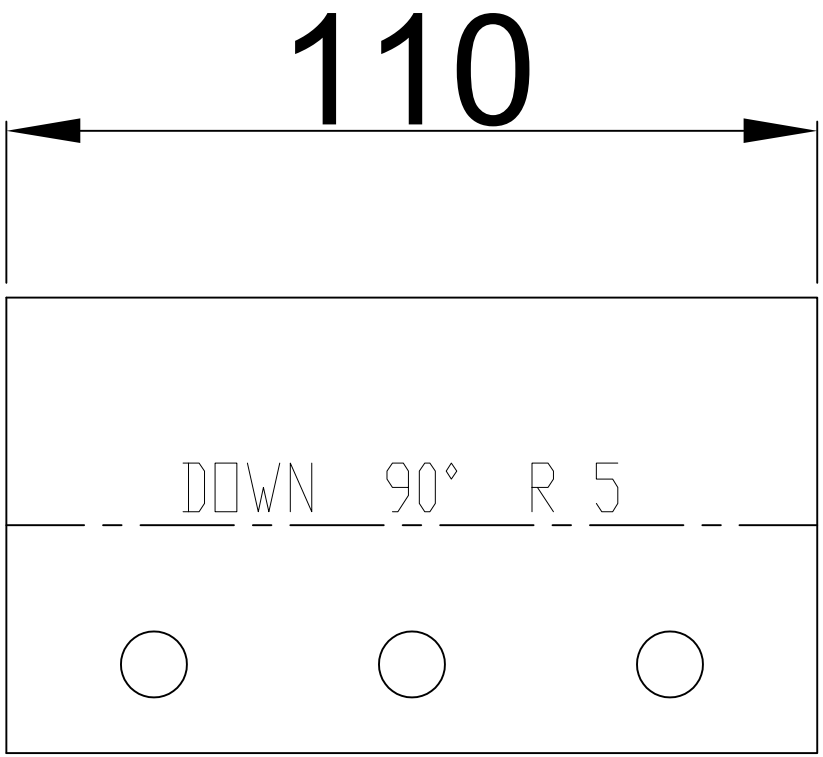


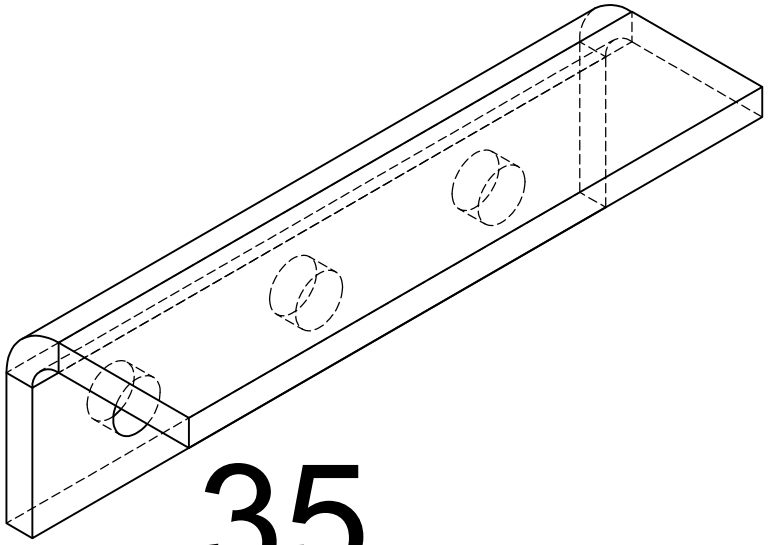

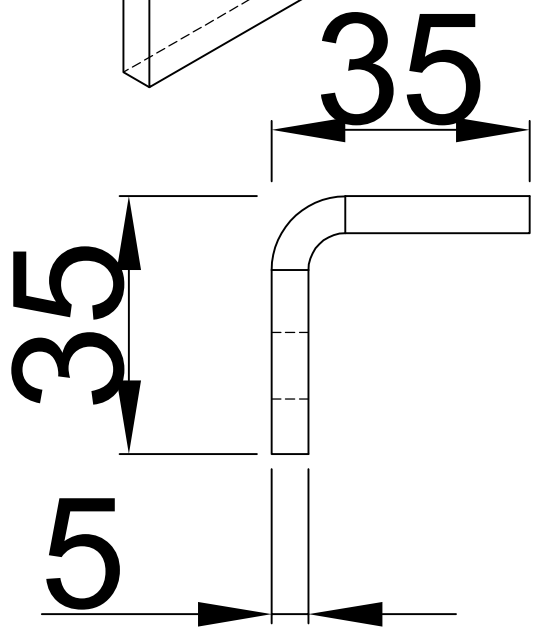

L BKT -02
MATL-MS
QTY-16
DRG NO-01-10

TITLE:- L BKT-02				NIHVA TECHNOLOGIES PVT. LTD. PUNE Tel : 020 66304033 Email:- info@nihva.com Website:- www.nihva.com		
	NAME	DATE	SIGN			
DRAWN	KISHAN	18/07/22		CLIENT - NIHVA TECHNOLOGIES PVT.LTD		
CHECK	G. JAIN	18/07/22		LOCATION -		
APPRD.	V. TARAK			PRODUCT - RETRACTABLE ROOF		
If any queries contact : design@nihva.com				DWG NO:-NIHVA/22-23/MFG/0035		REV- 0
ALL DIMENSION ARE IN mm				SCALE: NTS	SCALE:-- 1:1	SHEET: 01 OF 01

SR NO.	REV NO.	Date	Revised By