
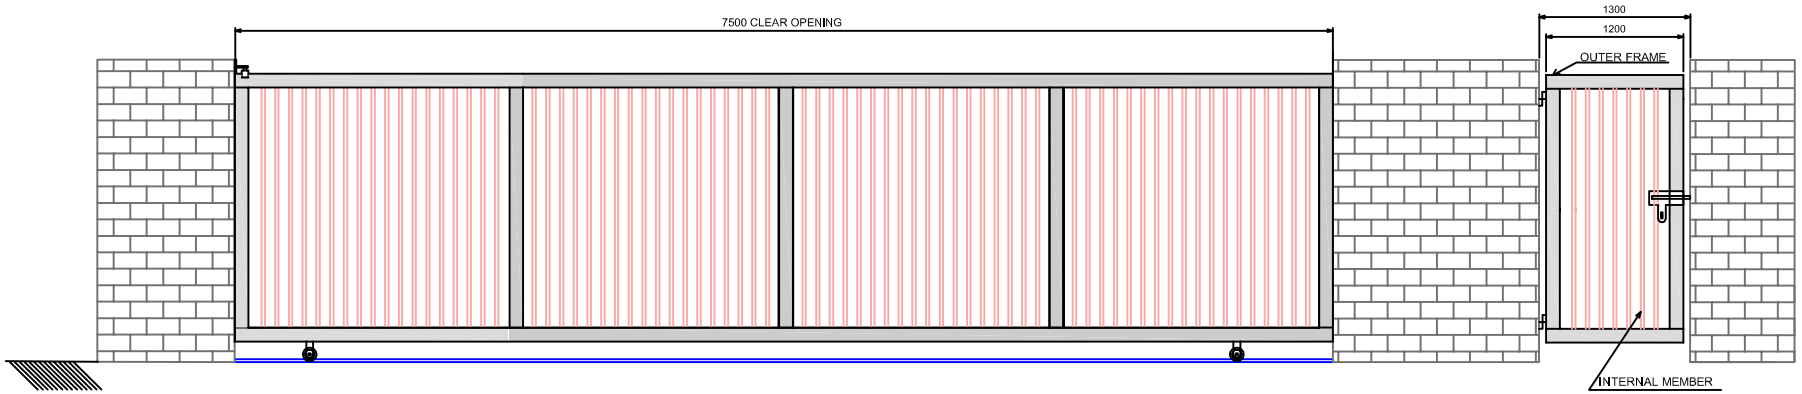



OUTSIDE VIEW

SLIDING DIRECTION →

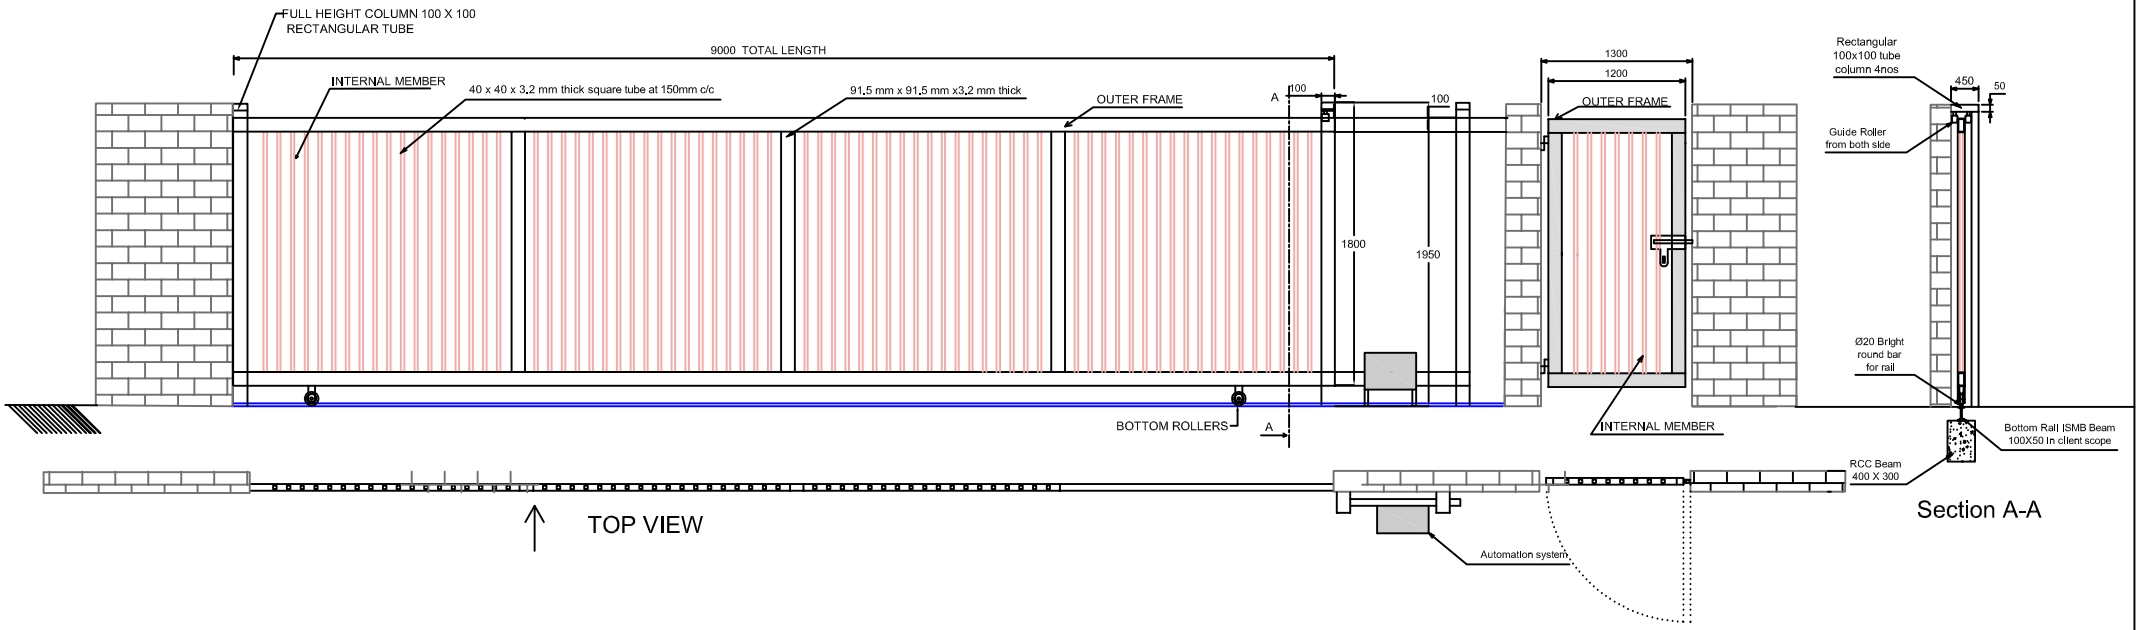


TOP VIEW

Section A-A

Sliding gate size - 7500X1800mm(Clear opening)
Total length of gate - 9000mm
Wicket gate size - 1200X1800mm
No. Of Column - 4 nos.
Factory paint finish - Red oxide primer coat

| | | | | | |
|---|---|---|---|---|---|
| Drawn By:-A.K | Checked By | Approved By - Date | | Date 23-07-14 | Scale NTS |
| NIHVA TECHNOLOGIES PVT. LTD. | | | CLIENT — PMP Drive system Pvt Ltd. | | |
| | | | DRG. No.NVA/PMP/07/14-15 | Revision 00 | Sheet 1-1 |