




VIEW 1-1

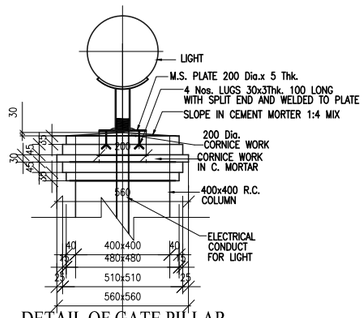


DETAIL OF GATE PILLAR
TOP CORRNICE WORK

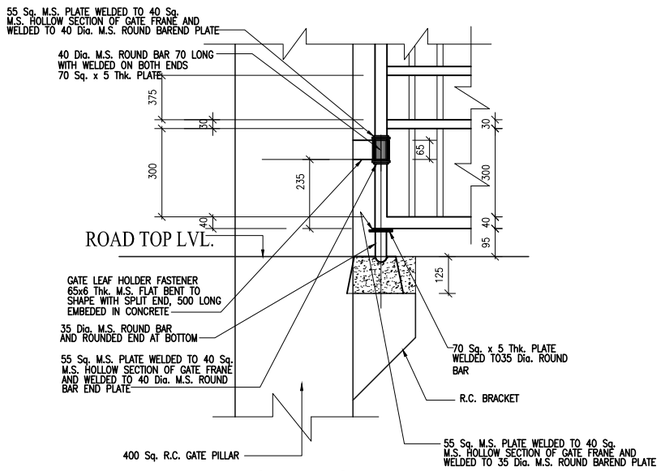


DETAIL AT Z

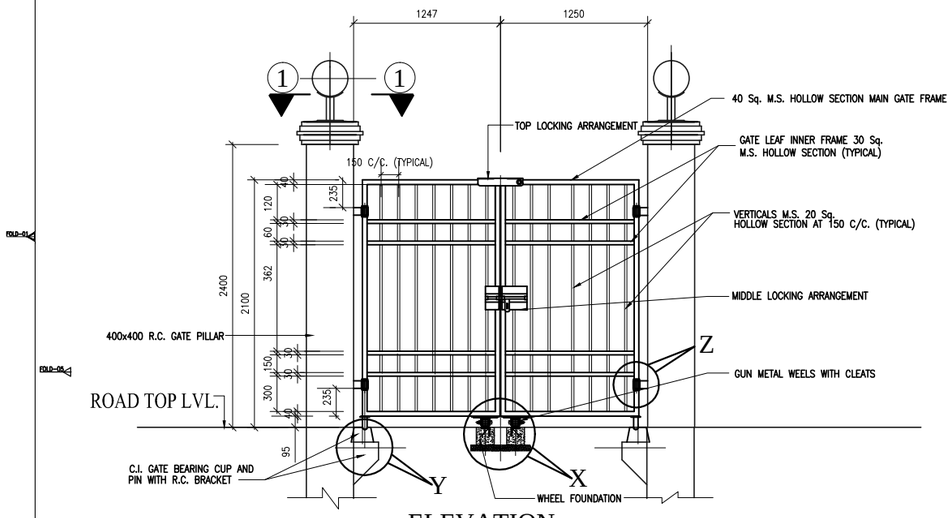


ELEVATION

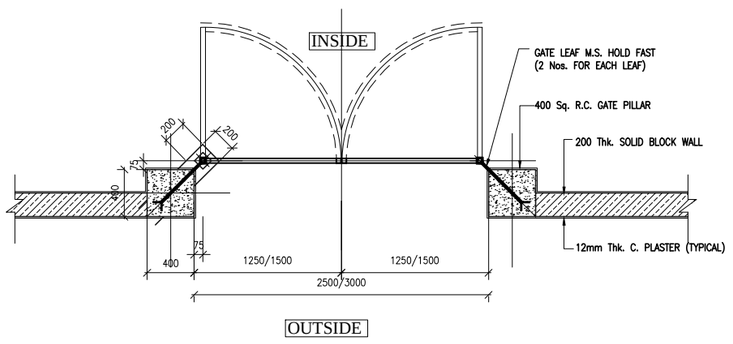

PLAN

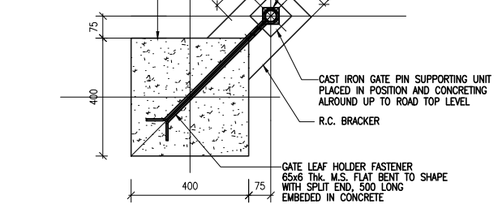


DETAIL AT Y

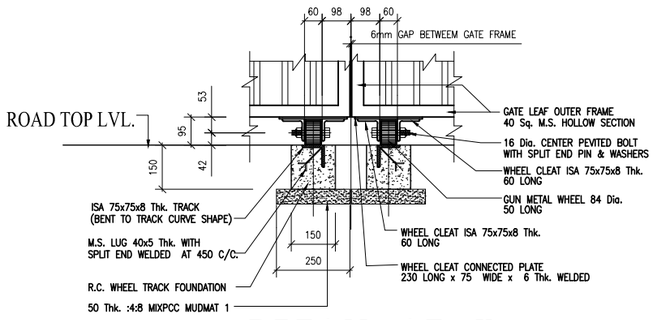

DETAIL AT X

KEY PLAN :-

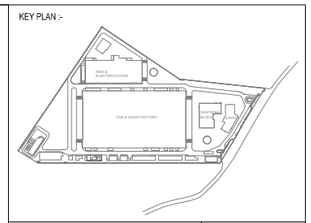

N

GENERAL NOTES :

- ALL DIMENSIONS ARE IN MILLIMETRES AND ARE UNFINISHED DIMENSIONS UNLESS OTHERWISE SPECIFIED.
- ALL LEVELS ARE IN METRES AND ARE UNFINISHED LEVELS UNLESS OTHERWISE SPECIFIED.
- DO NOT SCALE DRAWINGS. ONLY WRITTEN DIMENSIONS SHALL BE FOLLOWED. ANY DISCREPANCIES NOTED SHALL BE BROUGHT TO THE NOTICE OF THE ARCHITECT PRIOR TO EXECUTION.

REV.	DESCRIPTION	DATE	BY	CHD.
T2	ISSUED FOR TENDER	02.03.17	SV	VA
T1a	ISSUED FOR CLIENT REVIEW	25.11.16	SV	VA
T1	ISSUED FOR TENDER	01.04.15	MB	VA

AMENDMENT

GRAPHIC SCALE: 0 1M 4M 8M / 1M 0 2M 6M 10M

CLIENT:
KONE ELEVATOR INDIA PVT. LTD.

PROJECT:
PROPOSED KONE ELEVATOR FACTORY AT PILLAIPAKKAM, NEAR CHENNAI.

DRAWING TITLE:
STANDARD DETAILS - 08
OPENABLE GATE DETAIL

SCALE : 1:25 ; 1:10	DRAWN : V.A.	REV
DATE : 18.02.2015	CHKD : V.R.	

DRAWING NO:
KEIPL-P-FAC-AR20-08-01-189952 — T2

ARCHITECTURE • INTERIOR DESIGN • ENGINEERING • PLANNING • CONSTRUCTION MANAGEMENT
C R NARAYANA RAO
10, KARPAGAMBAL NAGAR, MYLAPORE, CHENNAI-600 004
B.Arch. (Hons.), M.Arch., (Calif.), F.I.I.A., Intl.Assoc.A.I.A., Registered Architect.