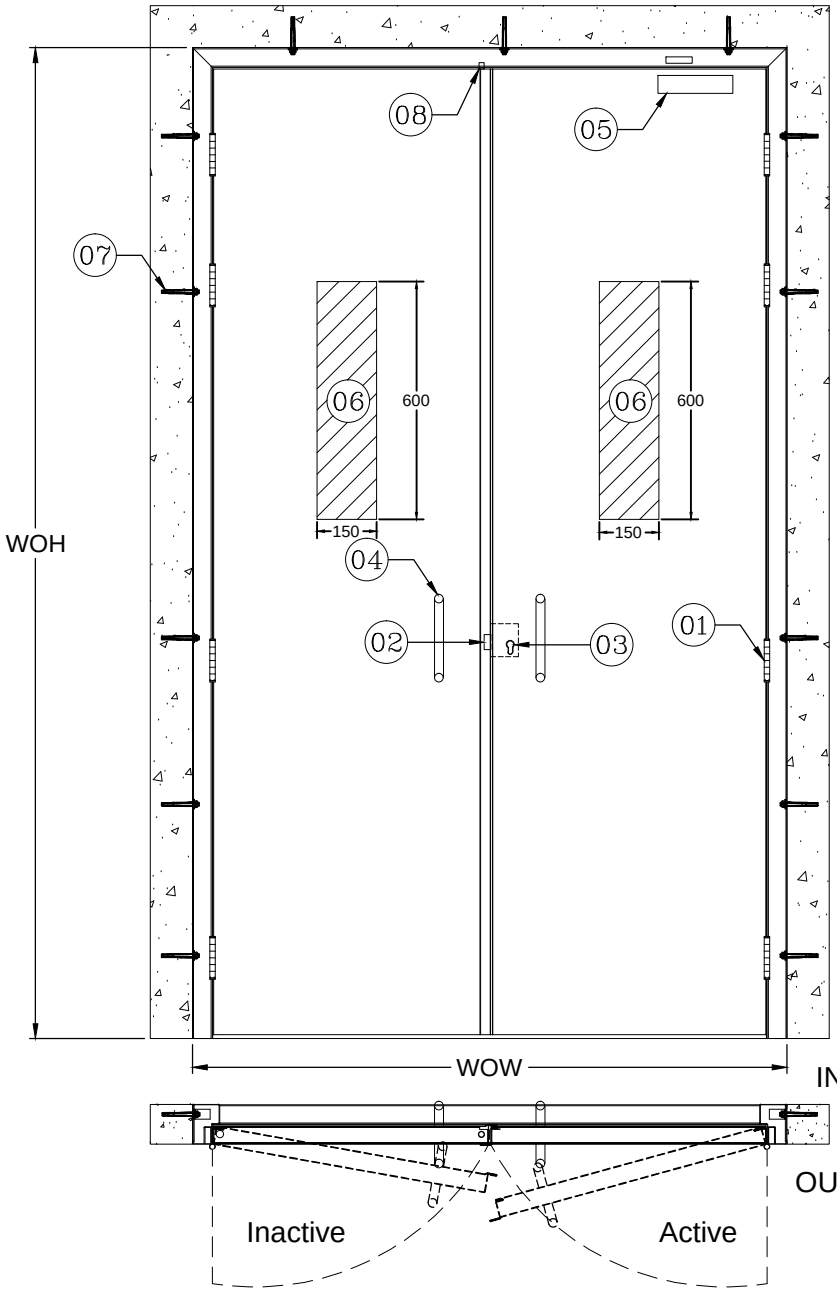


Abbrevation's:
WOW-Wall Opening Width
WOH-Wall Opening Height

Hardware List:-

SR.NO	DESCRIPTION	QTY.
01	HINGES	08 Nos.
02	DEAD LOCK	01 No.
03	CYLINDER WITH BOTH SIDE KEY	01 No.
04	BOTH SIDE`D'HANDLE	02 Nos.
05	DOOR CLOSER	01 No.
06	VISION PANEL 150X600	02 Nos.
07	ANCHOR FASTENERS	13 Nos.
08	CONCELED TOWER BOLT	01 No.

DOOR OPENING TYPE: TYPE 8 - RIGHT HAND REVERSE ACTIVE

(for opening type refer door handling sheet)

Door Sizes :-

SR.NO	WOW	WOH	QTY.
01	1490	2505	01 No.

COLOR : RAL 9016 TRAFFIC WHITE

NOTE:-
*All Dimensions are in mm.
*Tolerance:-All Linear Dimensions ±3mm,Others ±0.5mm.
*The Drawing Is For Location of Hardware only. Drawing Does Not Represent The Hardware For More Clarity, Please Go Through Hardware Broucher.

NIHVA TECHNOLOGIES PVT. LTD. PUNE
Email:- info@nihva.com
Website:- www.nihva.com

TITLE:
STEEL DOOR (DOUBLE LEAF)

CLIENT'S APPROVAL :

CLIENT - RUTCON CONSTRUCTION PROJECT PVT. LTD.
PROJECT - JISL SITE HUBBALLI
SITE LOCATION -
DWG. NO. : NIHVA/16-17/0044
SCALE: NTS | WT: | SHEET:1 OF 1
DRAWN BY: ANIL KHOT DATE: 25-07-2016
CHECK : ANIL DATE: 25-07-2016
If any queries contact : projects@nihva.com
NOTE: ALL DIMENSION ARE IN mm

THIS DRAWING & DESIGNING IS THE PROPERTY OF NIHVA TECHNOLOGIES. NOT BE SOLD OR COPY TO ANY OTHER CONCERN.