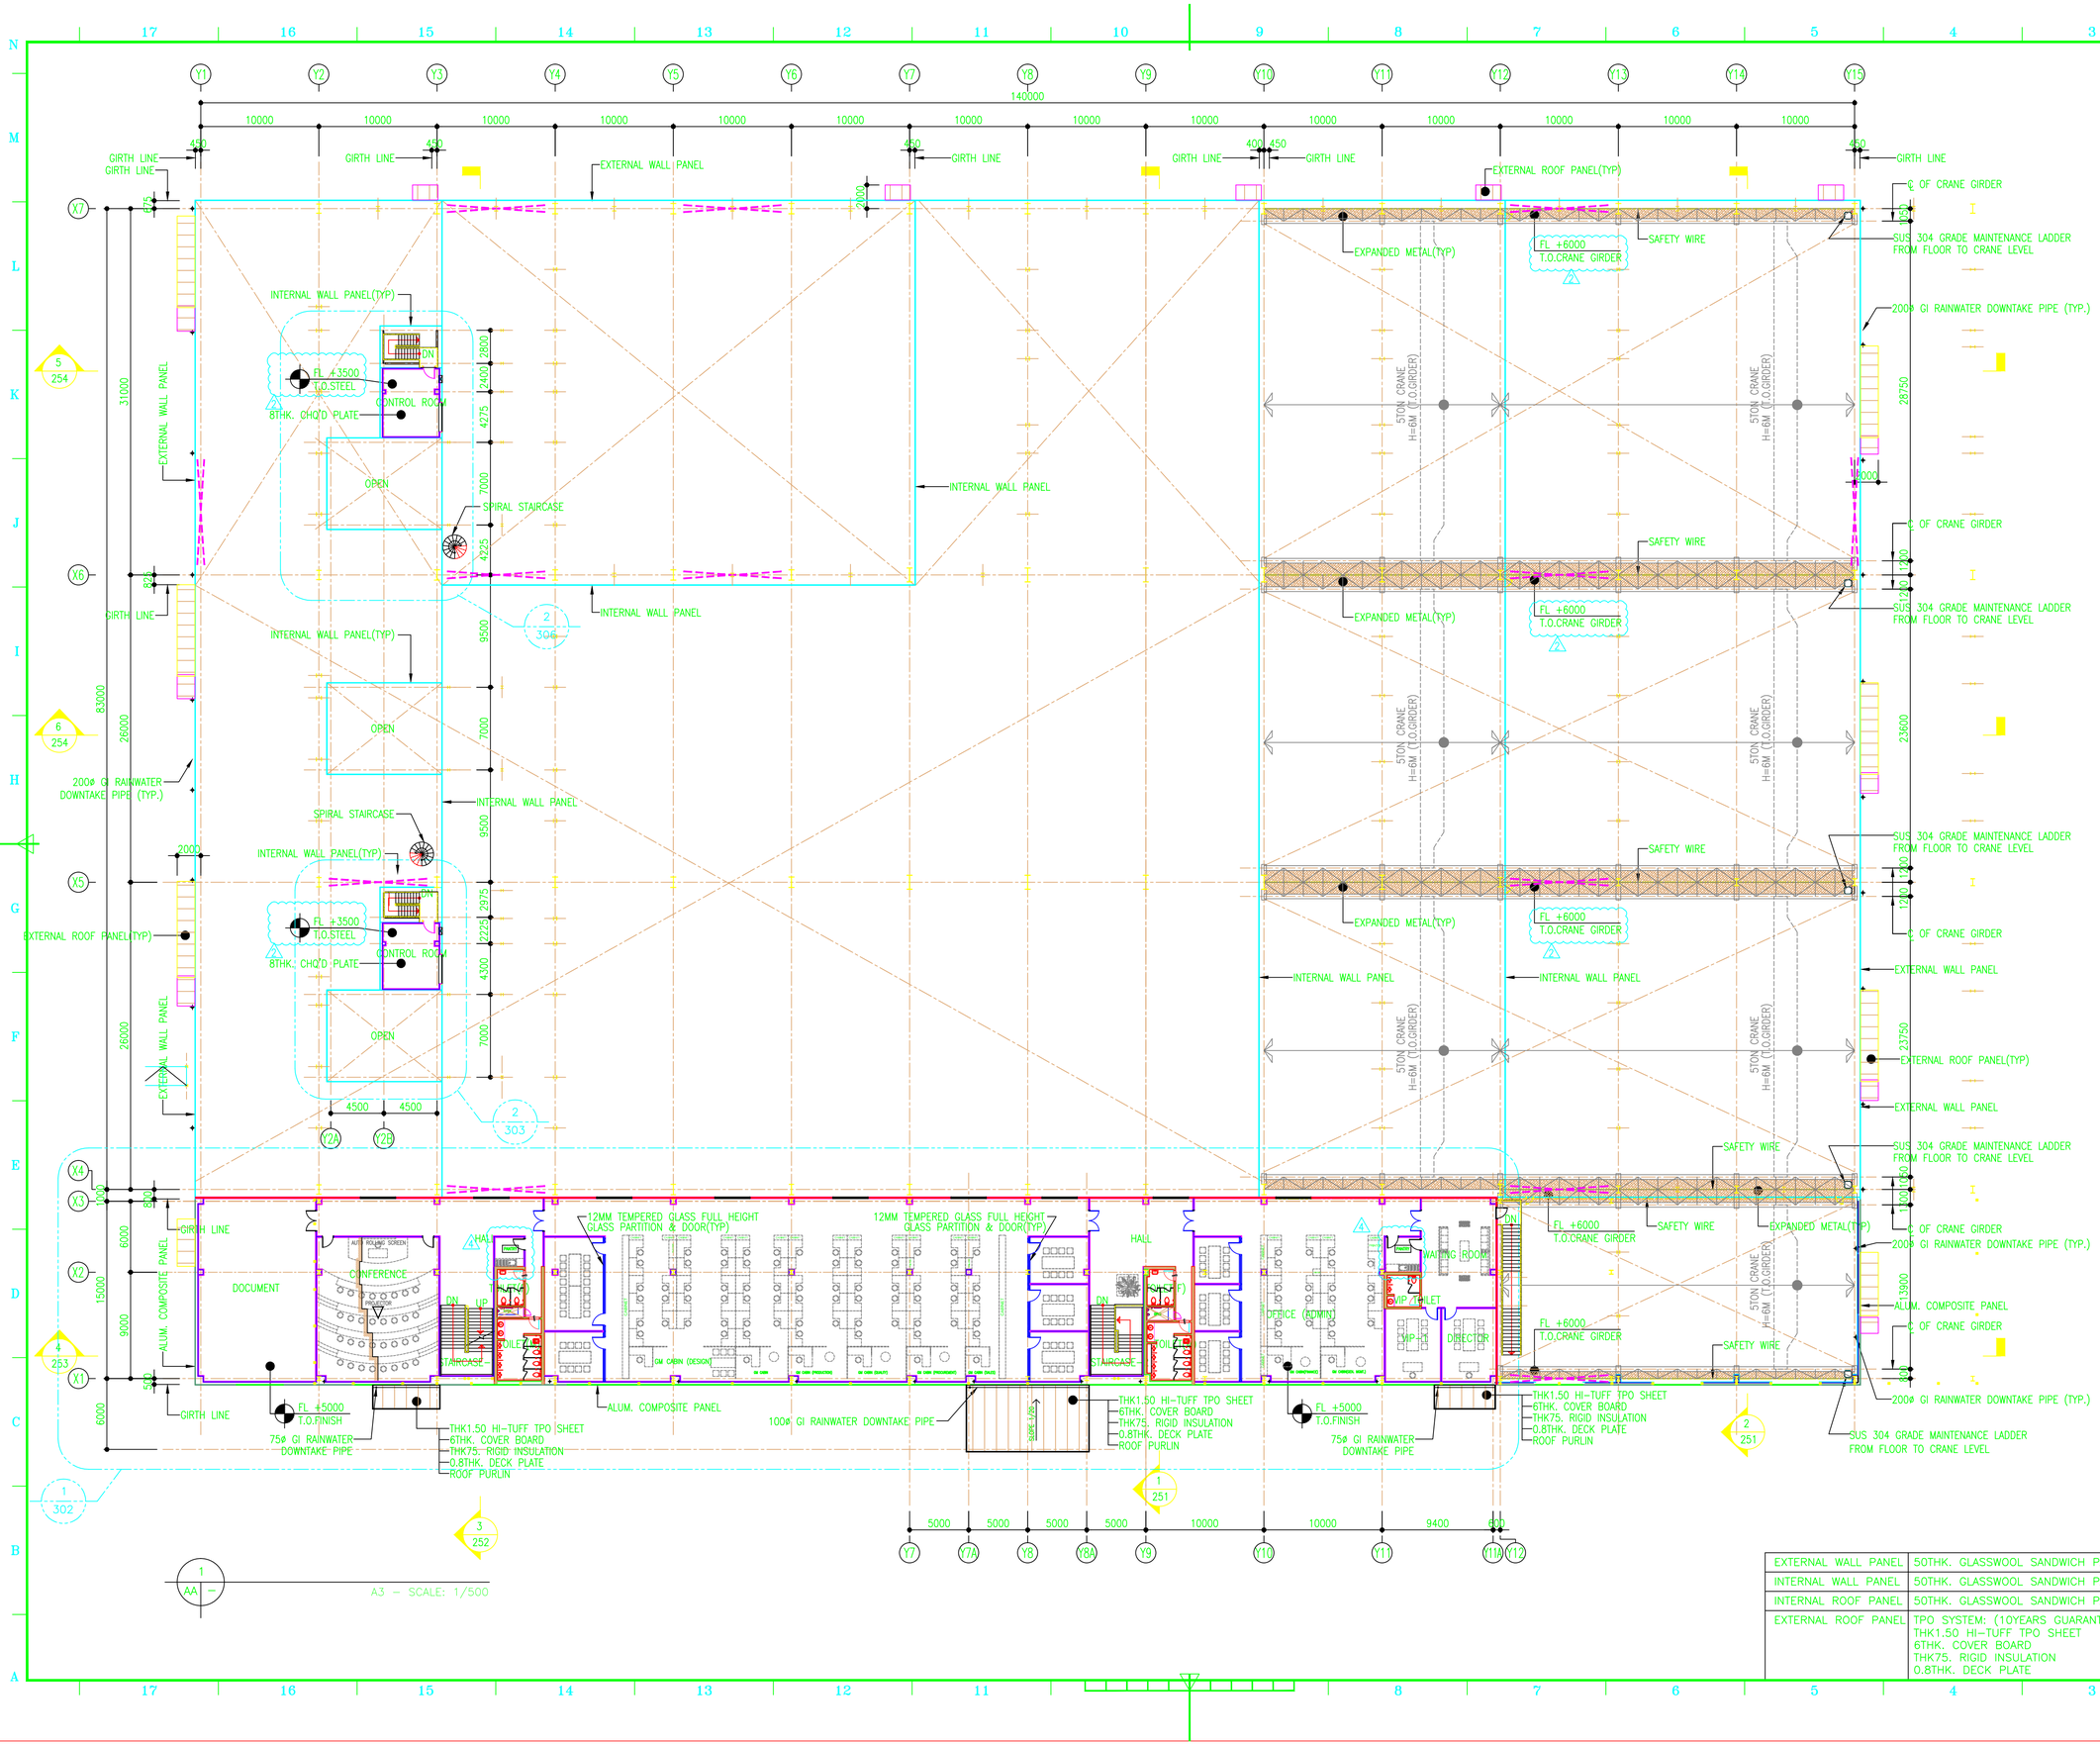


KEY PLAN

OFFICE LAYOUT REVISED AS PER CLIENT'S REQUIREMENT

REQUEST FOR REFERENCE ONLY

REV.	CONTENTS	NAME	DATE
4	OFFICE LAYOUT REVISED AS PER CLIENT'S REQUIREMENT	ANBU	08.DEC 2015
3	ISSUED FOR CONSTRUCTION	ANBU	16.OCT 2015
2	ISSUED FOR TENDER	ANBU	05.AUG 2015
1	FOR CLIENT CONFIRMATION AND ROUGH ESTIMATION DRAWING	ANBU	18.JUL 2015

CLIENT

HYOSUNG T&D

HYOSUNG CORPORATION INDIA PVT. LTD.

ARCHITECTS & ENGINEERS

HTI ENGINEERING PVT. LTD.

91.44.2252.3743 www.mapgroup.co.kr

PROJECT TITLE

HYOSUNG PUNE PLANT

DRAWING TITLE

1st FLOOR PLAN

EXTERNAL WALL PANEL	50THK. GLASSWOOL SANDWICH PANEL
INTERNAL WALL PANEL	50THK. GLASSWOOL SANDWICH PANEL
INTERNAL ROOF PANEL	50THK. GLASSWOOL SANDWICH PANEL
EXTERNAL ROOF PANEL	TPO SYSTEM: (10YEARS GUARANTEE) THK1.50 HI-TUFF TPO SHEET 6THK. COVER BOARD THK75. RIGID INSULATION 0.8THK. DECK PLATE

SCALE A3:1/500 A1:1/250	DRAWN BY	DESIGNED BY	CHECKED BY	APPROVED BY
DATE	ANBU	H.G.KIM	–	–
	20.MAY.2015	20.MAY.2015	–	–

DRAWING NO. HY-PU-FAC-AA-102 REV. 3