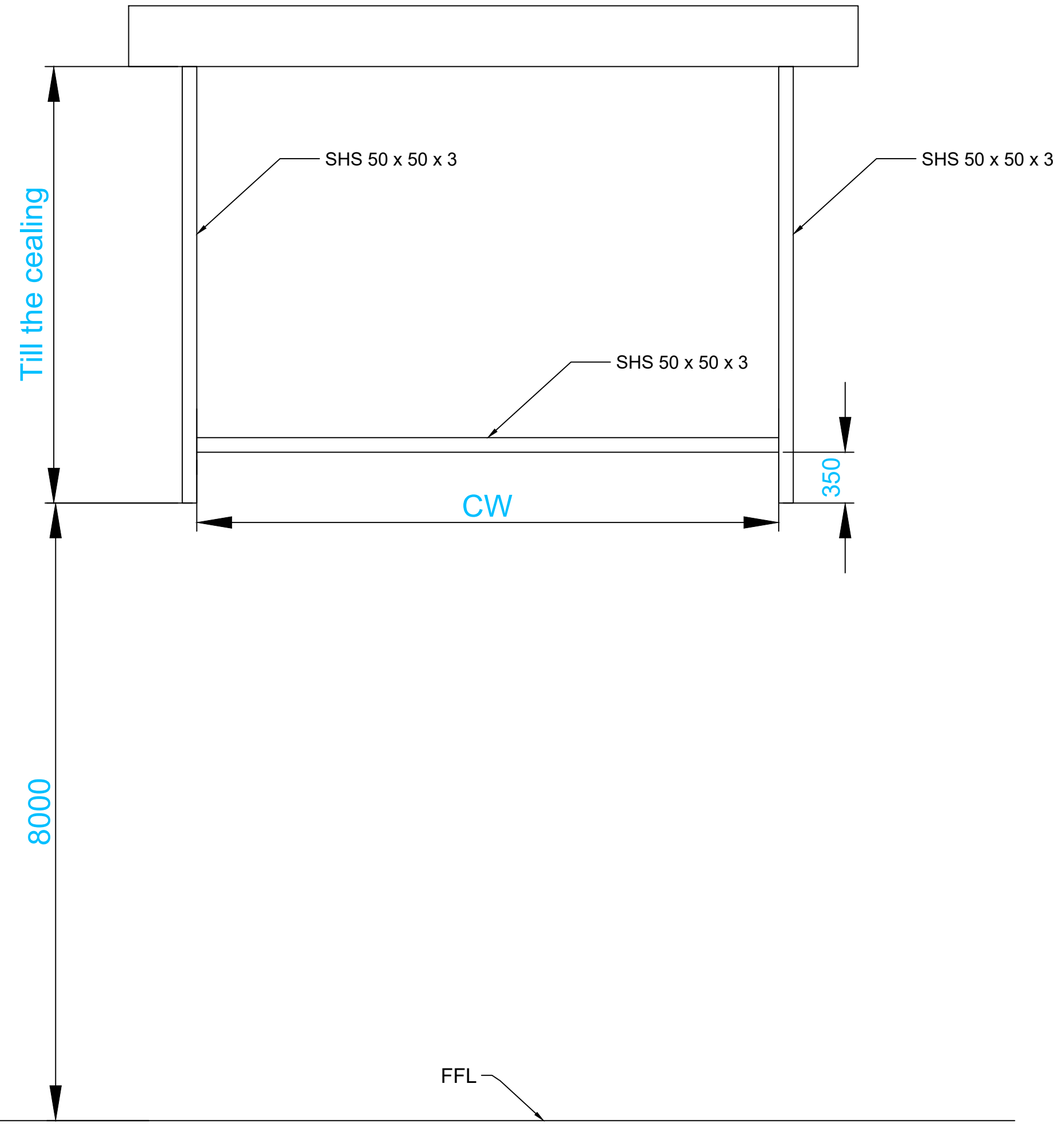


2.	MODIFIED HORIZONTAL POSITION TO PARTIAL VERTICAL & HORIZONTAL	MAHESH S.	28/11/2022
1.	Mentioned title name RS06	Sujata	28/12/2021
Rev.no	Revision	Revised BY	Date

NOTES-
(1) REQUIRED M.S. STRUCTURE , FITTING & ALL CIVIL WORK IN CLIENT SCOPE .
(2) PRODUCT WILL BE INSTALLED AFTER READINESS OF STRUCTURE AS PER DRAWING.

SR NO	CLEAR WIDTH CW	CLEAR HEIGHT CH		QTY
1	4800 mm	4500mm		1 nos

This drawing & design is the property of NIHVA TECHNOLOGIES. Not to be sold or copied to any other concern.

TITLE
STRUCTURE - Top Support
RS06 North Side

NIHVA TECHNOLOGIES PVT. LTD. PUNE
Tel : 020 66304033
Email:- info@nihva.com
Website:- www.nihva.com

	NAME	SIGN	DATE
DRAWN	G.P.		23.12.2021
CHECK	A.K.		23.12.2021
REV.			
APPROVAL			

CLIENT -AJAY KALE AND ASSOSIATES
PROJECT -
SITE LOCATION -
DWG. NO. : NIHVA/21-22/CLT/284
If any queries contact : design@nihva.com
SCALE: NTS | WT: | SHEET: 03 OF 03
ALL DIMENSION ARE IN mm