




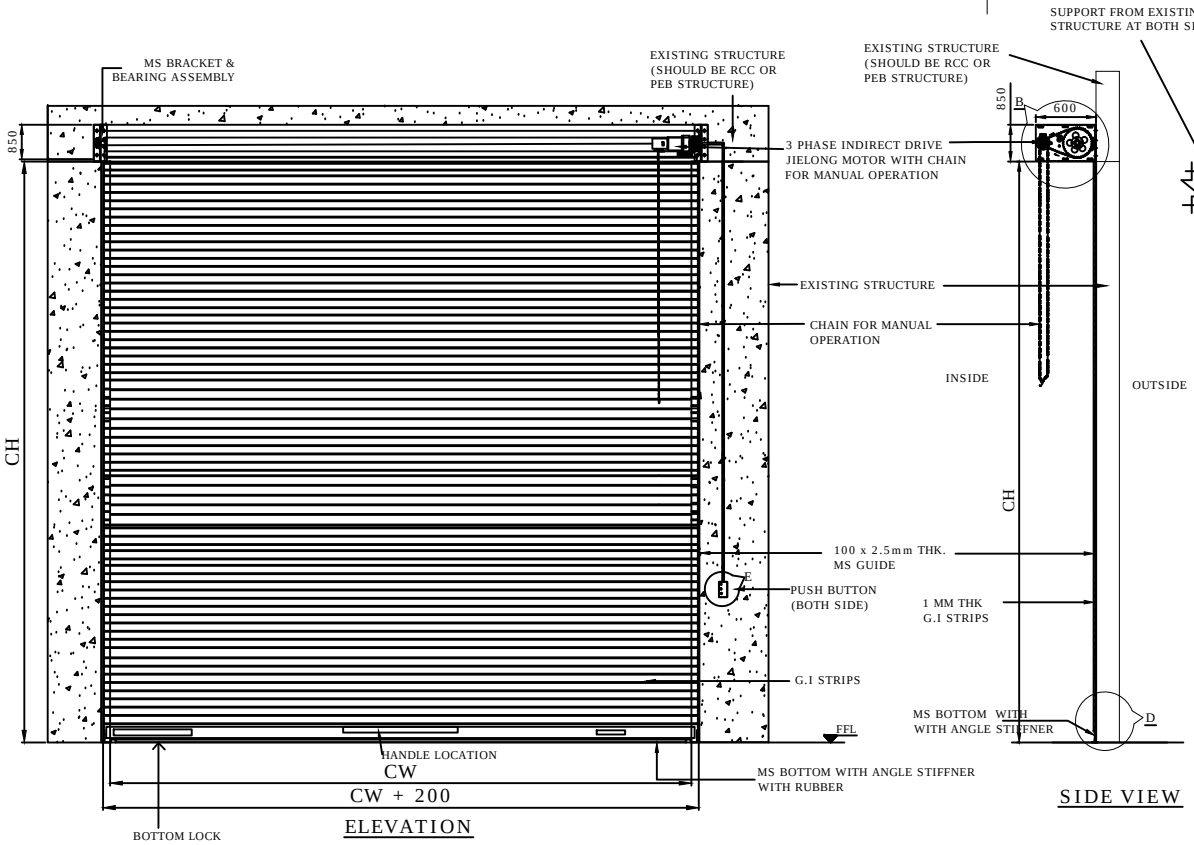


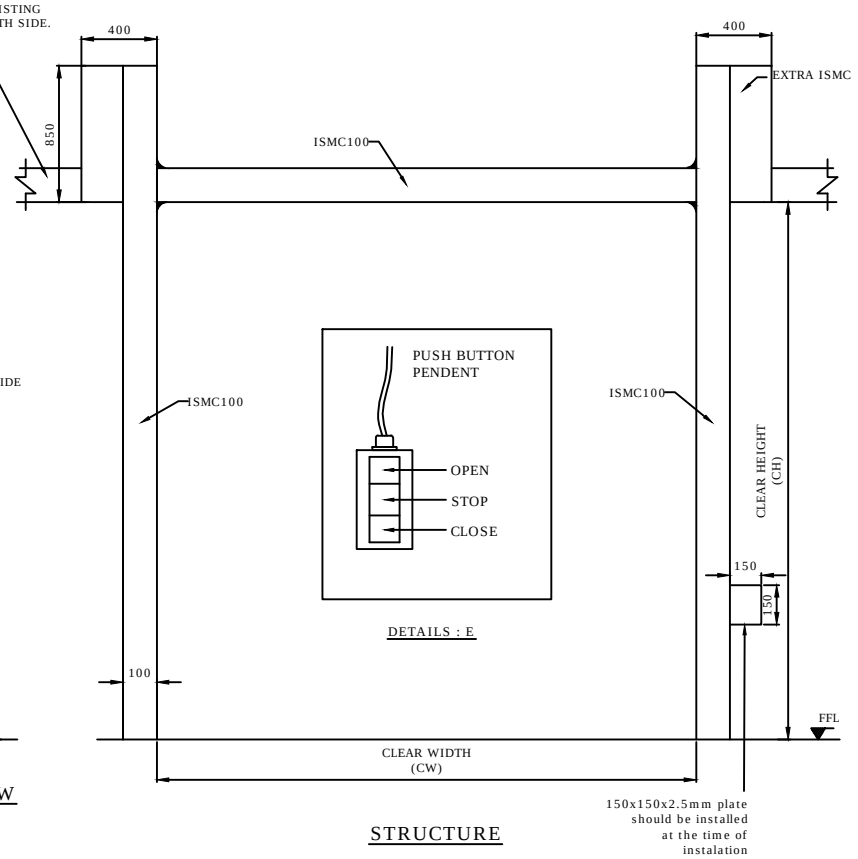


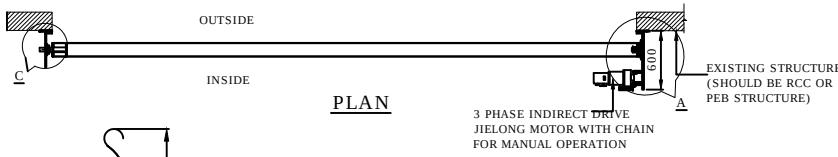

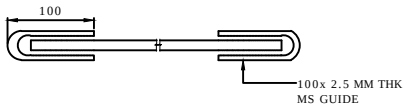

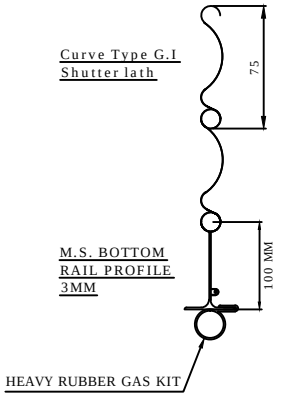

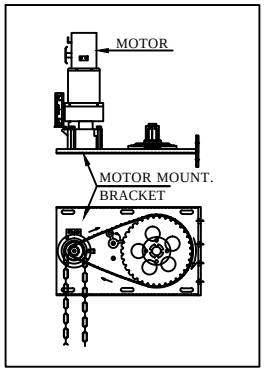

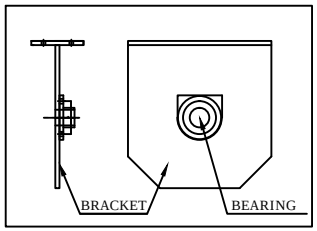

(NOTE: REQUIRED TECHANICAL STRUCTURE FOR SHUTTER IN CLIENT SCOPE)

4000	5000	8	RAL - 3001	
CLEAR WIDTH (CW)	CLEAR HEIGHT (CH)	QUANTITY	RAL COLOR	LOCATION

This drawing & design is the property of NIHVA TECHNOLOGIES. Not to be sold or copied to any other concern.

TITLE: MOTORIZED ROLLING SHUTTER

	NAME	SIGN	DATE
DRAWN	P.A		25.02.2020
CHECK	G.J		25.02.2020
APPRD.			

NIHVA TECHNOLOGIES PVT. LTD.
NIHVA TECHNOLOGIES PVT. LTD. PUNE
Tel : 020 66304033
Email:- info@nihva.com
Website:- www.nihva.com

CLIENT - M/S.RELIABLE CONSTROTECH ENT.

PROJECT -M/S.TATA CUMMINS PRIVATE LTD

SITE LOCATION - PHALTAN

If any queries contact : design@nihva.com

DWG. NO. : NIHVA/19-20/0217 REV- R00

ALL DIMENSION ARE IN mm

SCALE: NTS WT: SHEET: