

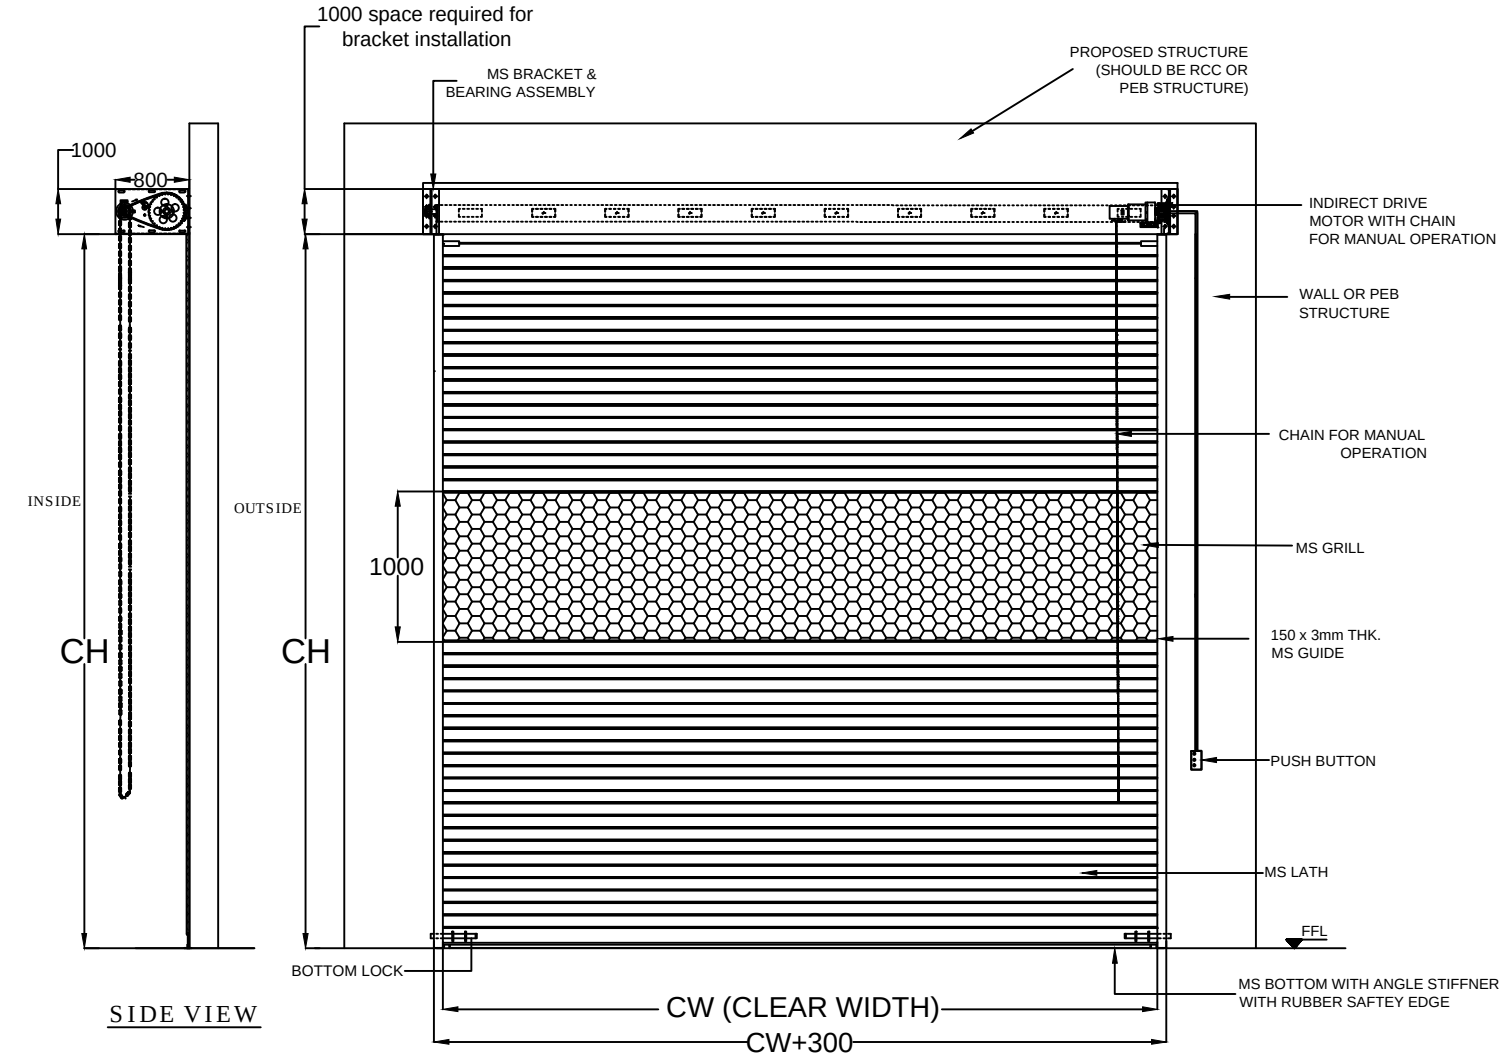


SIDE VIEW


ELEVATION

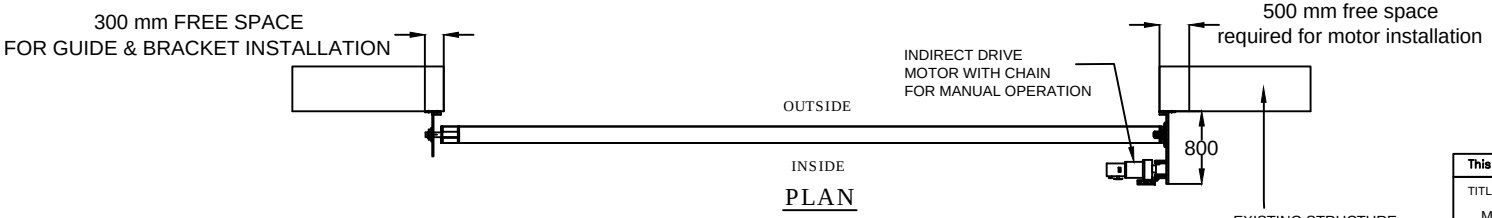

PLAN

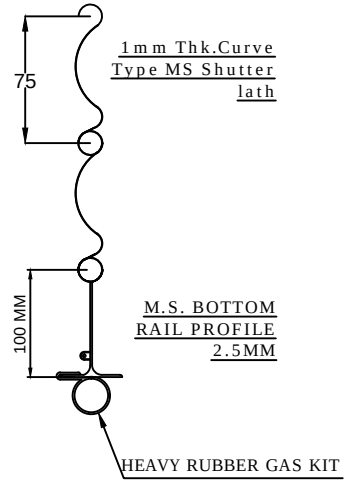

M.S. BOTTOM RAIL PROFILE 2.5MM

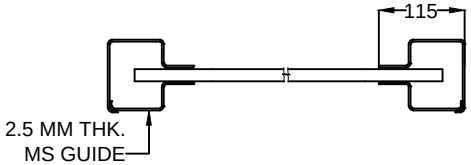

COLOR:- 1.RAL7035(LIGHT GRAY)
2.RAL9016(TRAFFIC WHITE)
3.RAL5005(SIGNAL BLUE)
4.RAL7004(SIGNAL GRAY)

CLEAR WIDTH (CW)	CLEAR HEIGHT (CH)	GRILL SIZE (CW) X (CH)	QUANTITY
7000	7000	7000 X 1000	04

NOTE:-
1. REQUIRED STRUCTURE FOR ROLLING SHUTTER SHALL BE IN CLIENT SCOPE.
2. ALL REQUIRED CIVIL WORK IN CLIENT SCOPE.
3. FOR FINAL FINISH CLIENT SHOULD CONFIRM RAL COLOR SHADE.
4. 3 PHASE POWER SUPPLY SHOULD BE PROVIDED BY CLIENT.

This drawing & designing is the property of NIHVA TECHNOLOGIES. Not to be sold or copied to any other concern.

TITLE: MOTORIZED ROLLING SHUTTER

NIHVA TECHNOLOGIES PVT. LTD. PUNE
Tel : 020 66304033
Email:- info@nihva.com
Website:- www.nihva.com

	NAME	SIGN	DATE
DRAWN	G.P.		11/09/21
CHECK	A.K.		11/09/21
APPROVAL	V.T.		11/09/21

CLIENT -
PROJECT -
SITE -

If any queries contact : design@nihva.com
DWG. NO. : NIHVA/21-22/VDR/0138
REV. - 0
ALL DIMENSION ARE IN mm
SCALE: NTS
WT:
SHEET: 01 OF 01