
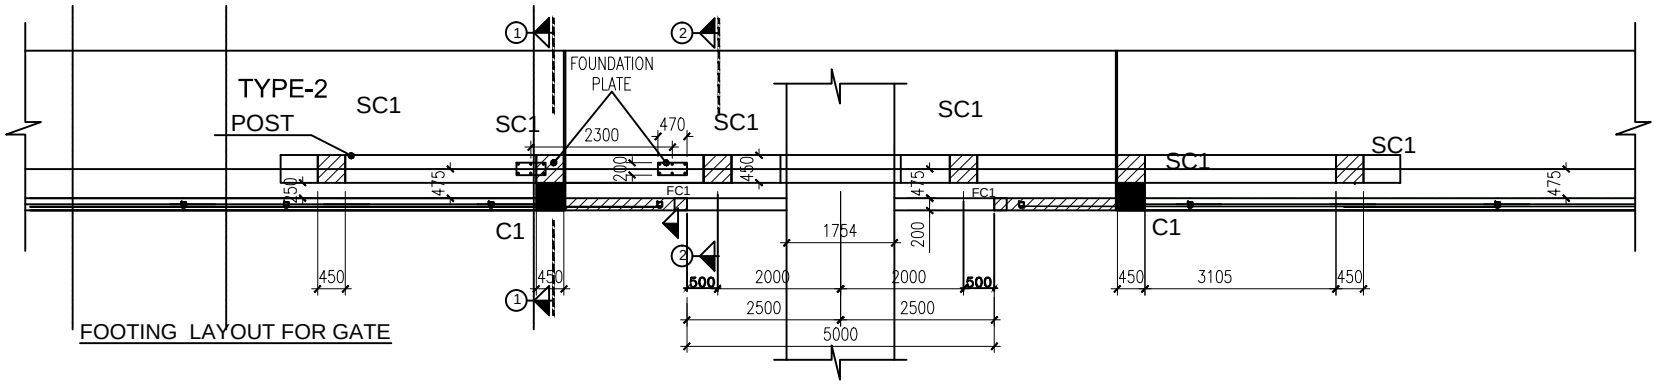



FOOTING LAYOUT FOR GATE

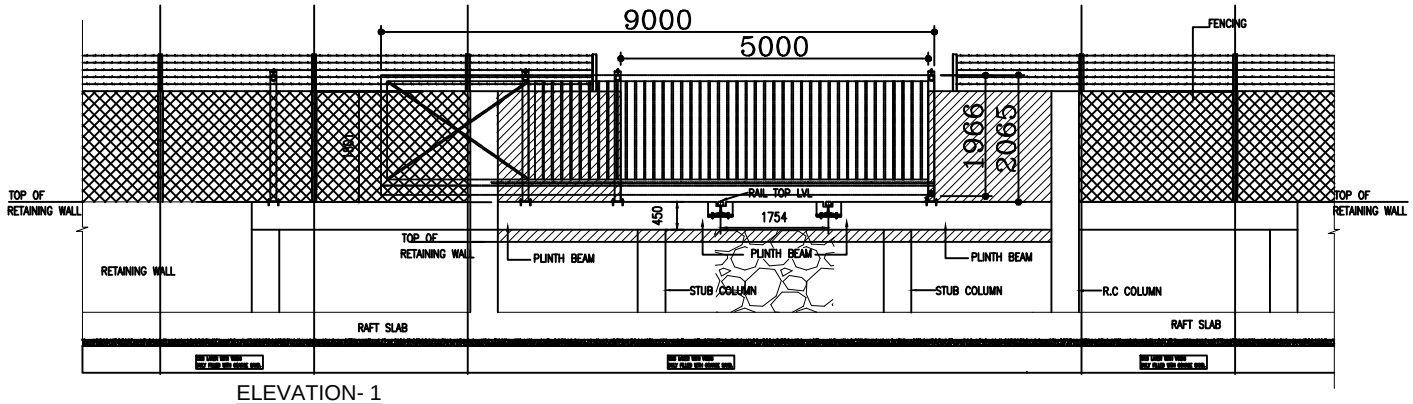


ELEVATION- 1

FOUNDATION DRAWING FOR WHEEL MOUNING PLATES

This drawing & designing is the property of NIHVA TECHNOLOGIES. Not to be sold or copied to any other concern.

| | | | | |
|---|---|---|---|---|
| TITLE: FOUNDATION DRAWING FOR CANTILEVER GATE | | | | NIHVA TECHNOLOGIES PVT. LTD. PUNE<br>Tel : 020 66304033<br>Website:- www.nihva.com<br>Email:- info@nihva.com |
| | Name | SIGN | DATE | |
| DRAWN | P.A | | 31.01.20 | CLIENT - DESAI CONSTRUCTION |
| CHECK | G.J | | 31.01.20 | PROJECT - |
| APPROVAL | | | | SITE LOCATION - GUJARAT |
| If any queries contact : design@nihva.com | | | | DWG. NO. : NIHVA/19-20/0202 REV.:- 0 |
| ALL DIMENSION ARE IN mm | | | | SCALE: NTS WT: SHEET: 01 OF 01 |