

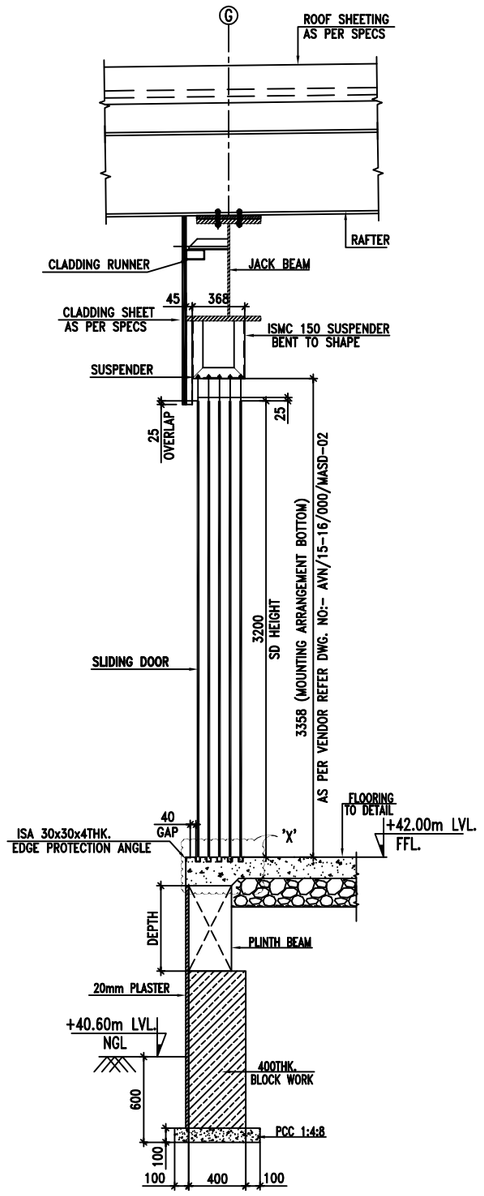



TYPICAL SLIDING DOOR CONNECTION DETAIL FOR 5 PANELS

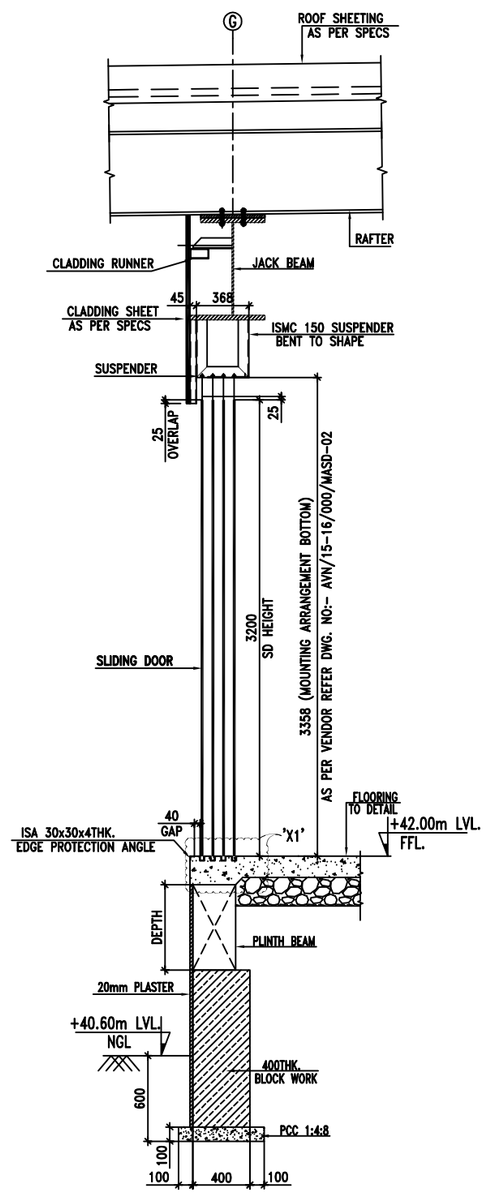


TYPICAL SLIDING DOOR CONNECTION DETAIL FOR 4 PANELS

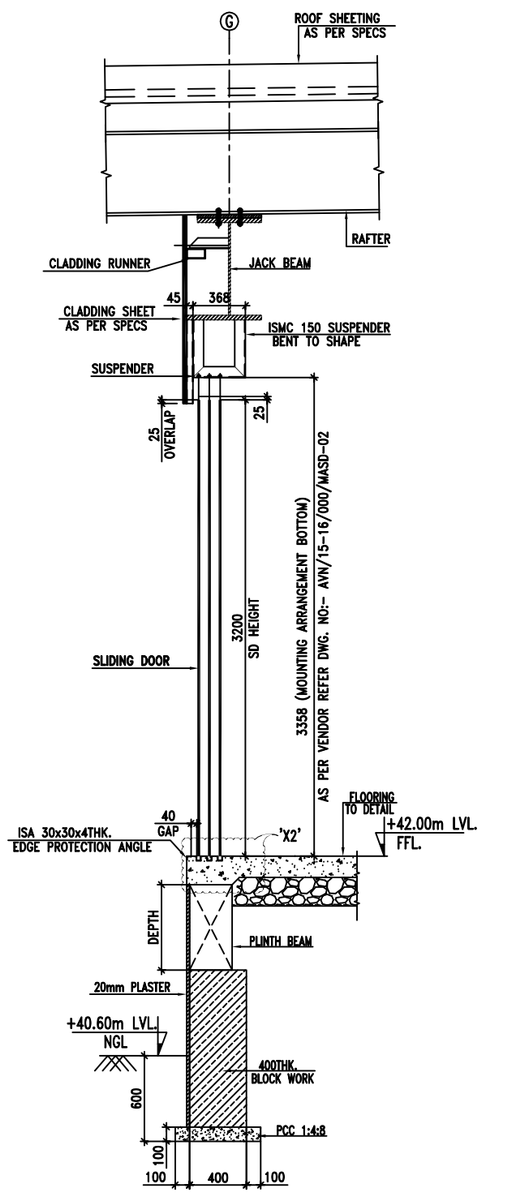


TYPICAL SLIDING DOOR CONNECTION DETAIL FOR 3 PANELS

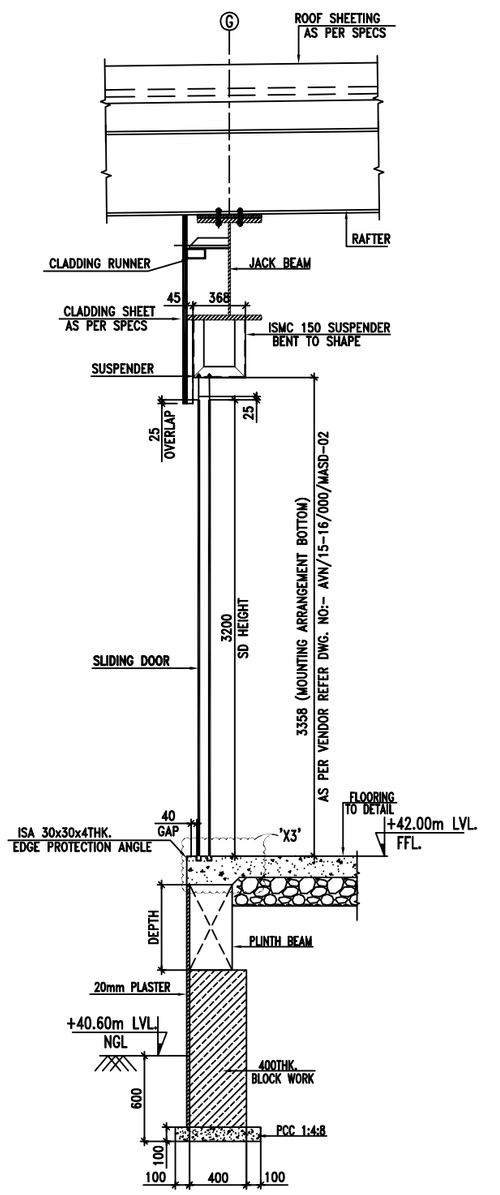


TYPICAL SLIDING DOOR CONNECTION DETAIL FOR 2 PANELS

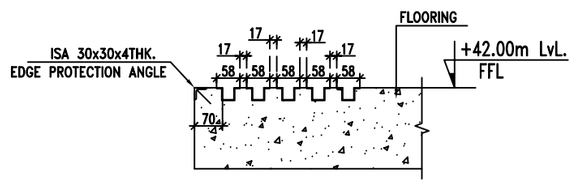


DETAIL–'X'

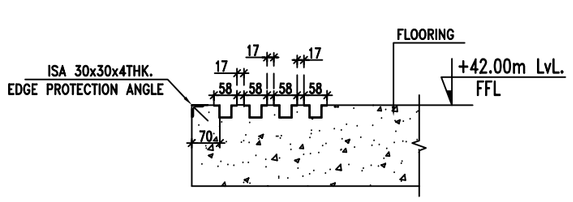

DETAIL–'X1'

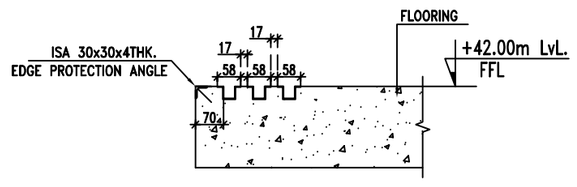

DETAIL–'X2'

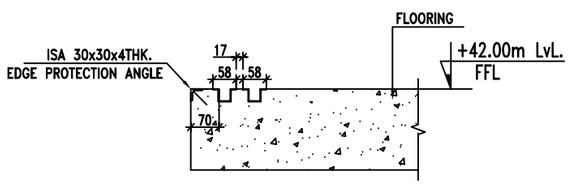

DETAIL–'X3'

IF IN DOUBT ASK

NOTES :–

REFERENCE DRAWINGS:–


1) FOR STANDARD R.C.C NOTES REFER. DRG.NO.:–
SUZ–STD–RC–200

2). REFER THIS DRAWING ALONG WITH DWG. NO:–
SC/SPCL/SMG/STR/RC/WS–203
SC/SPCL/SMG/STR/RC/WS–203A

FOR APPROVAL

14.03.17	RO	FOR APPROVAL	
DATE	NO	REVISIONS	BY
DATE	NO	ISSUED TO	BY
03.01.17	MAIL	SITE	

KEY PLAN

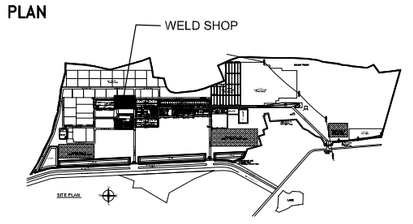

CLIENT

SUZUKI
SUZUKI MOTOR GUJARAT PVT. LTD.

DESIGN & BUILD CONTRACTOR

Shapoorji Pallonji ENGINEERING & CONSTRUCTION

WELD SHOP

DRAWING NO: SC/SPCL/SMG/STR/RC/WS–203B

TITLE : WELD SHOP
SLIDING DOOR CONNECTION DETAIL

SCALE :1:25,10	
DRAWN BY :	SAI
CHECKED BY :	MIRZA
APPROVED BY :	RAJESH RB
DESIGN ENGR. :	MIRZA
DATE :	14/03/2017
REV. NO.	R0

N W E S

LATEST ARCH. DRG.	SC/SCPL/SMG/ARCH/WS–01 TO 07
LAST MODIFIED	05/09/2016