SHUTTER SIZE:-
2471X3133-22NOS

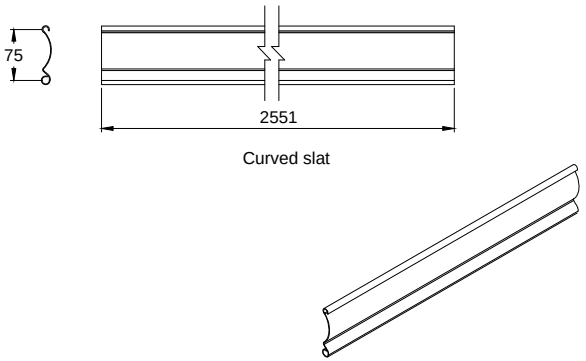

Curved slat

Slat profile- curved type.
Material- GI
Thickness - 1mm
Length of slats - 2551mm
Total no of slat - 1144 NOS

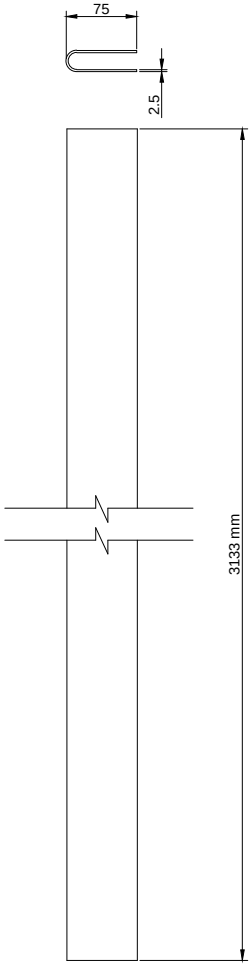

Material- MS
Thickness - 2.5mm
Length of guide - 3133mm
Quantity- 44 Nos.

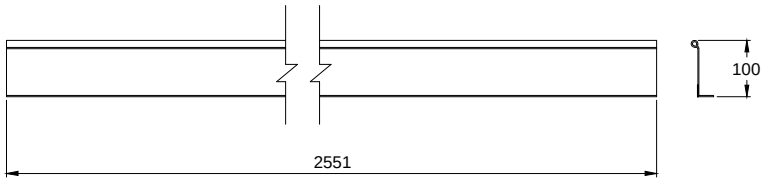

Material- MS
Thickness - 2.5mm
Length of bottom profile - 2551mm
Quantity- 22 Nos.

This drawing & designing is the property of NIHVA TECHNOLOGIES. Not be sold or copy to any other concern.

TITLE
GUIDE,BOTTOM & SLAT

NIHVA
NIHVA TECHNOLOGIES PVT. LTD.

NIHVA TECHNOLOGY
PVT. LTD. PUNE
Tel : 020 66304033
Email:- info@nihva.com
Website:- www.nihva.com

	NAME	SIGN	DATE
DRAWN	SURAJ		11.08.2018
CHECKED	P.A		11.08.2018
APPROVAL	R.D		11.08.2018

CLIENT -
PROJECT -
SITE -

If any queries contact : design@nihva.com
DWG. NO. : NIHVA/18-19/VDR/123
REV:- 0

ALL DIMENSION ARE IN mm
SCALE: NTS
WT:
SHEET: 01 OF 01