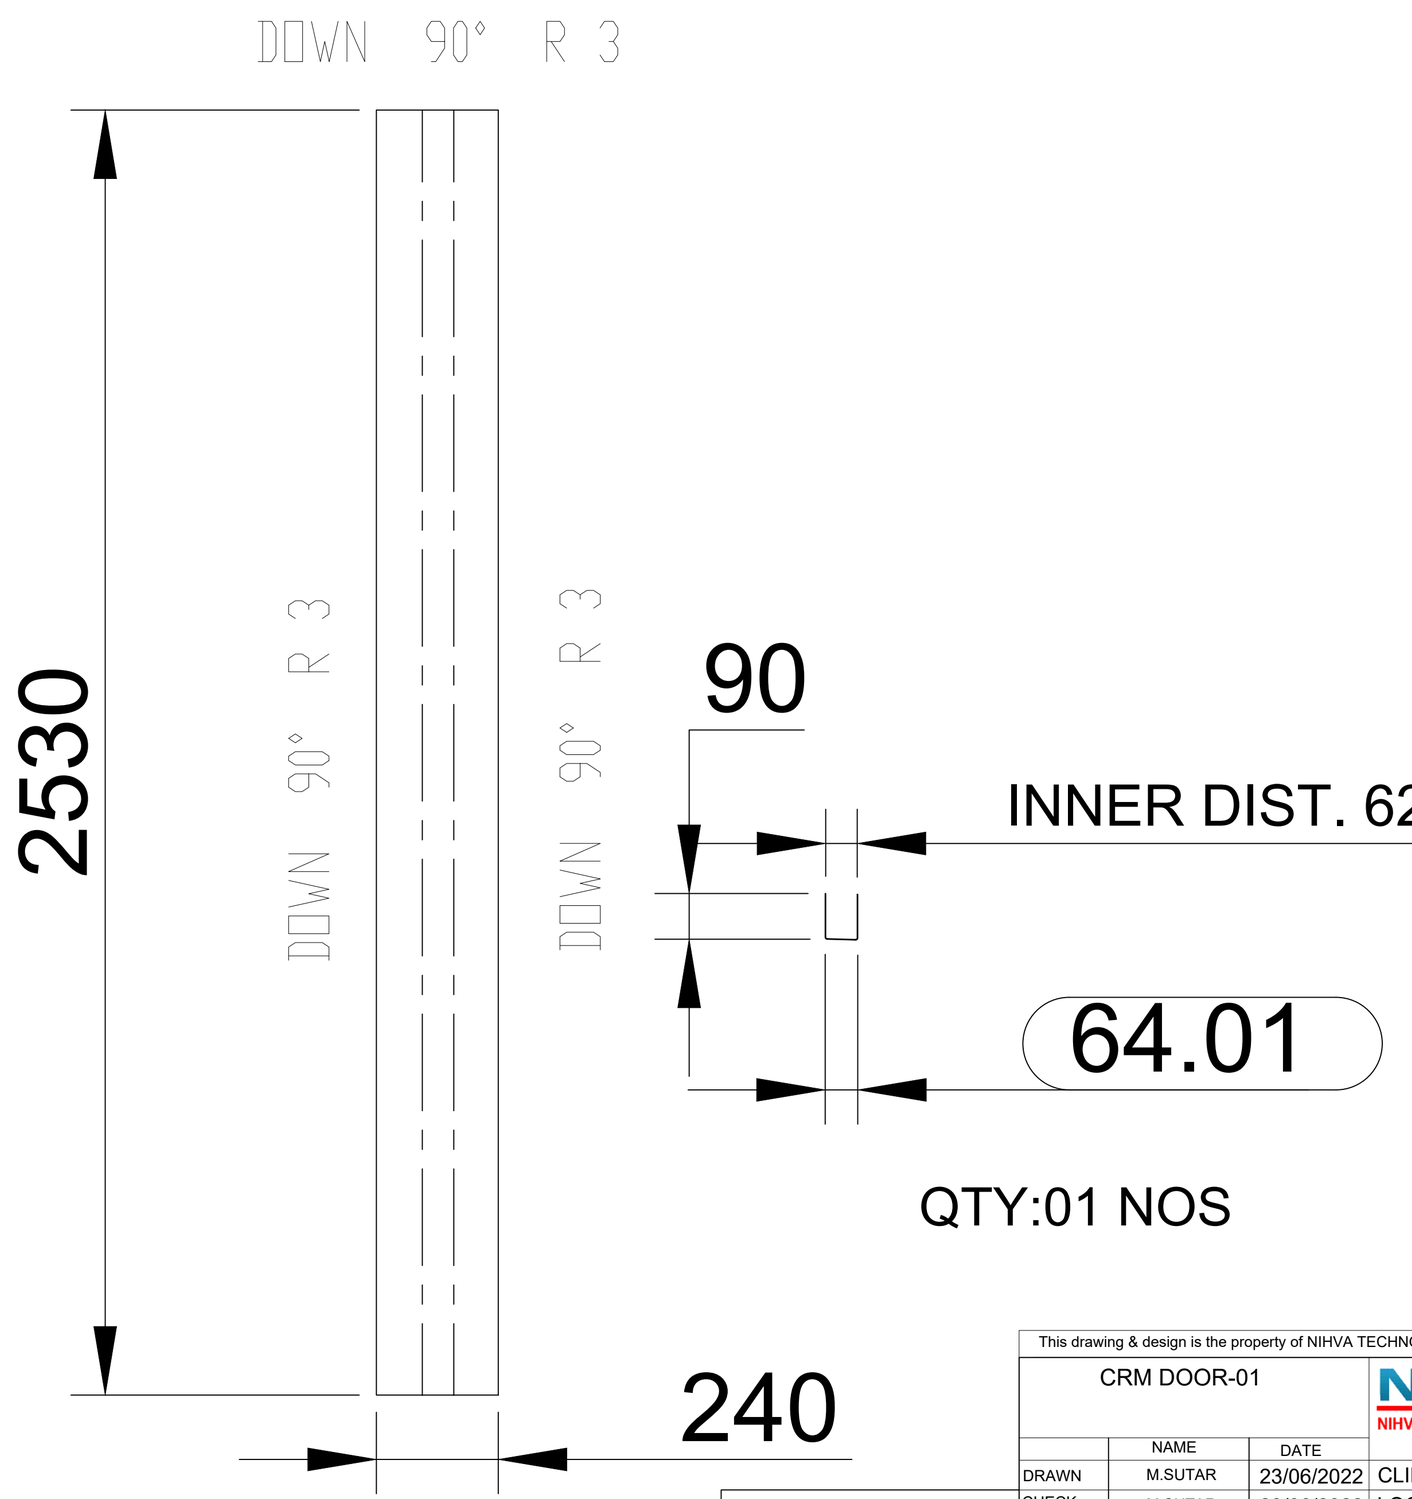


QTY:01 NOS

This drawing & design is the property of NIHVA TECHNOLOGIES. Not to be sold or copied to any other concern.

CRM DOOR-01			NIHVA TECHNOLOGIES PVT. LTD. PUNE Tel : 020 66304033 Email:- info@nihva.com Website:- www.nihva.com
	NAME	DATE	
DRAWN	M.SUTAR	23/06/2022	CLIENT - NIHVA TECHNOLOGIES PVT LTD
CHECK	M.SUTAR	23/06/2022	LOCATION -
APPRD.		23/06/2022	PRODUCT - SLIDING DOOR
If any queries contact : design@nihva.com			DWG NO:-NIHVA/22-23/VDR/0045
ALL DIMENSION ARE IN mm			SCALE: NTS SCALE:-- 1:1 SHEET:

Rev No.	Revision	Date	Revised By