
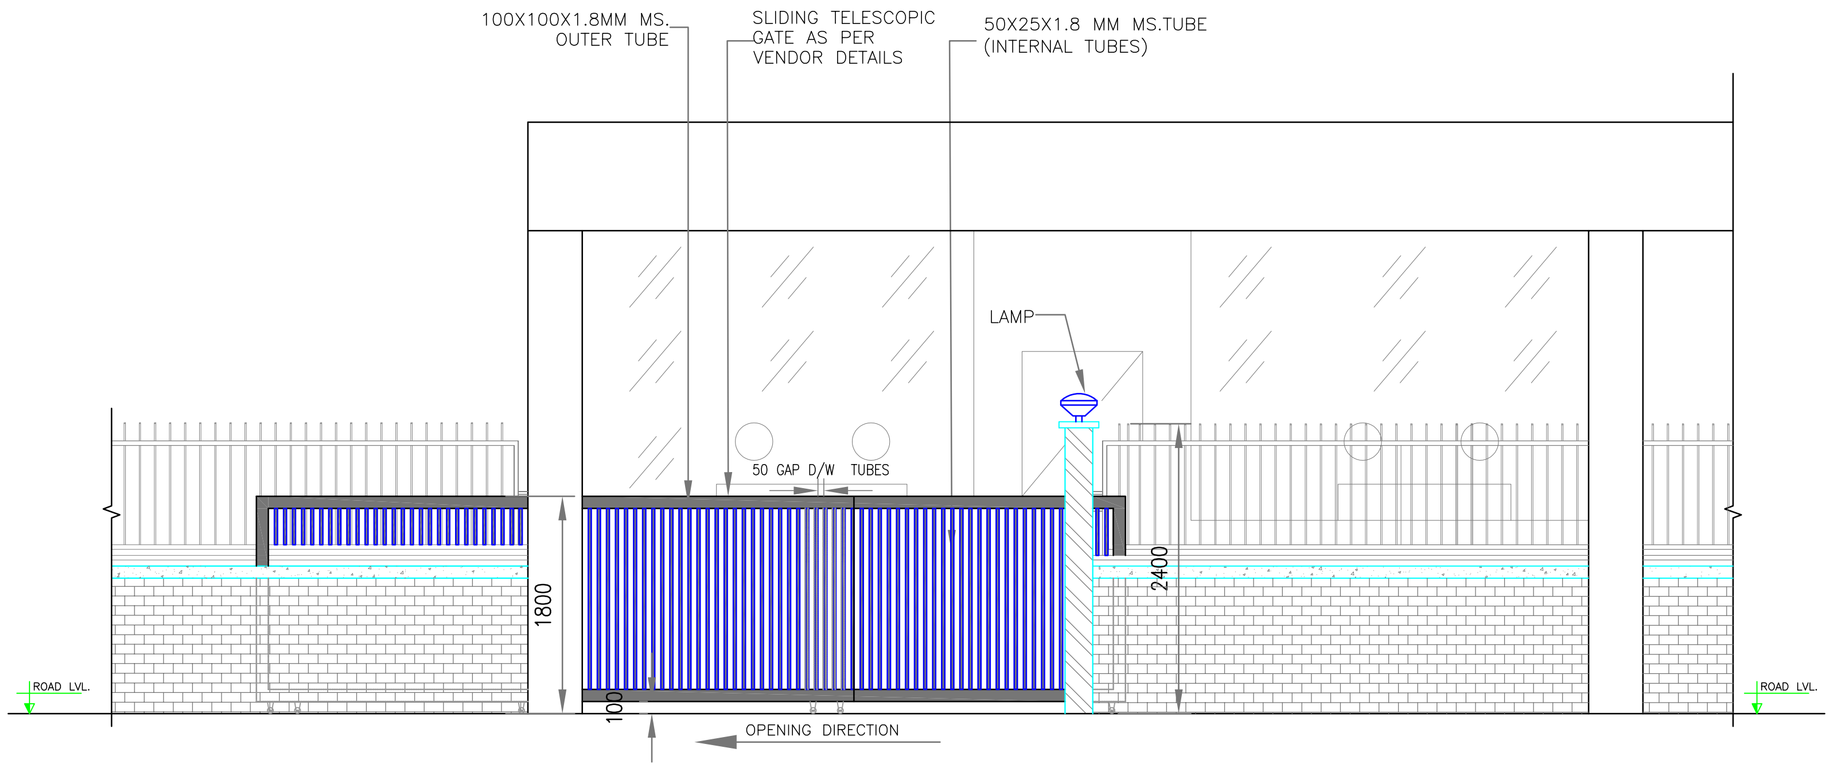


WEST ELEVATION OF CONTRACTOR & STAFF ENTRY GATE

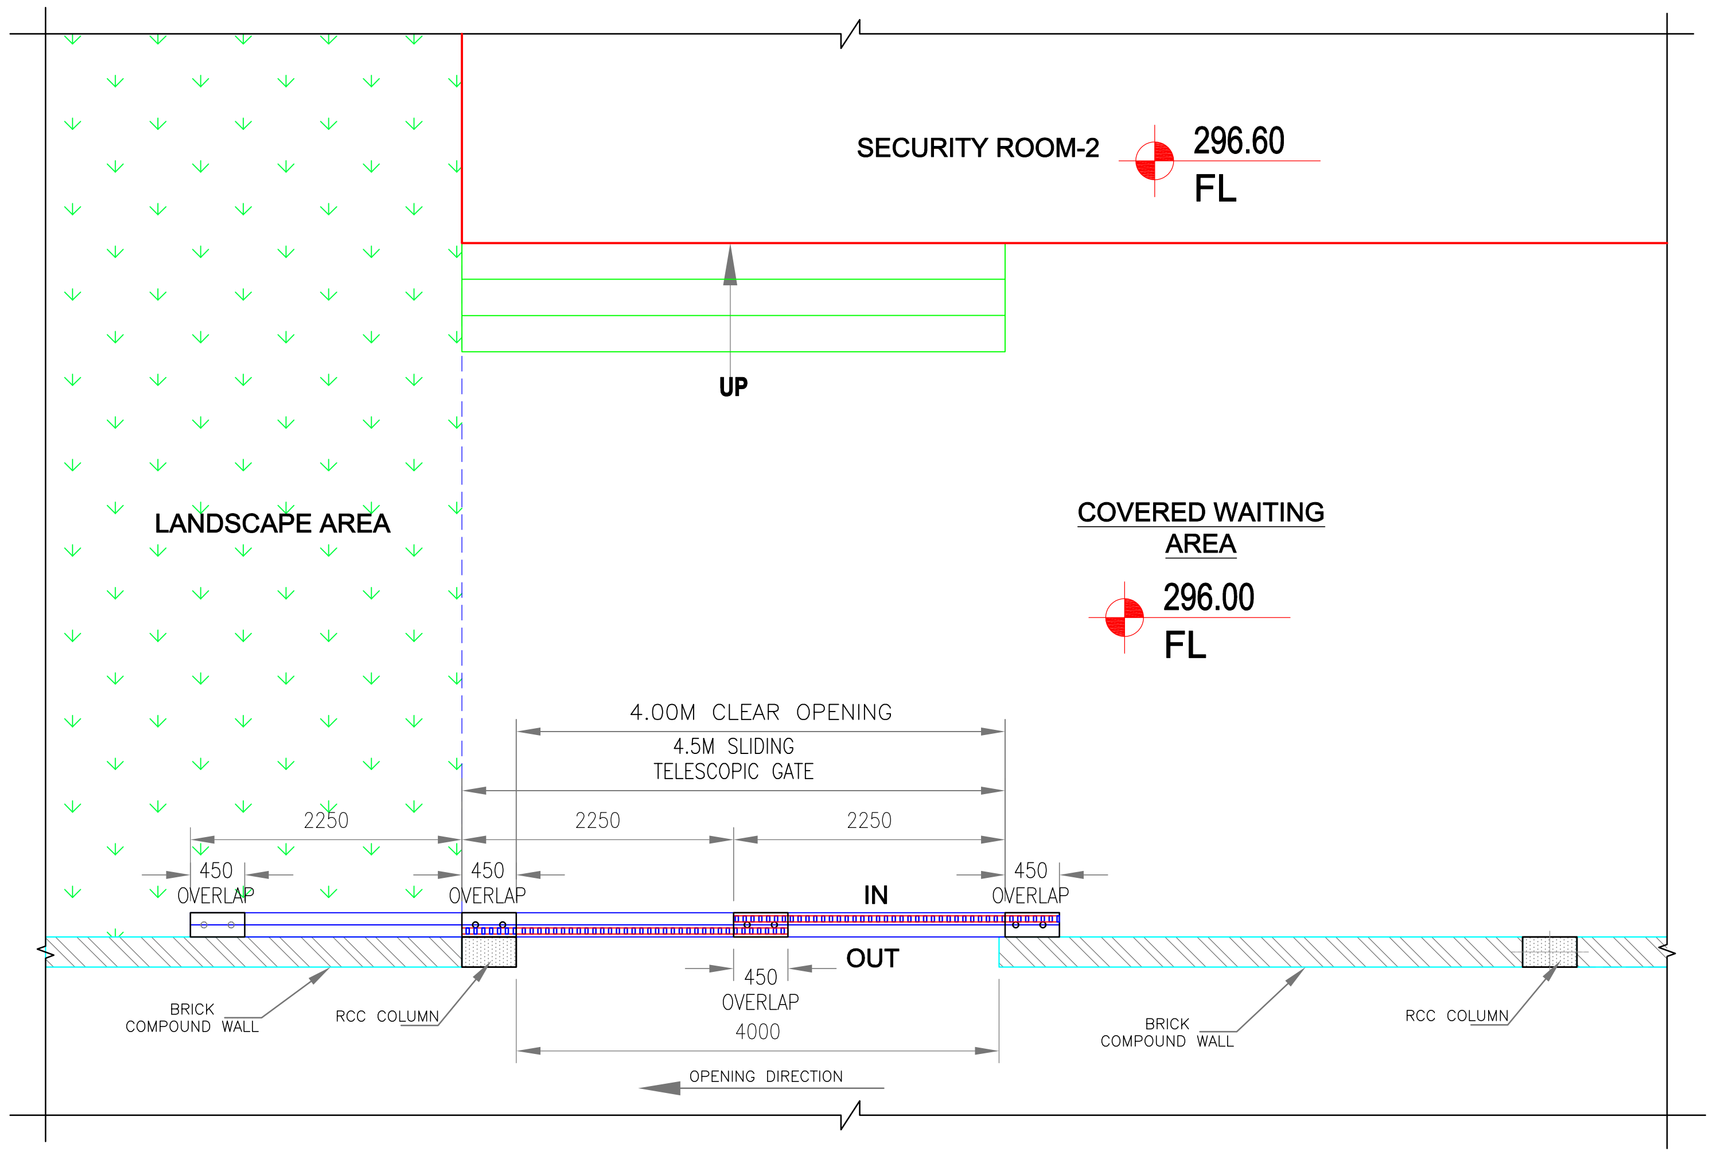

PLAN OF CONTRACTOR & STAFF ENTRY GATE

ips INTERNATIONAL

Integrated Project Services

Engineering
Design
Site Supervision
Consulting


C-1,C-Block, Community Centre, Naraina Vihar
New Delhi - 110 028

+91-11-25777806 phone
+91-11-25779089 phone
+91-11-25779152 phone
www.ipsintl.net

REVISION	DATE	DESCRIPTION	BY
R0	16AUG17	NEW DRAWING	SJ

FOR COMMENTS AND APPROVAL

KEY PLAN

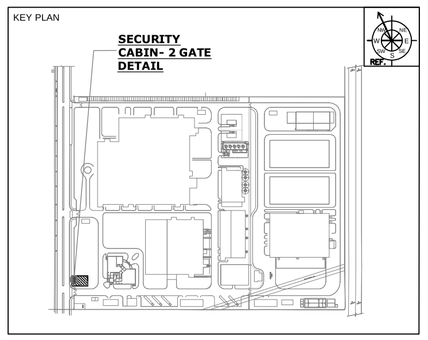

CONFIDENTIAL

THE INFORMATION CONTAINED HEREIN MAY NOT BE USED OR REPRODUCED IN ANY MANNER WITHOUT WRITTEN PERMISSION OF INTEGRATED PROJECT SERVICES.

CLIENT

LUPIN LIMITED
MIHAN NAGPUR

Lupin Ltd.

DRAWING TITLE

OSD BLOCK
SECURITY CABIN 2
CONTRACTOR STAFF ENTRY
GATE DETAIL

ENGINEER	ARCHITECT	DESIGNER
DRAWN BY: SJ	REVIEWED BY:	SCALE: 1:50

RECORDS CONTROL

IPS #	DRAWING NUMBER
14-1095/96	IPS-14-1095/96-AR-A12
XREF FILE(S)	
CADD FILE #	PAPER SIZE: A2 / REV.

8/16/2017 5:24:39 PM

PDF created with pdfFactory Pro trial version www.pdffactory.com