

Weitergabe sowie Vervielfältigung dieses Dokuments, Verwertung und Mitteilung seines Inhalts sind nur nach vorheriger ausdrücklicher schriftlicher Zustimmung von SMS Meer GmbH gestattet. Das Dokument ist vor unberechtigtem Zugriff Dritter zu schützen. Zuwiderhandlungen verpflichten zu Schadenersatz. Alle Rechte aus Patent-/Gebrauchsmuster-/Markenschutz vorbehalten.

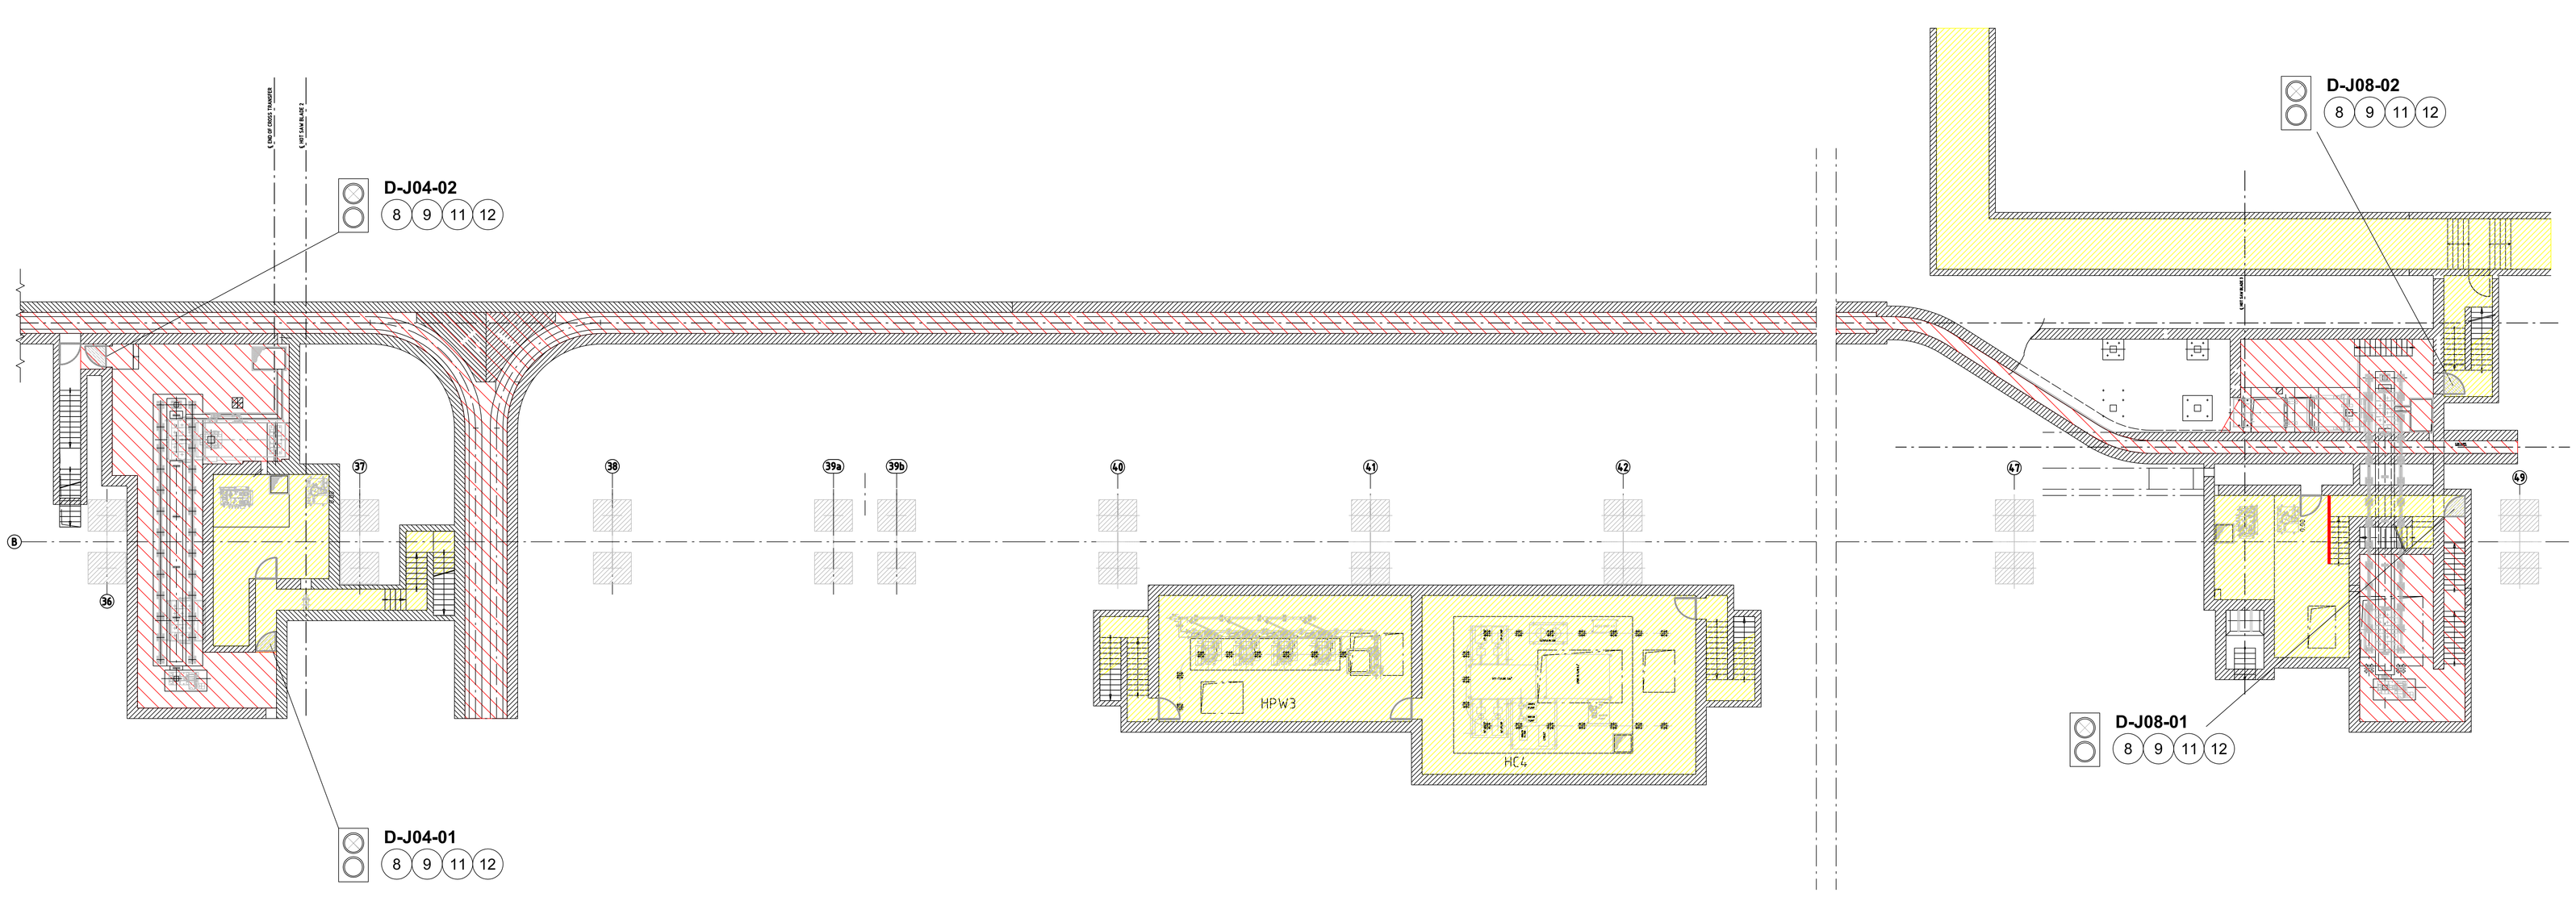

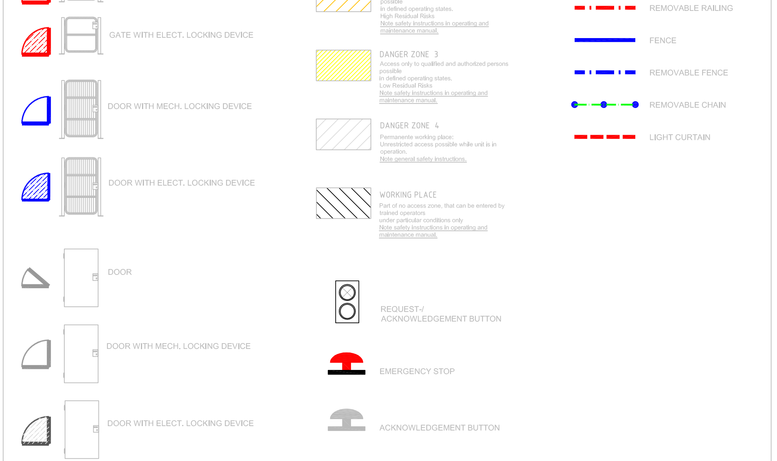

9463 0000 / RAILBHL

CATEGORY OF DRWG.	APPROVAL	INFORMATION	REFERENCE	RECORD	CONSTRUCTION

BHILAI STEEL PLANT, BHILAI, CHATTISGARH
7,0 MTPA EXPANSION

मेकॉन लिमिटेड
MECON LIMITED

VENSDOR'S NAME: SMS Meer/SMS Meer India/ABB

PACKAGE DESCRIPTION: UNIVERSAL RAIL MILL (Pkg No-047)

TITLE OF DRAWING. PARTITION 6, SAFETY LAYOUT

KHAZ-
VENDOR'S DRG NO.-
PROJECT DRG. NO. BSP-SMS Meer-08-047-21-130-35-BE-06654 REV. –

Fertigungsvorschriften / Manufacturing Instructions: SN 200

Ursprung / Origin | Fertiggewicht / Finished weight: kg | Werkstoff / Material | Projekt-Nr. / Pattern-No. | Projektionsmethode 1 / First angle projection method ISO 128

	Datum / Date	Name
Gezeichnet / Drawn	27.09.11	Fryen
Geprüft / Checked	27.09.11	Prätzel
Norm / Standard		
Freig. / Approved		

Typ / Type: Safety Layout
Benennung / Title: Teilbereich. 6
PARTITION 6
Sach-Nr. / Drawing-No.: 0100133-00.654
Maßstab / Scale: 1:100
Blatt / Sheet: 1
Blattzahl / Sheets: 1

SMS MEER GmbH, SMS group

Änderung / Revision	Datum / Date	Name

Ersatz für / Supersedes:
Ersetzt durch / Superseded by:

Diese Zeichnung und alle darauf enthaltenen Informationen sind vertraulich. This drawing and all information on it is confidential.

The reproduction, distribution and utilization of this document as well as the disclosure of its content to others without prior explicit written consent of SMS Meer GmbH is prohibited. Holder has to protect this document against unauthorized withdrawal of third parties. Offenders will be held liable for the payment of damages. All rights reserved in case of patent/utility model/ornamental design protection.