



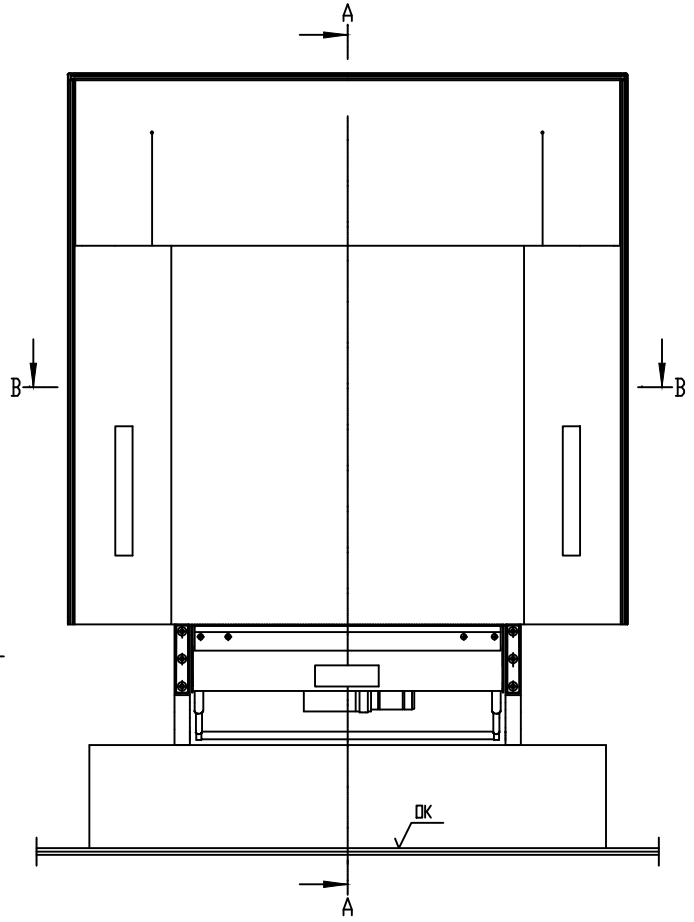


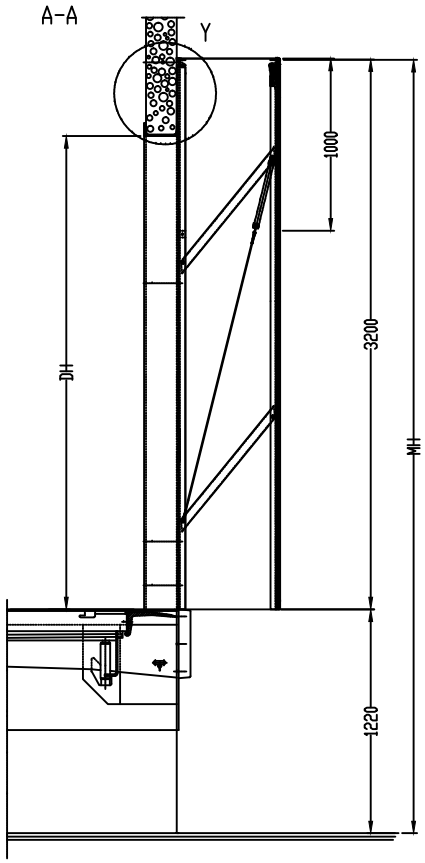

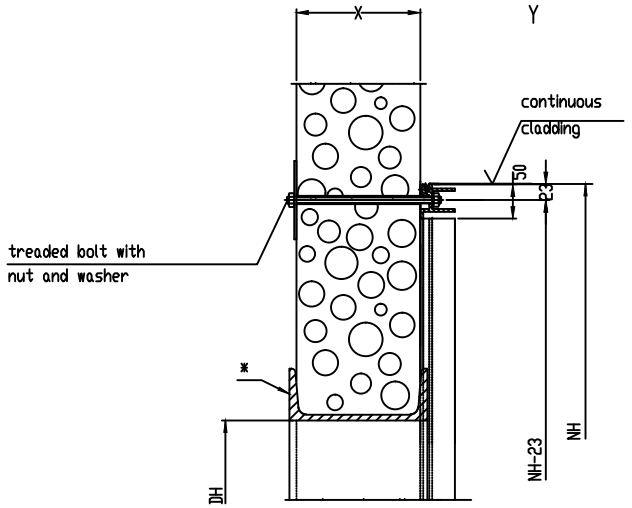

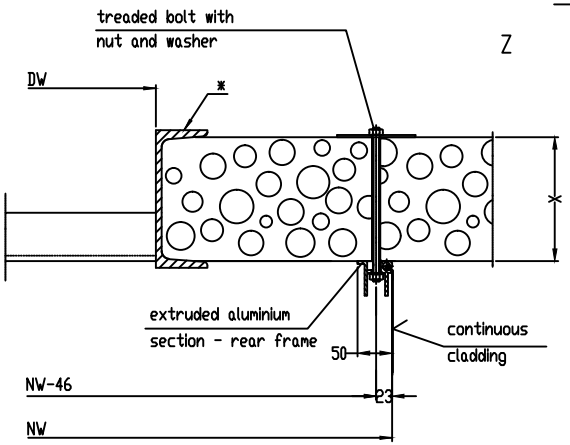

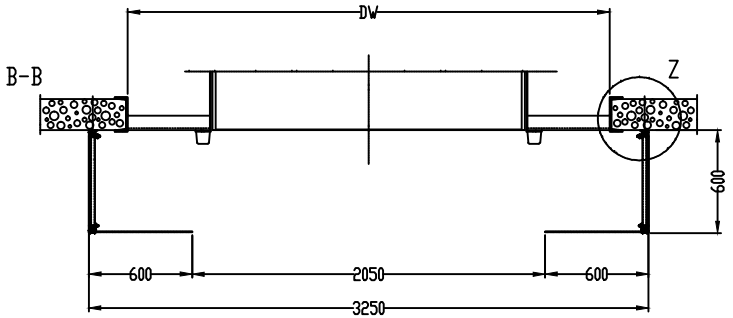

* By others, not included in the delivery.

NW-3250
NH-3200

TOLERANCE :- ± 10mm

This drawing & design is the property of NIHVA TECHNOLOGIES. Not to be sold or copied to any other concern.

TITLE
DOCK SHELTER

NIHVA
NIHVA TECHNOLOGIES PVT. LTD.

NIHVA TECHNOLOGIES PVT. LTD, PUNE
Tel : 020 66304033
Email:- info@nihva.com
Website:- www.nihva.com

	NAME	SIGN	DATE
DRAWN	P.V.A		26.06.2019
CHECK	V.M.T		26.06.2019
APPRD.			

CLIENT - WELSPUN INDIA PVT LTD
PROJECT -
SITE LOCATION - GUJRAT
If any queries contact : design@nihva.com
DWG. NO. : NIHVA/19-20/0043 REV- 00
ALL DIMENSION ARE IN mm
SCALE: NTS WT: SHEET: 01 OF 01