
ALBANY
ASSA ABLOY

Fixingplan
High speed roll door RapidProtect 300, RP300

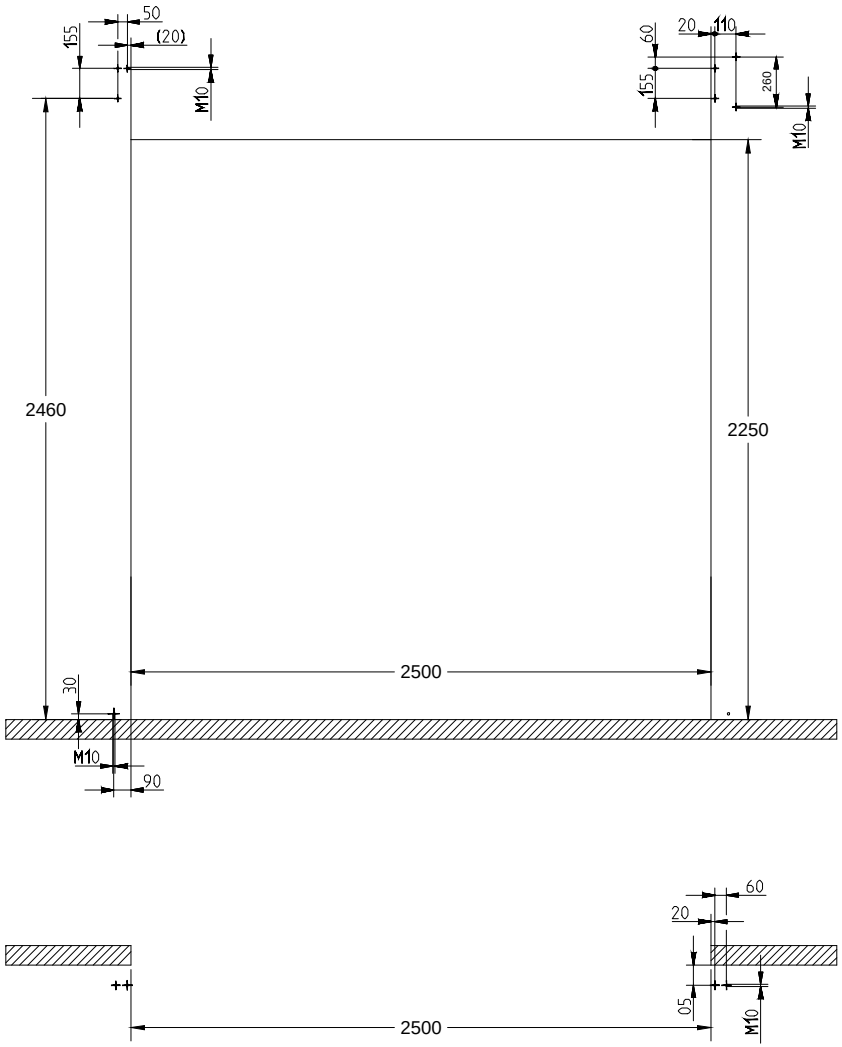

CLEAR WIDTH(DW)	CLEAR HEIGHT(DH)	QTY
2500mm	2250mm	01 NOS

TOLERANCE - ±10mm

This drawing & design is the property of NIHVA TECHNOLOGIES. Not to be sold or copied to any other concern.

TITLE
FIXING PLAN OF RP300

NIHVA TECHNOLOGIES PVT. LTD.

NIHVA TECHNOLOGIES PVT. LTD. PUNE
Tel : 020 66304033
Email:- info@nihva.com
Website:- www.nihva.com

	NAME	SIGN	DATE
DRAWN	OMKAR		27-04-2018
CHECK	PRADEEP		27-04-2018
APPRD.	PRADEEP		27-04-2018

CLIENT - ABB GROUP
PROJECT -
SITE LOCATION - BANGLORE
If any queries contact : design@nihva.com
DWG. NO. : NIHVA/18-19/0021
REV- 0
ALL DIMENSION ARE IN mm
SCALE: NTS
WT:
SHEET: 01 OF 01