


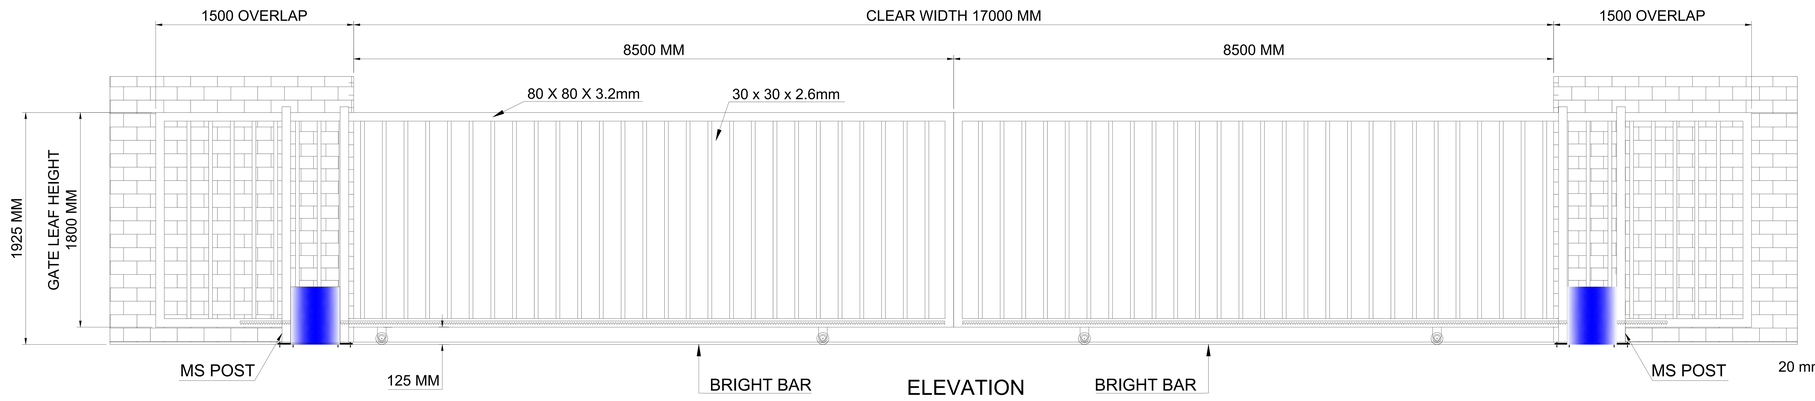


ELEVATION

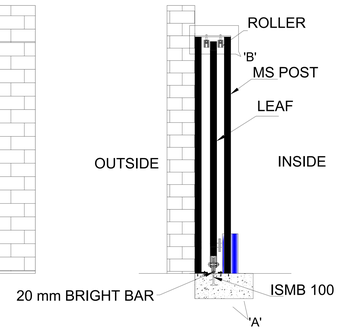


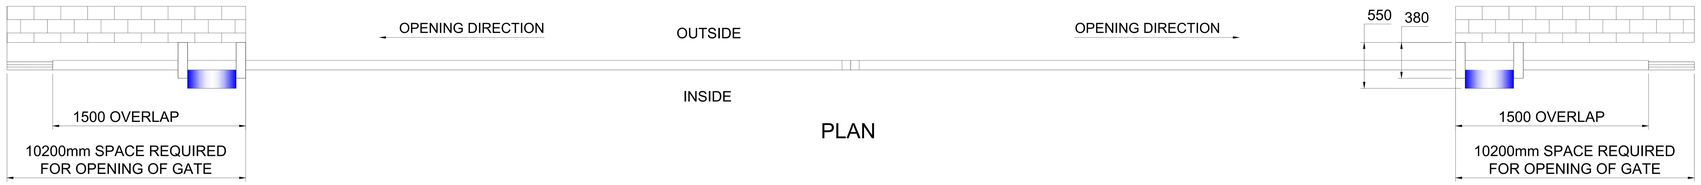

PLAN

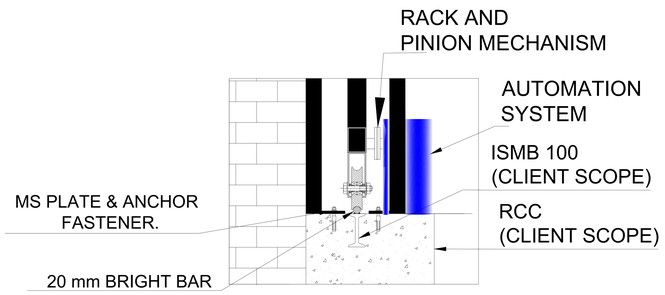

DETAIL VIEW OF A

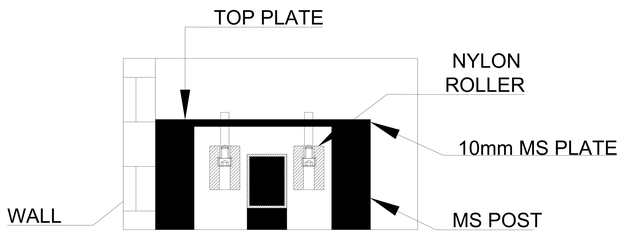

DETAIL VIEW OF B

04	RAL 7035	LIGHT GREY
03	RAL 5002	ULTRAMARINE BLUE
02	RAL 9002	GREY WHITE
01	RAL 1004	GOLDEN YELLOW
SR.NO	RAL CODE	RAL COLOR

TOLERANCE ± 10 MM.

NOTE-
1. ALL REQUIRED CIVIL WORK WILL BE IN CLIENTS SCOPE.
2.IN NECESSARY GATE LEAF WILL BE IN TWO OR THREE PARTS FOR TRANSPORTATION AND WILL BE WELDED TOGETHER ON SITE.

17000 mm	1800 mm	1 NO
CLEAR WIDTH	CLEAR HEIGHT	QUANTITY

This drawing & design is the property of NIHVA TECHNOLOGIES. Not to be sold or copied to any other concern.

TITLE
AUTOMATIC BI PARTING SLIDING GATE

	NAME	SIGN	DATE
DRAWN	P.A		08.09.2020
CHECK	G.J		08.09.2020
APPRD.			

If any queries contact : design@nihva.com

ALL DIMENSION ARE IN mm

NIHVA
NIHVA TECHNOLOGIES PVT. LTD.

NIHVA TECHNOLOGIES PVT. LTD. PUNE
Tel : 020 66304033
Email:- info@nihva.com
Website:- www.nihva.com

CLIENT - HIRANANDANI
PROJECT - VESTAS
SITE LOCATION - CHENNAI
DWG. NO. : NIHVA/20-21/0051 REV- R00
SCALE: NTS WT: SHEET: 01 OF 01