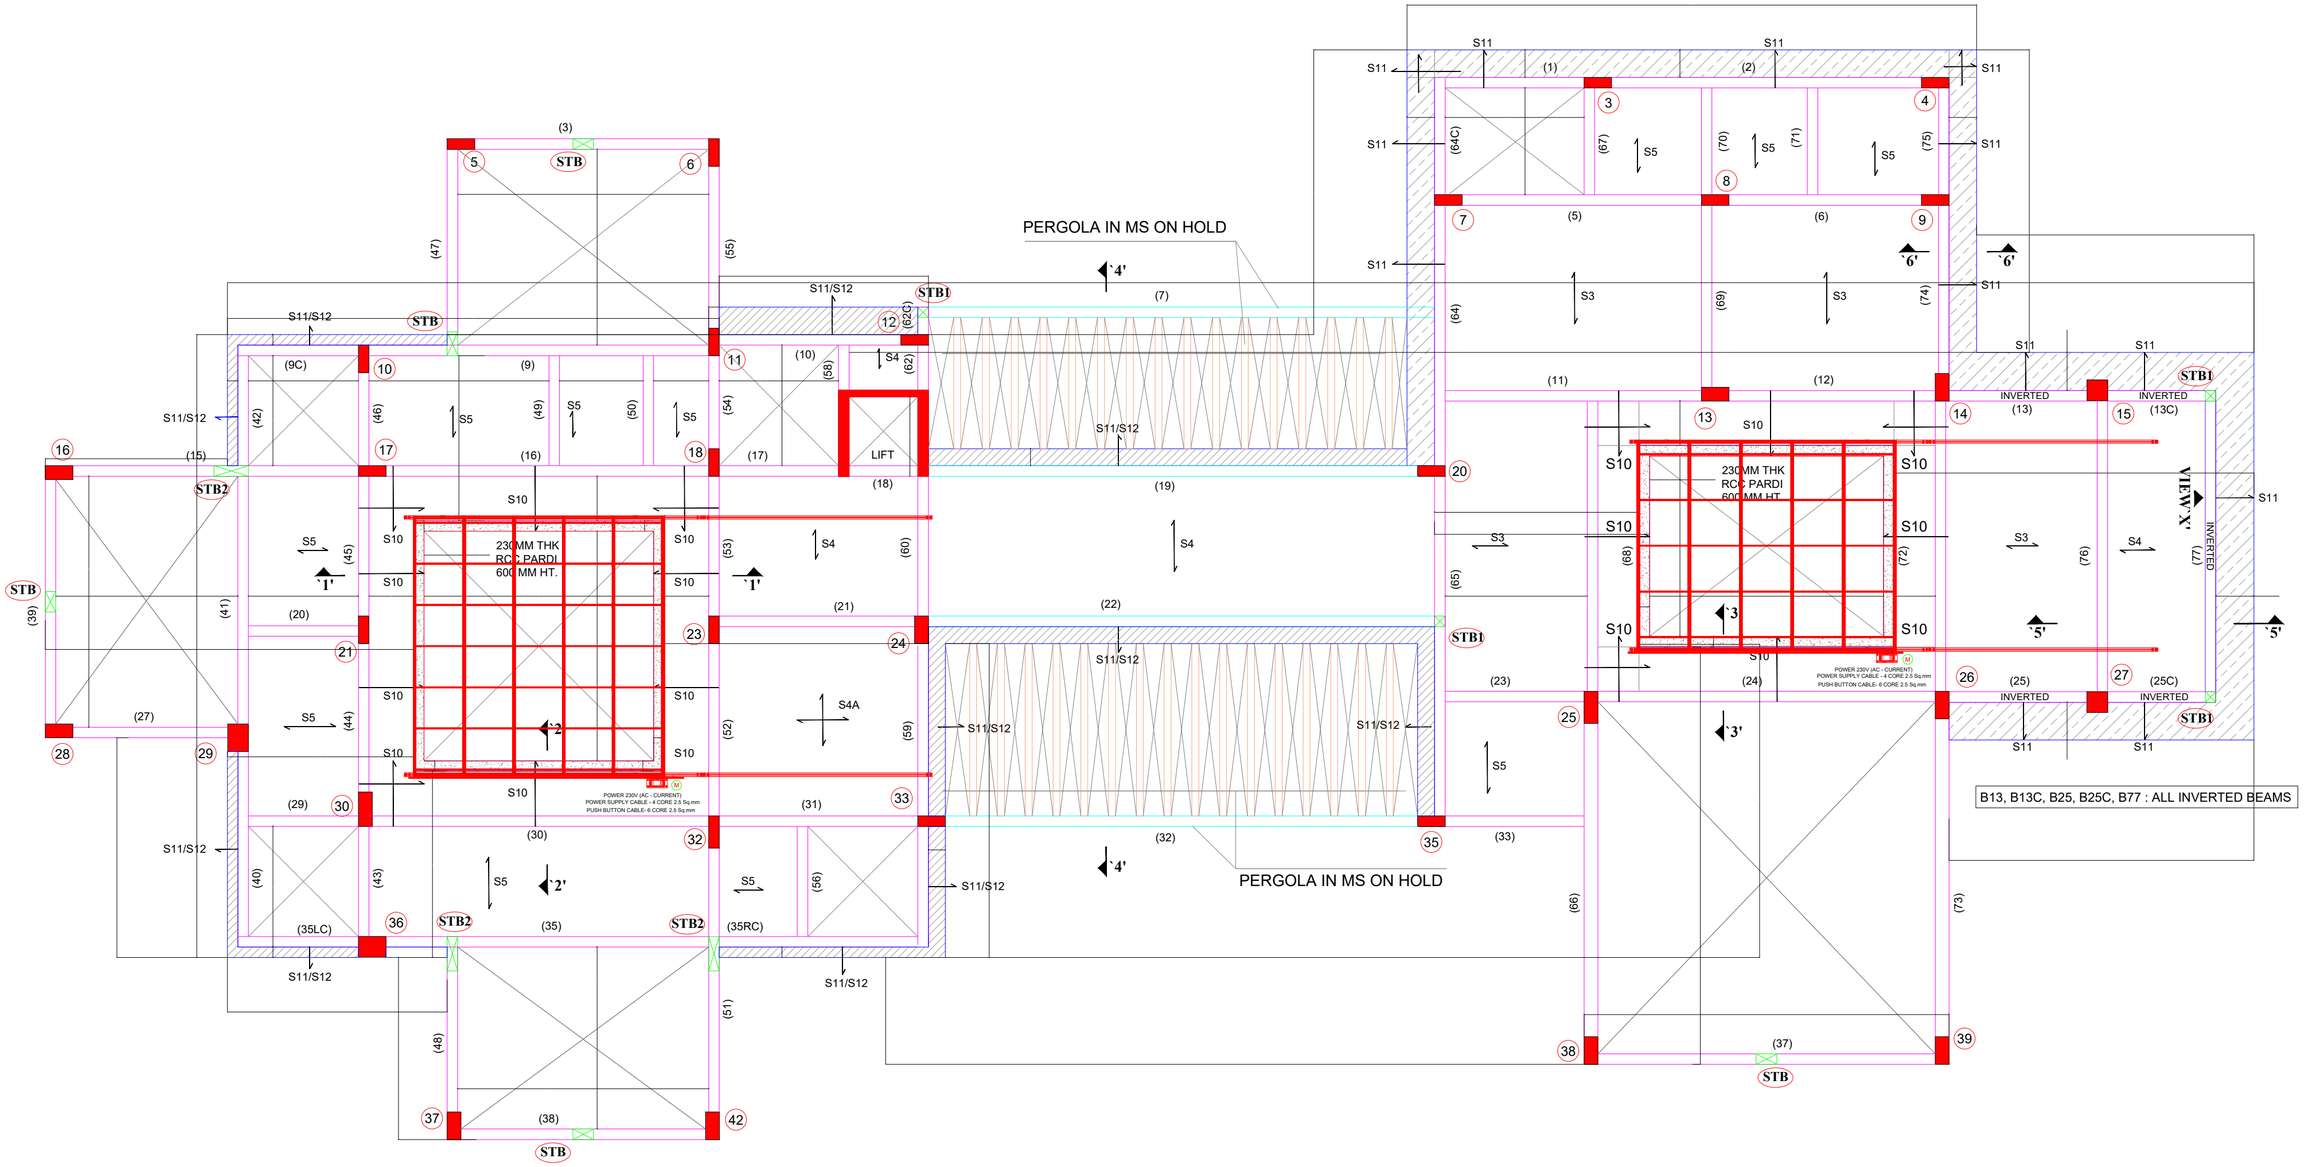


2ND RCC SLAB FRAMING PLAN

GOOD FOR EXECUTION

REVISION	DATE	DESCRIPTION
R0	21.07.26	–

BRIEF NOTES :

FN-DD-DF-02 R0 - 01.09.10

SCHEDULE OF OPENINGS

TYPE	SIZE	SILL LVL	LINTLE LVL

DRAWING TITLE : WORKING DRAWING

SUB TITLE : 2ND RCC FRAMING PLAN

PROJECT NAME : PROPOSED FARM HOUSE AT HISSA NO. 2, S. NO. 402 AT BHUGAON, TAL. MULSHI, PUNE FOR MR. DAVE.

axis paradigm spaces (i) p. ltd. architecture and interior design
3, Omkar, Plot No.-20, Madhavbaug. Co.Op.Hsg.Soc. Shivtirthnagar, Kothrud, Pune-38
tel.:+91-9923004917 e-mail:architects@axisassociates.com

NORTH

SCALE	JOB NO.	DRAWN BY	APPROVED BY	DATE	COMPUTER FILE
N.S.T.	00-R-P00	MVH	ARP	21.07.26	----