
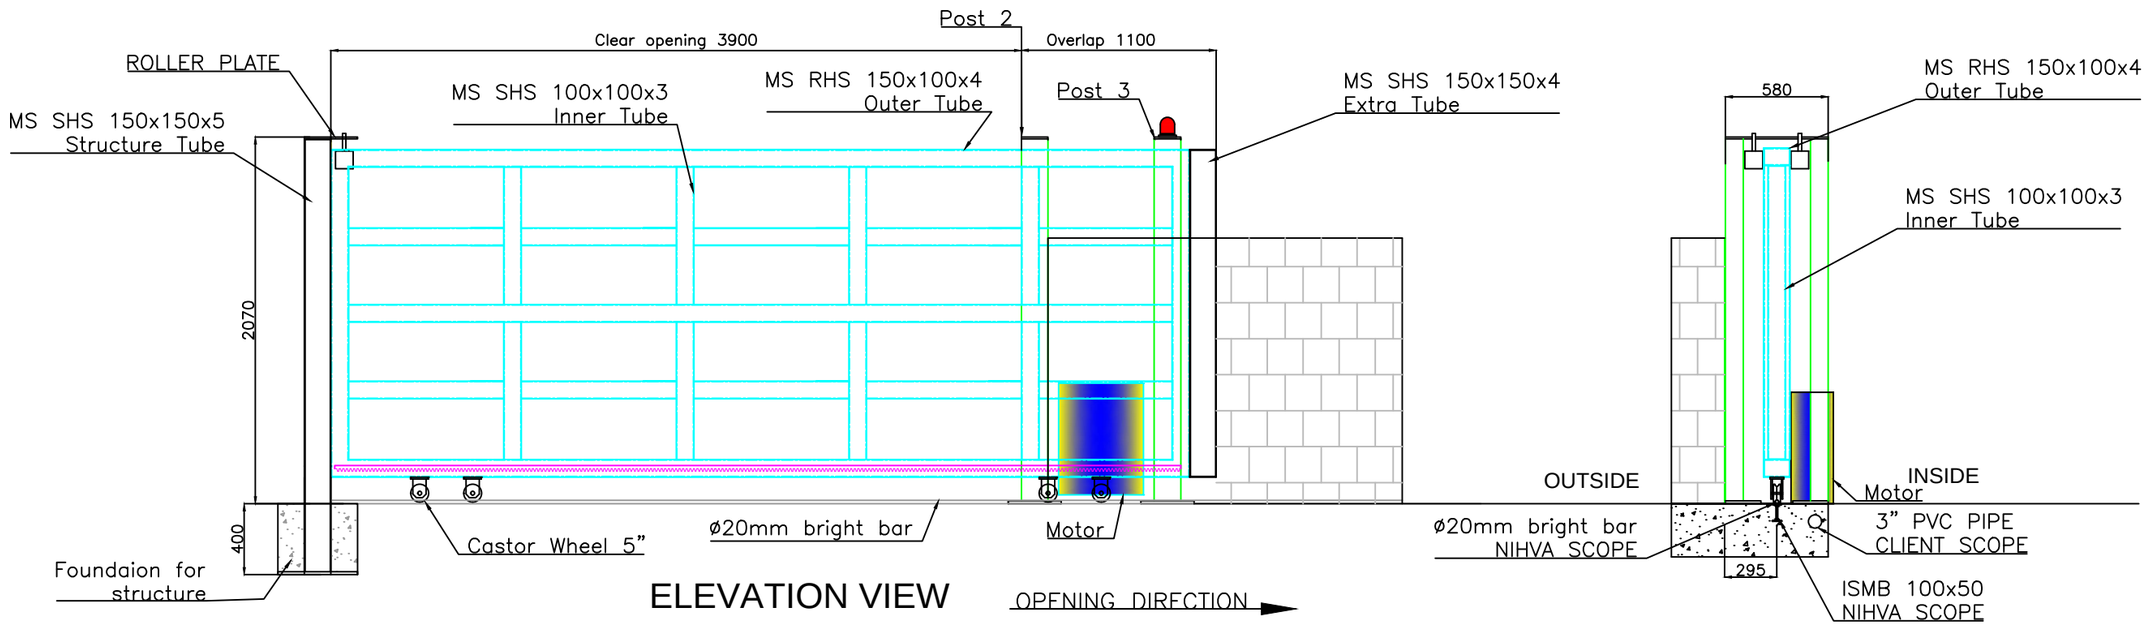


ELEVATION VIEW

OPENING DIRECTION

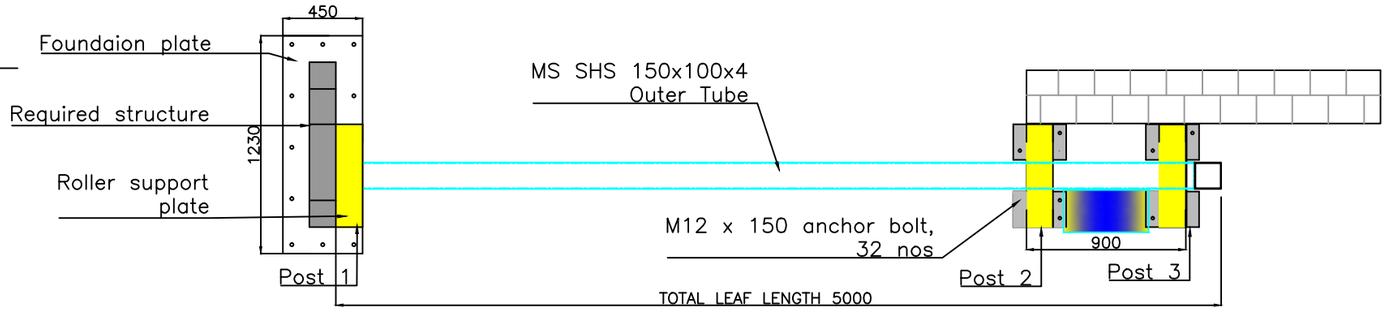

PLAN

Note-

1. All dimension are in mm.
2. All civil work is under client scope.
3. 3" PVC pipe in the foundation to be provided by client.
4. Power supply single phase 230v, 50hz.
5. Cable for power supply 2.5 sqmm 3 core
6. Cable for photocell - 1.5 sqmm 4 core

Rev 01-

1. Orientation changed from left to right.

Rev 02-

1. Foundation plate and structure added.
2. Post positions changed.
3. Clear opening changed to 3900.
4. Extra tube added to achieve clear opening.

Technical Specs of Motorized Sliding Gate

1. Opening length - 3900mm
2. Gate Height - 2000mm
3. Total leaf weight ≈ 790 kg
4. Parking length required - 5000mm
5. Outer tube size - MS SHS 150x100x4mm
6. Inner tube size - MS SHS 100x100x3mm
7. Extra support tube- MS SHS 150x150x4mm
8. Bottom Rail - Bright bar Ø20mm
9. Post size - MS SHS 150x100x4mm
10. T`Safety feature - Photocell and flashing light
11. Operation - Push button from side

This drawing & design is the property of NIHVA TECHNOLOGIES. Not to be sold or copied to any other concern.

TITLE			
SLIDING (EXIT) GATE SOUTH WEST			
	NAME	SIGN	DATE
DRAWN	G.P.		22.01.22
CHECK	A.K.		22.01.22
APPRD.	V.T.		22.01.22
If any queries contact : design@nihva.com			
ALL DIMENSION ARE IN mm			

NIHVA TECHNOLOGIES PVT. LTD.
NIHVA TECHNOLOGIES PVT. LTD. PUNE
Tel : 020 66304033
Email:- info@nihva.com
Website:- www.nihva.com

CLIENT -HAIMAVATHY PROPERTIES PVT. LTD.		
LOCATION - MUMBAI		
PRODUCT - SLIDING GATE 3900 X 2000		
NIHVA\20-21\191	REV- 02	
SCALE: NTS		SHEET: 01 OF 02