
Weitergabe sowie Vervielfältigung dieses Dokuments, Verwertung und Mitteilung seines Inhalts sind nur nach vorheriger ausdrücklicher schriftlicher Zustimmung von SMS Meer GmbH gestattet. Das Dokument ist vor unberechtigtem Zugriff Dritter zu schützen. Zuwiderhandlungen verpflichten zu Schadenersatz. Alle Rechte aus Patent-/Gebrauchsmuster-/Markenschutz vorbehalten

The reproduction, distribution and utilization of this document as well as the disclosure of its content to others without prior explicit written consent of SMS Meer GmbH is prohibited. Offenders will be held liable for the payment of damages. All rights reserved in case of patent/utility model/ornament protection.

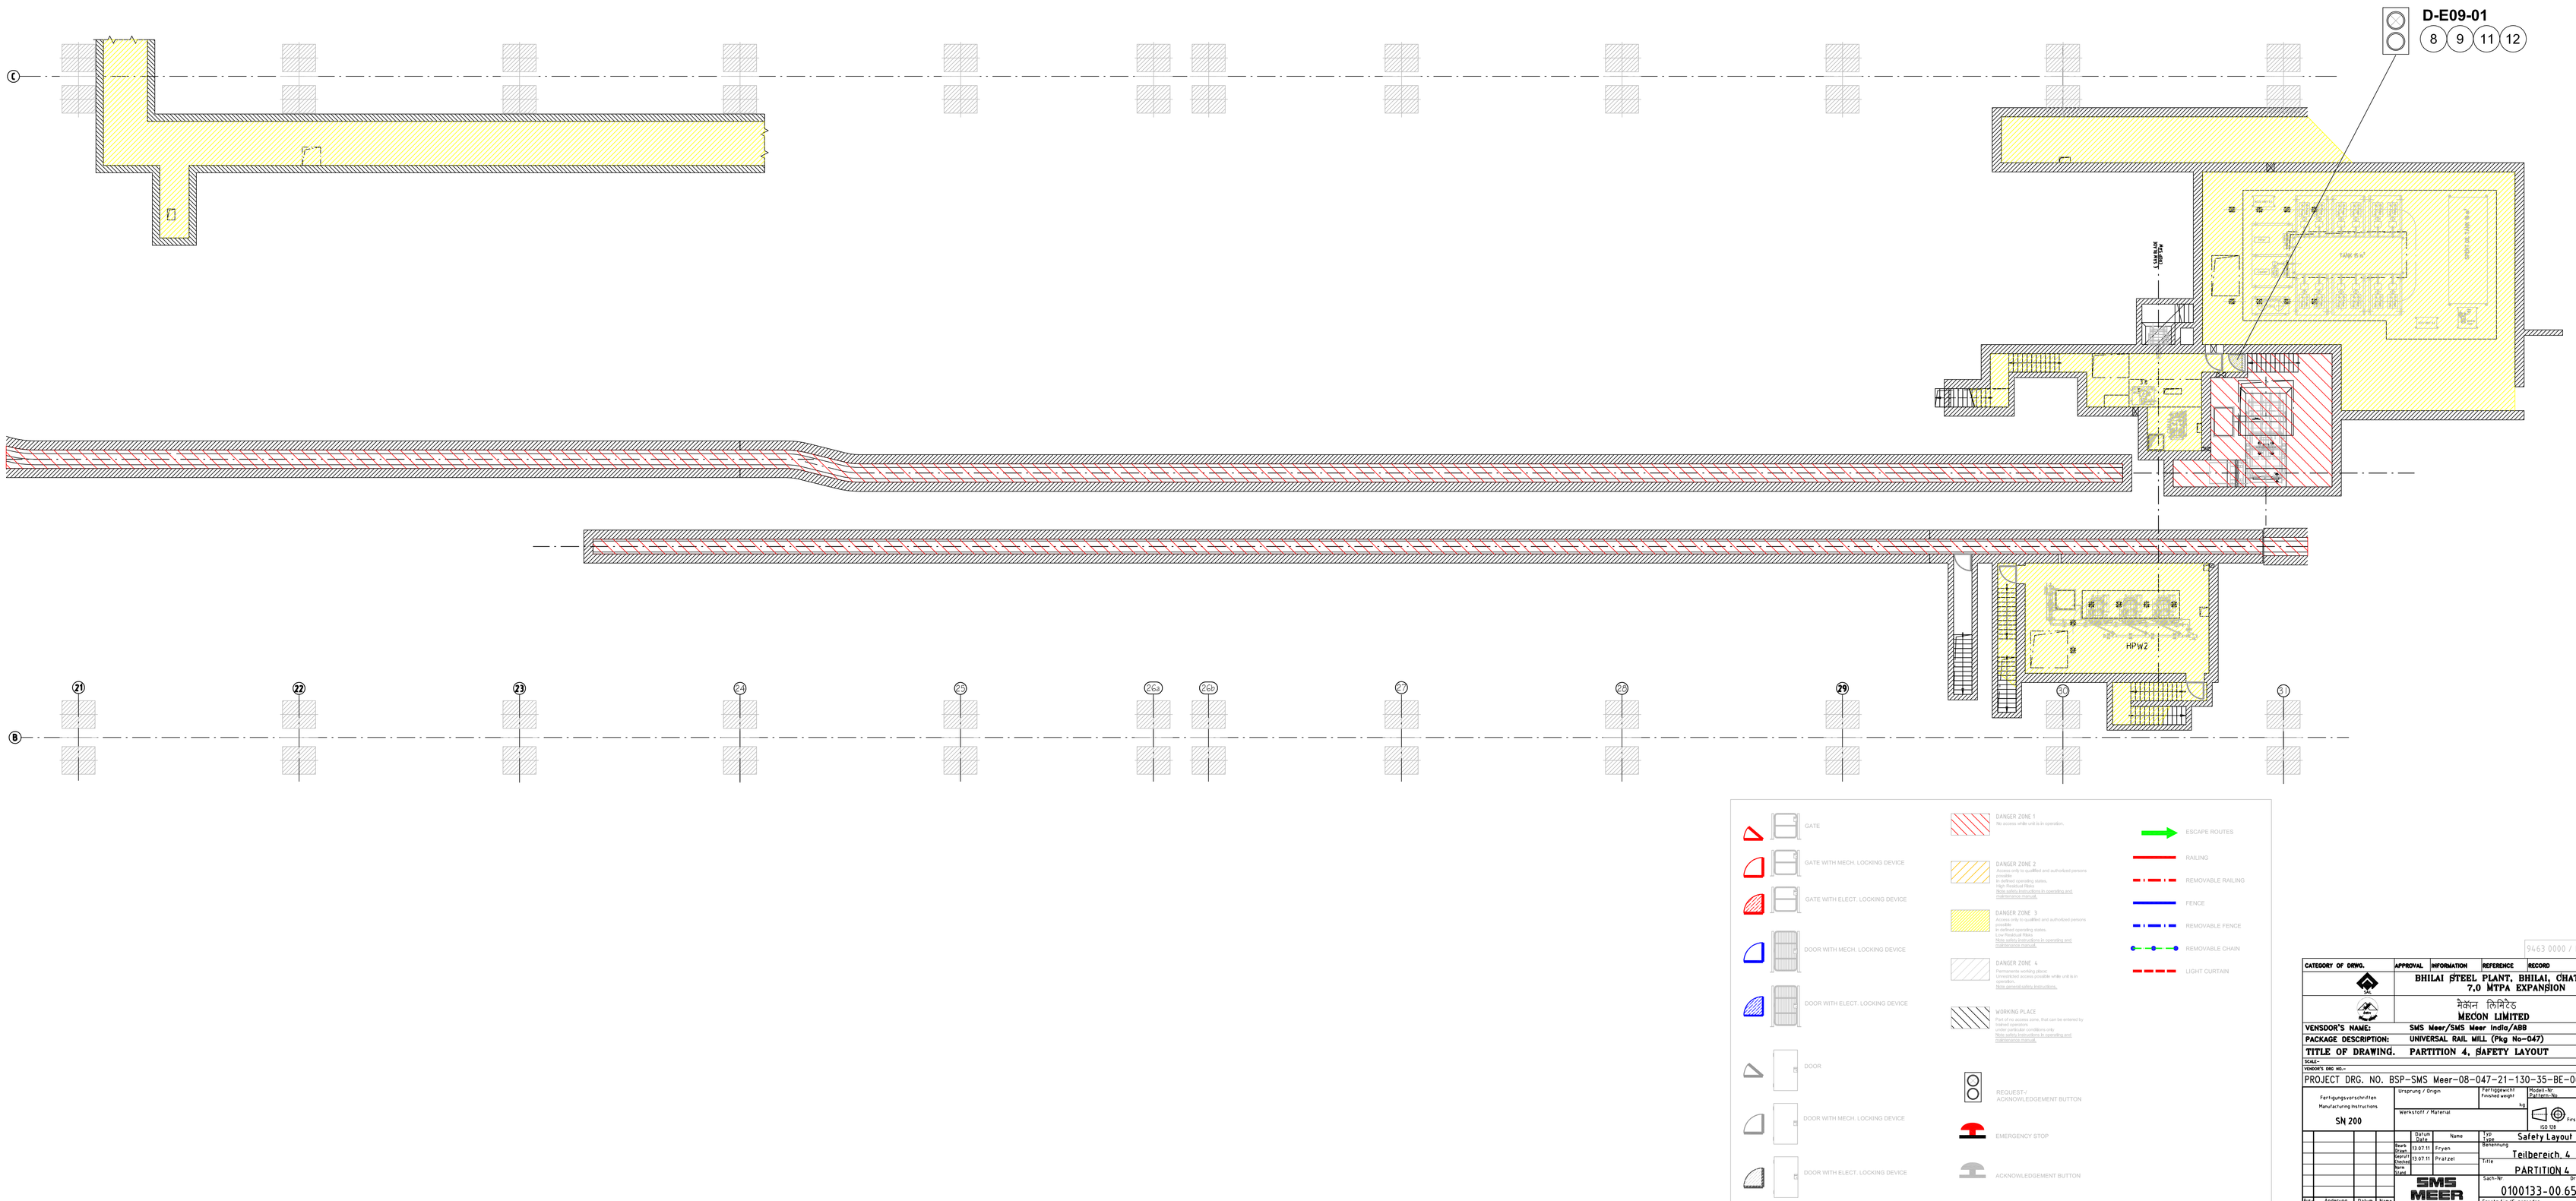

9463 0000 / RAILBHL

CATEGORY OF DRWG.	APPROVAL	INFORMATION	REFERENCE	RECORD	CONSTRUCTION

BHILAI STEEL PLANT, BHILAI, CHATTISGARH
7,0 MTPA EXPANSION

RAIL BARS
MECON LIMITED

VENDOR'S NAME: SMS Meer/SMS Meer India/ABB
PACKAGE DESCRIPTION: UNIVERSAL RAIL MILL (Pkg No-047)
TITLE OF DRAWING. PARTITION 4, SAFETY LAYOUT
SCALE:
VENDOR'S DRG NO.:
PROJECT DRG. NO. BSP-SMS Meer-08-047-21-130-35-BE-06652 REV. --

Fertigungsvorschriften / Manufacturing instructions: SN 200
Ursprung / Origin
Fertiggewicht / Finished weight: kg
Werkstoff / Material
Modell-Nr. / Pattern-No.
Projektionsmethode / First angle projection method ISO 128

	Datum / Date	Name	Typ / Type: Safety Layout	Maßstab / Scale
Bearb. / Dsgn.	13.07.11	Fryen	Bezeichnung / Title: Teilbereich 4	1:100
Gepr. / Checked	13.07.11	Pratzel	PARTITION 4	
Norm / Appd.			Sach-Nr. / Drawing-No: 0100133-00.652	Blatt / Sheet 2 / 2 Blatt / Sheets

Ausg. / Issue	Änderung / Revision	Datum / Date	Name

SMS MEER
SMS group

Ersatz für / Supersedes
Ersatz durch / Superseded by

Diese Zeichnung und alle darauf enthaltenen Informationen sind vertraulich. This drawing and all information on it is confidential.

A0