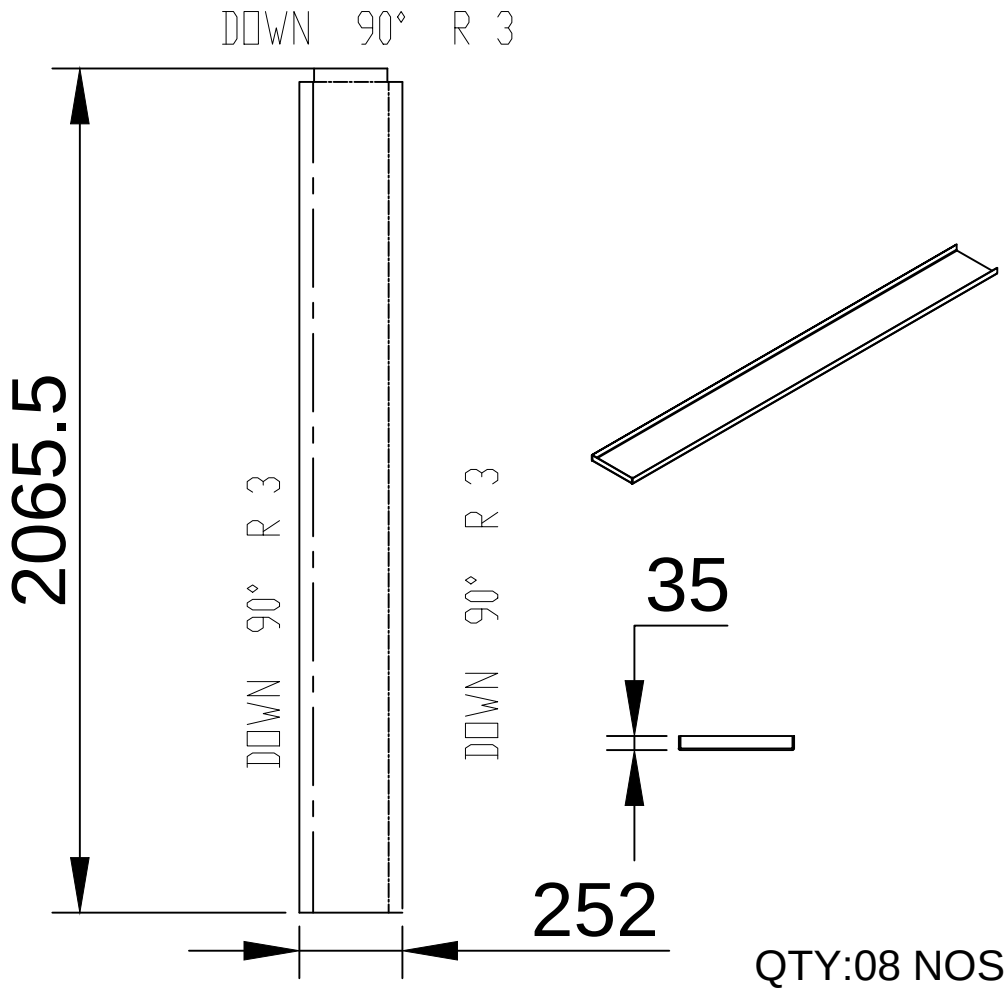

QTY:08 NOS

This drawing & design is the property of NIHVA TECHNOLOGIES. Not to be sold or copied to any other concern.

SINGLE LEAF LEFT SIDE
CRM DOOR 05

NIHVA TECHNOLOGIES PVT. LTD.

NIHVA TECHNOLOGIES
PVT. LTD. PUNE
Tel : 020 66304033
Email:- info@nihva.com
Website:- www.nihva.com

	NAME	DATE
DRAWN	KISHAN	16/05/2022
CHECK	M.SUTAR	16/05/2022
APPRD.	V.TARAK	16/05/2022

If any queries contact : design@nihva.com

ALL DIMENSION ARE IN mm

CLIENT - NIHVA TECHNOLOGIES PVT LTD
LOCATION -
PRODUCT - SLIDING DOOR
DWG NO:-NIHVA/22-23/CLT/
SCALE: NTS | SCALE:-- 1:1 | SHEET:

Rev No.	Revision	Date	Revised By