


C1
QTY - 2

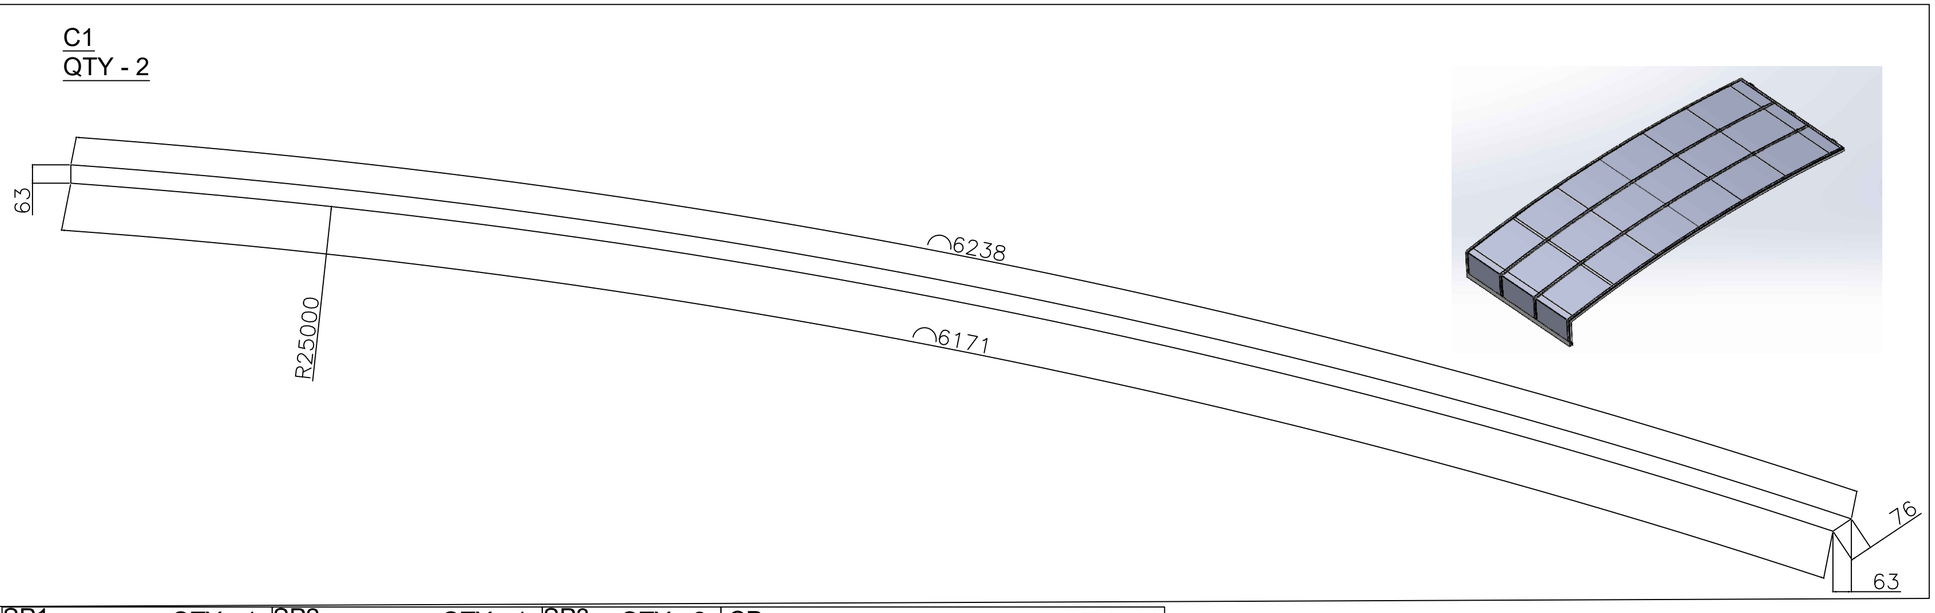


SP1 QTY - 1

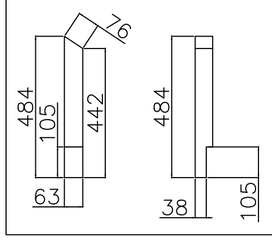


SP2 QTY - 1

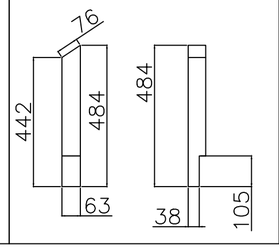


SP3 QTY - 2

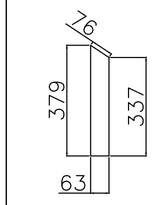

CP QTY - 90

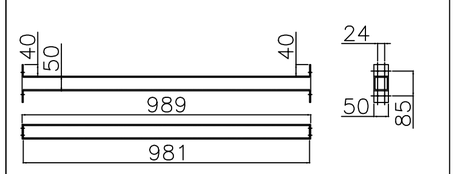

REV NO.	DESCRIPTION	Date	Revised By

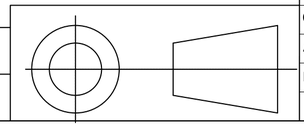

TITLE:- PANEL - 1

NIHVA TECHNOLOGIES PVT. LTD.

NIHVA TECHNOLOGIES PVT. LTD. PUNE
Tel : 020 66304033
Email:- info@nihva.com
Website:- www.nihva.com

	NAME	DATE	SIGN
DRAWN	MAHESH S.	22/10/22	
CHECK	MAHESH S.	22/10/22	
APPRD.	VIJAY T.	22/10/22	

If any queries contact : design@nihva.com

ALL DIMENSION ARE IN mm

CLIENT - NIHVA TECHNOLOGIES PVT.LTD

LOCATION -

PRODUCT: FIX & RETRACTABLE ROOF

DWG NO:-NIHVA/22-23/MFG/0048 | REV- 0

SCALE: NTS | SCALE:-- 1:1 | SHEET: 01 OF 01