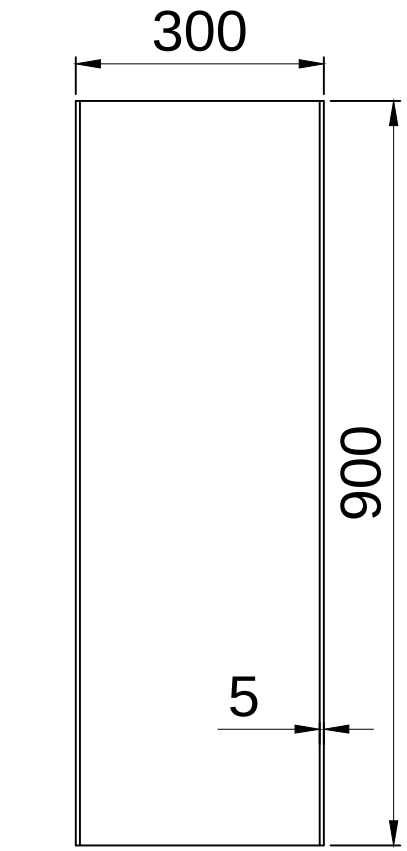

PLAIN SHEET 400 X 5 THK X 900L = 01 NO

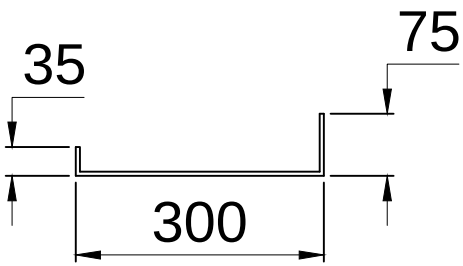

This drawing & design is the property of NIHVA TECHNOLOGIES. Not to be sold or copied to any other concern.

TITLE	BEND PLATE			NIHVA TECHNOLOGIES PVT. LTD. PUNE
	NAME	SIGN	DATE	Tel : 020 66304033
DRAWN	P.A		03.12.18	Email:- info@nihva.com
CHECK	P.A		03.12.18	Website:- www.nihva.com
APPRD.	R.D		03.12.18	CLIENT -
If any queries contact : design@nihva.com				PROJECT -
ALL DIMENSION ARE IN mm				SITE LOCATION -
DWG. NO. : NIHVA/18-19/VDR/269				REV- 0
SCALE: NTS		WT:		SHEET: 01 OF 01