


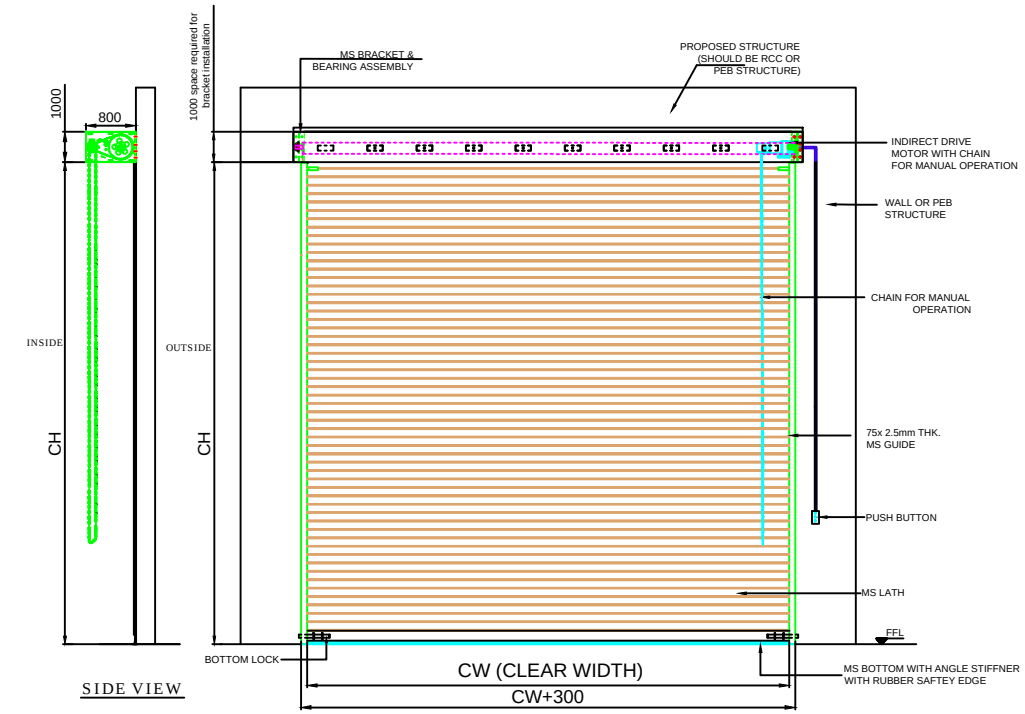


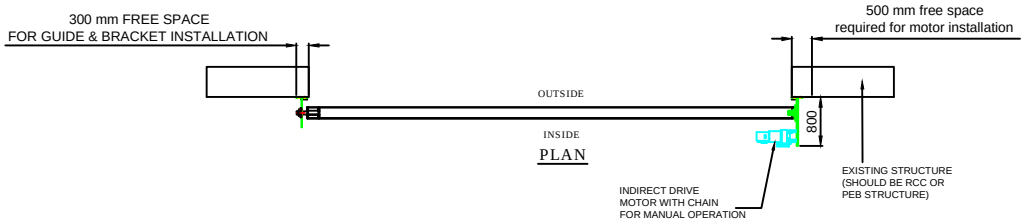

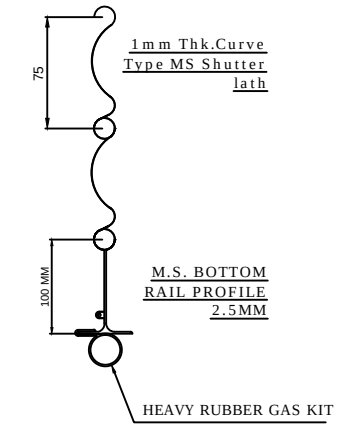

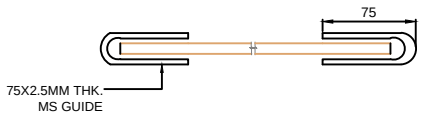

NOTE:-

1.REQUIRED STRUCTURE FOR ROLLING SHUTTER SHALL BE IN CLIENT SCOPE.
2. ALL REQUIRED CIVIL WORK IN CLIENT SCOPE.
3. FOR FINAL FINISH CLIENT SHOULD CONFIRM RAL COLOR SHADE.
4. 3 PHASE POWER SUPPLY SHOULD BE PROVIDE.

S.N.	LOCATION	SIZE	QUANTITY
1	-	4000(W)X4000(H)	01 NOS

TOLERANCE - ±10mm

This drawing & design is the property of NIHVA TECHNOLOGIES. Not to be sold or copied to any other concern.

TITLE				
MOTORISED ROLLING SHUTTER 4mX4m STRUCTURE				NIHVA TECHNOLOGIES PVT. LTD. PUNE
	NAME	SIGN	DATE	Website:- www.nihva.com Tel : 020 66304033 Email:- info@nihva.com
DRAWN	SURAJ		06.12.2018	CLIENT -REWARD
CHECK	PRADEEP		06.12.2018	PROJECT -
APPRD.	R.D		06.12.2018	SITE LOCATION - RANJANGAON.
If any queries contact : design@nihva.com				DWG. NO. : NIHVA/18-19/0193 REV- 0
ALL DIMENSION ARE IN mm				SCALE: NTS WT: SHEET: 01 OF 01