
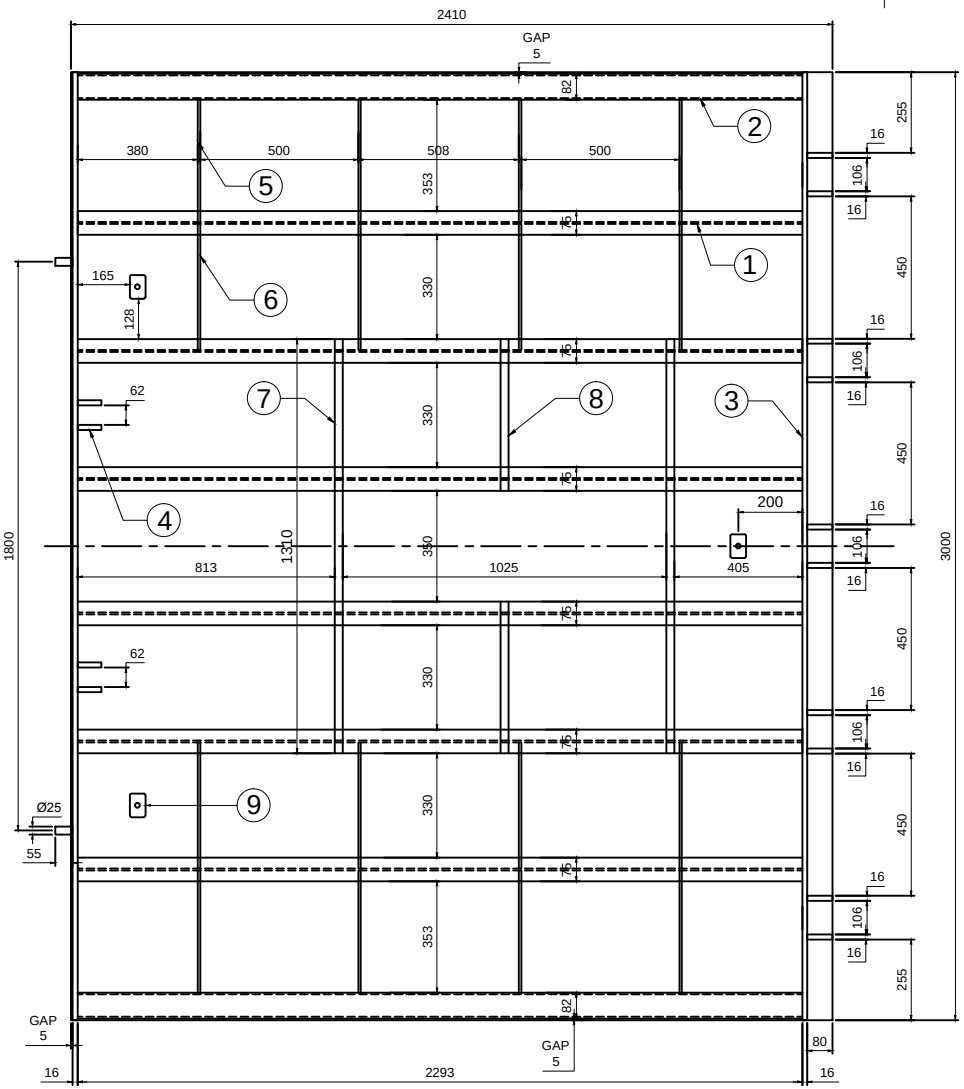


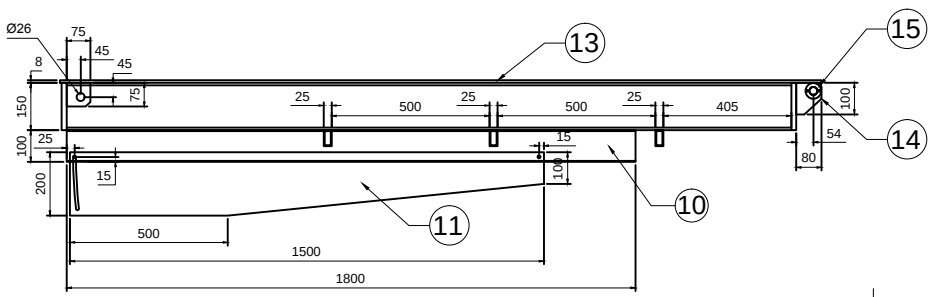

NOTE:~ MTL : MS

PART NO.	PART NAME	DESCRIPTION	QTY
1.	ISMB	150 X 75 X 2290L	6 NOS
2.	R.TUBE	145 X 82 X 4.8THK X 2290L	2 NOS
3.	FLAT	150 X 16 X 3000L	2 NOS
4.	FLAT	75 X 16 X 75L	4 NOS
5.	FLAT	150 X 8 X 385L	8 NOS
6.	FLAT	150 X 8 X 398L	8 NOS
7.	R.TUBE	50 X 25 X 3 X 1300L	2 NOS
8.	R.TUBE	50 X 25 X 3 X 480L	2 NOS
9.	FLAT	50 X 16 X 75L (M16 TAPPING)	3 NOS
10.	SIDE BEND	100 X 2THK X 1800L	2 NOS
11.	SIDE COVER	200 X 2 THK X 1500L	2 NOS
12.	LIP STOPER	Ø25 X 53L	2 NOS
13.	CHEQ.SHEET	2410 X 8 THK X 3000L	1 NO
14.	PROFILE	80 X 16 THK X 100L	10 NOS
15.	PROFILE	50 X 5 THK	2 NOS

This drawing & design is the property of NIHVA TECHNOLOGIES. Not to be sold or copied to any other concern.

TITLE

DECK ASSLY

NIHVA TECHNOLOGIES PVT. LTD.

NIHVA TECHNOLOGIES PVT. LTD. PUNE
Tel : 020 66304033
Email:- info@nihva.com
Website:- www.nihva.com

	NAME	SIGN	DATE
DRAWN	P.A		20.08.2020
CHECK	G.J		20.08.2020
APPRD.			

If any queries contact : design@nihva.com

ALL DIMENSION ARE IN mm

CLIENT -

PROJECT - NDL_630_631

SITE LOCATION -

DWG. NO. : NIHVA/20-21/VDR/0046

SCALE: NTS | WT: | REV- 00