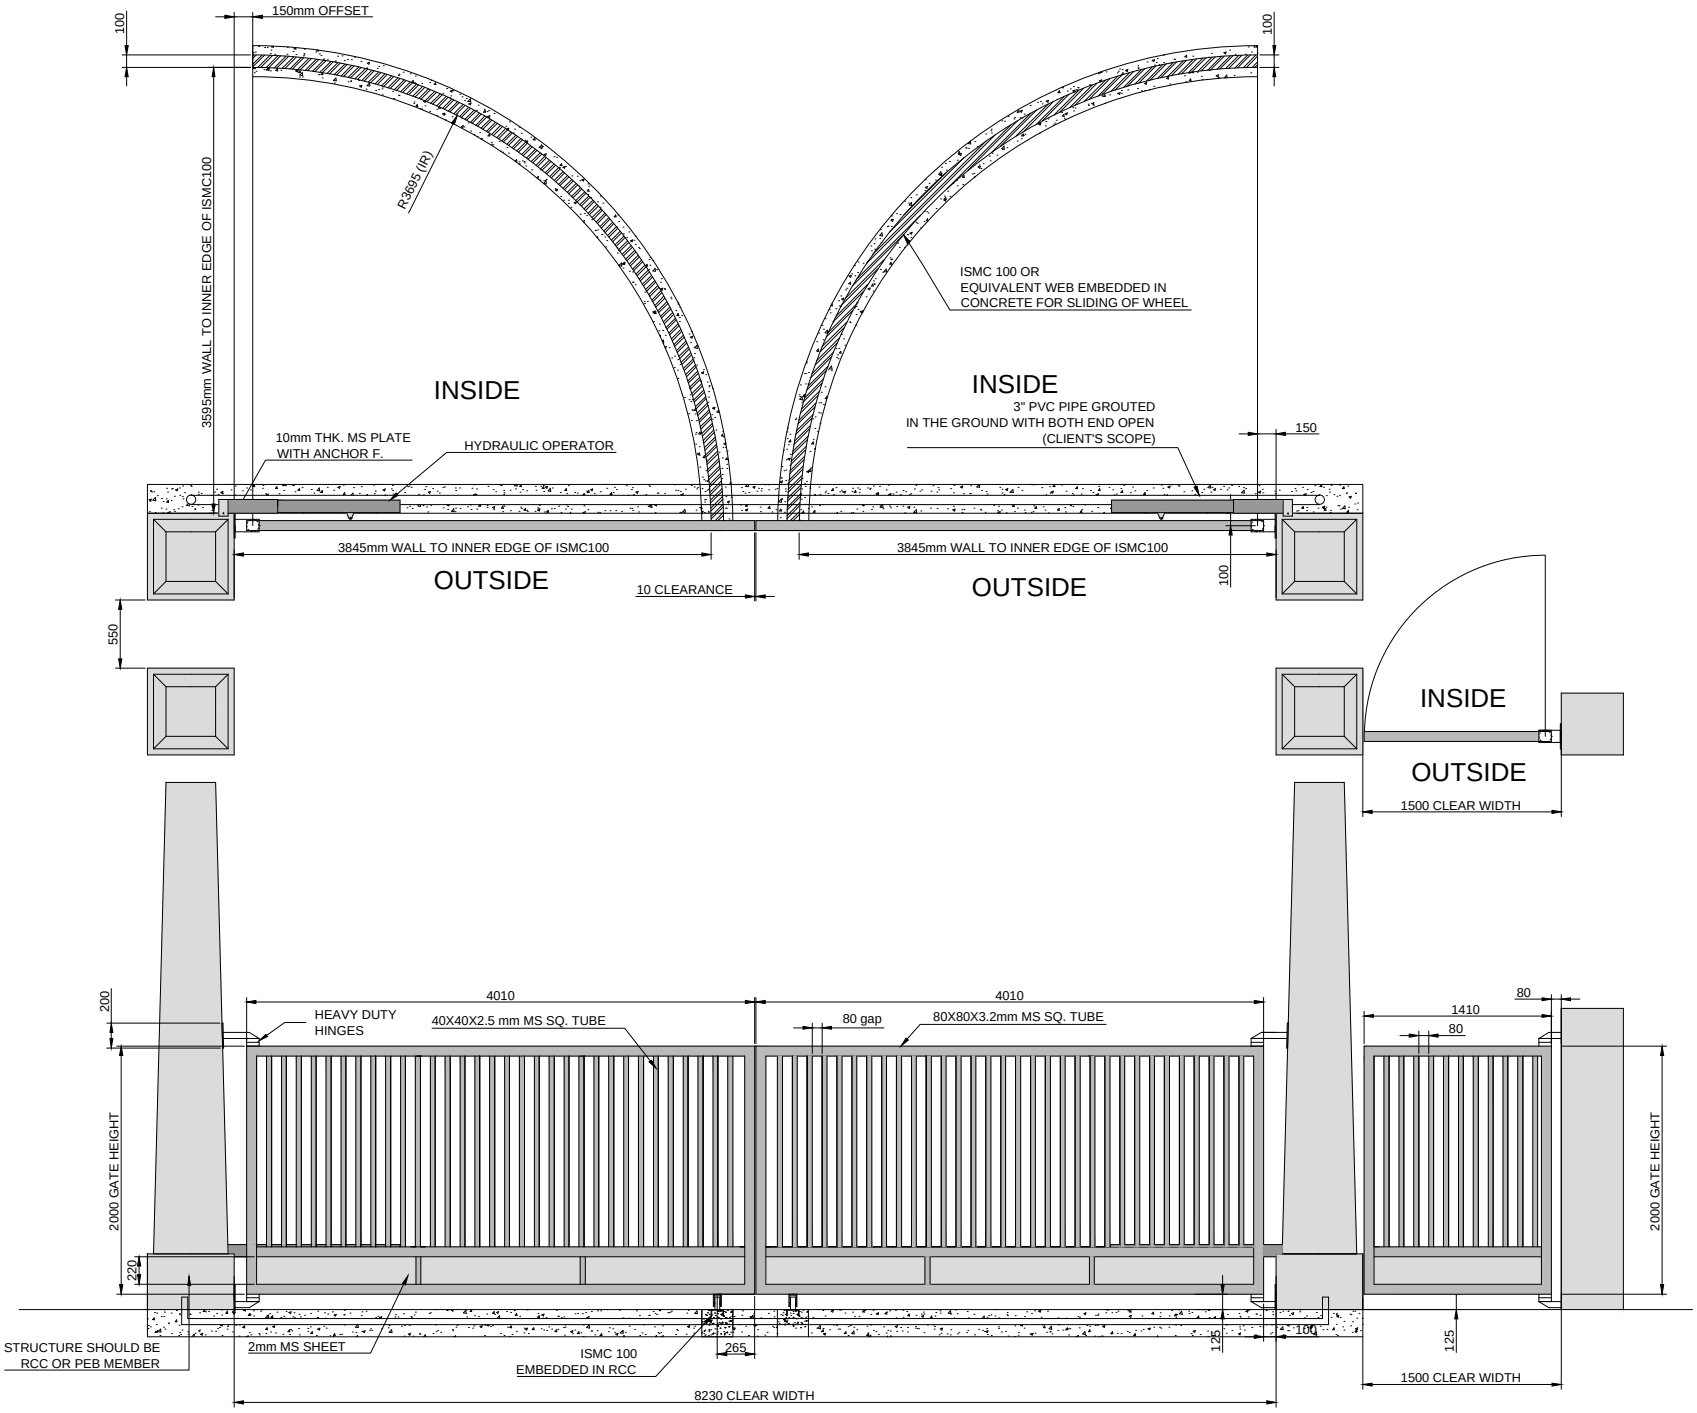

OUTSIDE ELEVATION

DIMENSION :

CLEAR WIDTH	CLEAR HEIGHT	QUANTITY
8230 mm	2000 mm	01 NOS.
1500 mm	2000 mm	01 NOS.

MATERIAL SPECIFICATIONS:

SR NO.	TUBE SIZES	
1	80x80x3.2mm MS TUBE	OUTER TUBE
2	40x40x2.5mm MS TUBE	INNER TUBE
3	2mm MS SHEET	AT BOTTOM

MODIFICATIONS DONE:-
1. SWING GATE HAVE TO BE SHIFTED TO INSIDE COLUMN FOR AUTOMATION.

NIHVA TECHNOLOGIES PVT. LTD.
NIHVA TECHNOLOGY PVT. LTD. PUNE
Email:- info@nihva.com
Website:- www.nihva.com

TITLE:

AUTOMATIC SWING GATE & MANUAL WICKET GATE

CLIENT'S APPROVAL :

CLIENT - LUPIN LIMITED

PROJECT -

SITE LOCATION - SIKKIM

DWG. NO. : NIHVA/16-17/0098/R04

SCALE: NTS	WT:	SHEET:1 OF 1
DRAWN BY: OMKAR		DATE: 01-12-2016
CHECK : SAGAR P.		DATE: 01-12-2016

If any queries contact : projects@nihva.com

NOTE: ALL DIMENSION ARE IN mm

THIS DRAWING & DESIGNING IS THE PROPERTY OF NIHVA TECHNOLOGIES. NOT BE SOLD OR COPY TO ANY OTHER CONCERN.