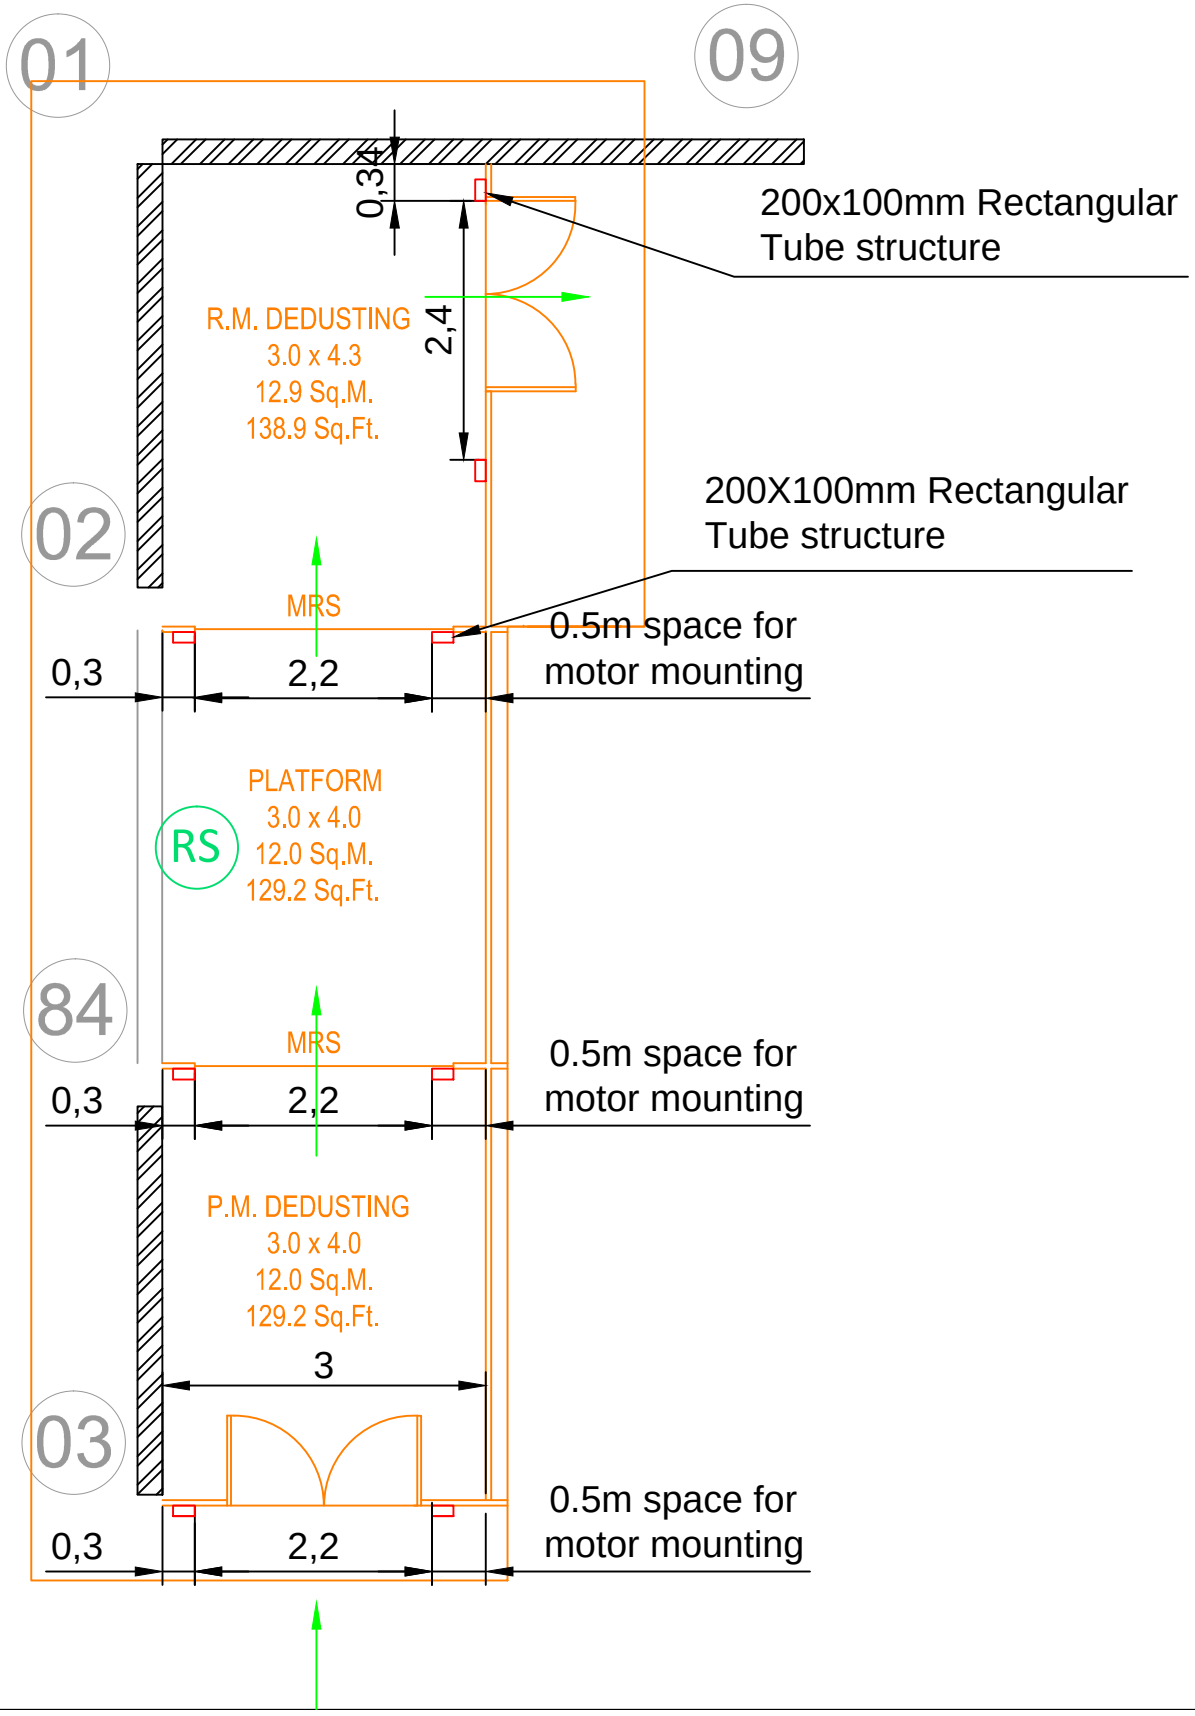

01
09
0,34
200x100mm Rectangular
Tube structure
R.M. DEDUSTING
3.0 x 4.3
12.9 Sq.M.
138.9 Sq.Ft.
2,4
02
200X100mm Rectangular
Tube structure
MRS
0,3
2,2
0.5m space for
motor mounting
PLATFORM
3.0 x 4.0
12.0 Sq.M.
129.2 Sq.Ft.
RS
84
MRS
0,3
2,2
0.5m space for
motor mounting
P.M. DEDUSTING
3.0 x 4.0
12.0 Sq.M.
129.2 Sq.Ft.
3
03
0,3
2,2
0.5m space for
motor mounting