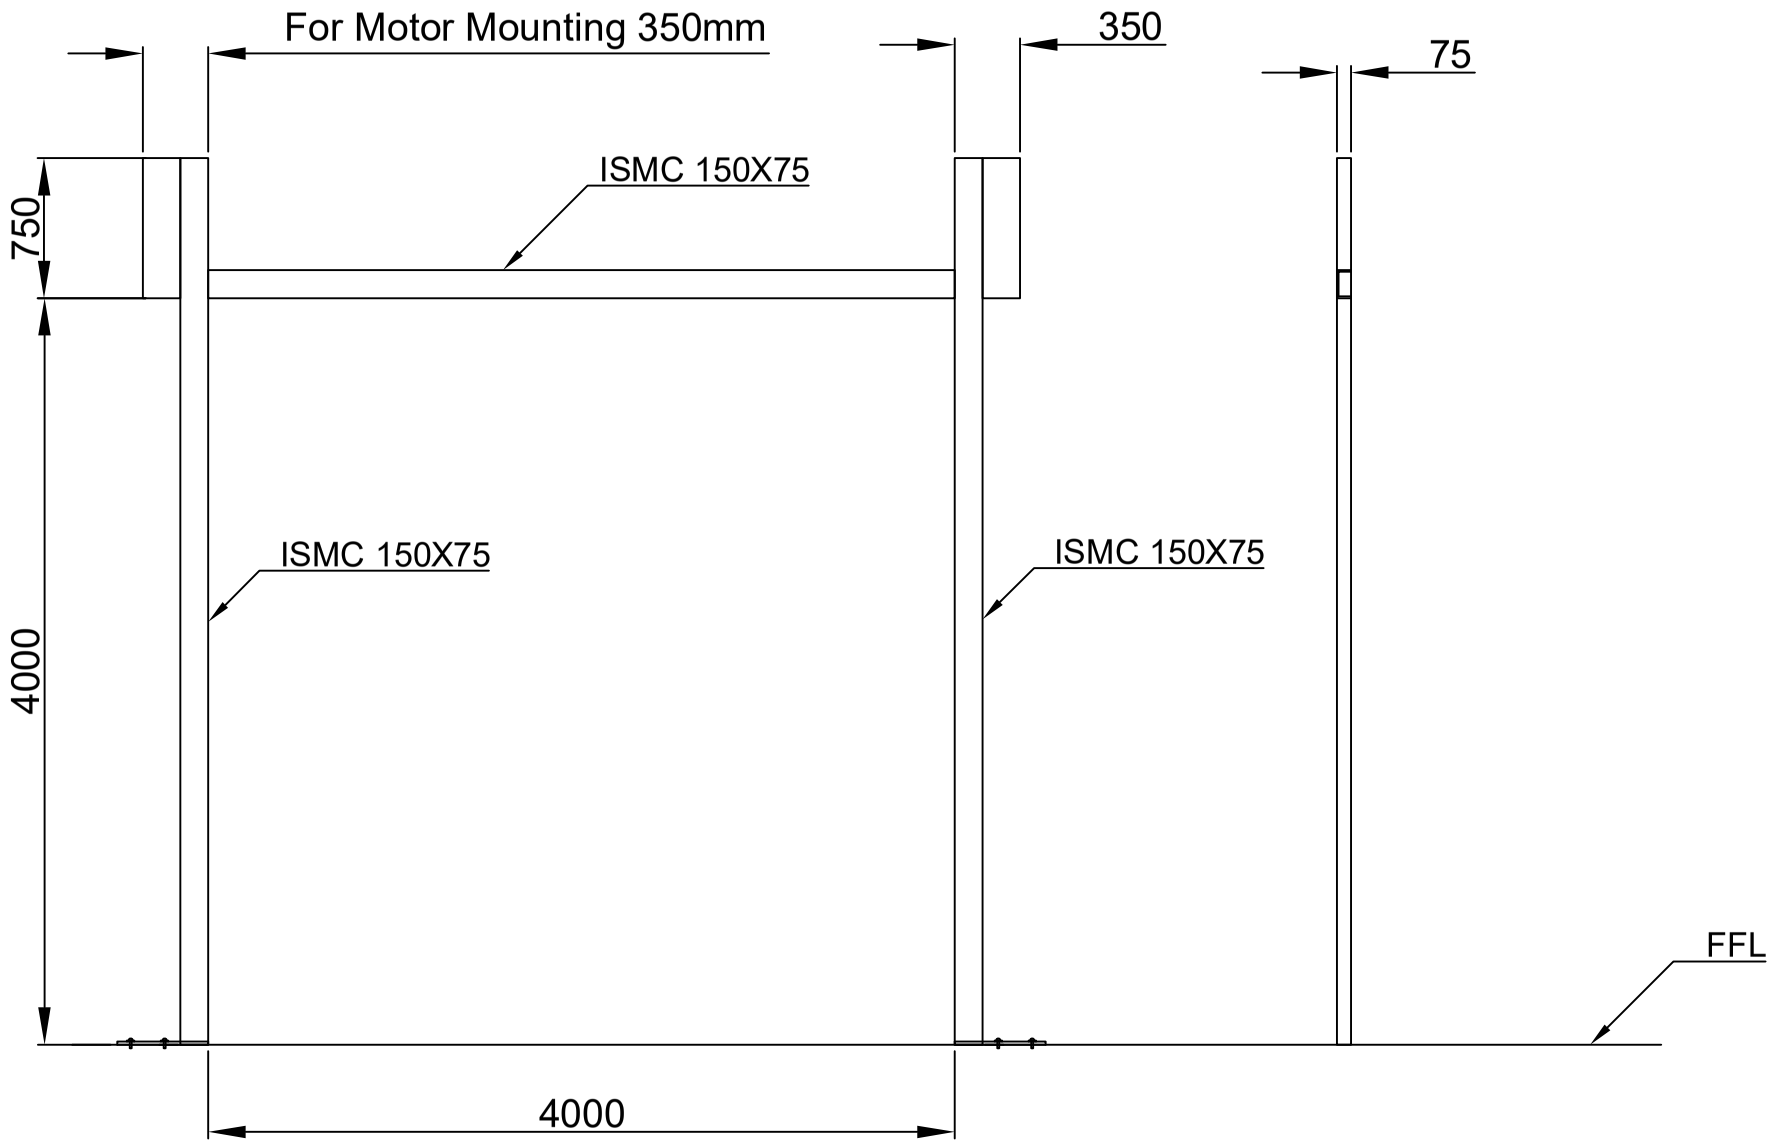


QTY : 1 NO

NOTE -
(1) ALL REQUIRED TECHNICAL MS STRUCTURE & FITTING IN CLIENT SCOPE .
(2) ALL CIVIL WORK IN CLIENT SCOPE .

This drawing & design is the property of NIHVA TECHNOLOGIES. Not to be sold or copied to any other concern.

TITLE	ALUMINUM HIGH SPEED DOOR STRUCTURE DWG		
	NAME	SIGN	DATE
DRAWN	S.B.		07/12/2021
CHECK	G.P		07/12/2021
APPRD.	A.K		07/12/2021

NIHVA TECHNOLOGIES PVT. LTD.
NIHVA TECHNOLOGIES PVT. LTD. PUNE
Tel : 020 66304033
Email:- info@nihva.com
Website:- www.nihva.com

CLIENT - MA ENGINEERING
PROJECT - JOHN DEERE
SITE LOCATION - PUNE
If any queries contact : design@nihva.com
DWG. NO. : NIHVA/21-22/CLT/0276 | REV- 0
ALL DIMENSION ARE IN mm
SCALE: NTS | WT: | SHEET: 01 OF 01