

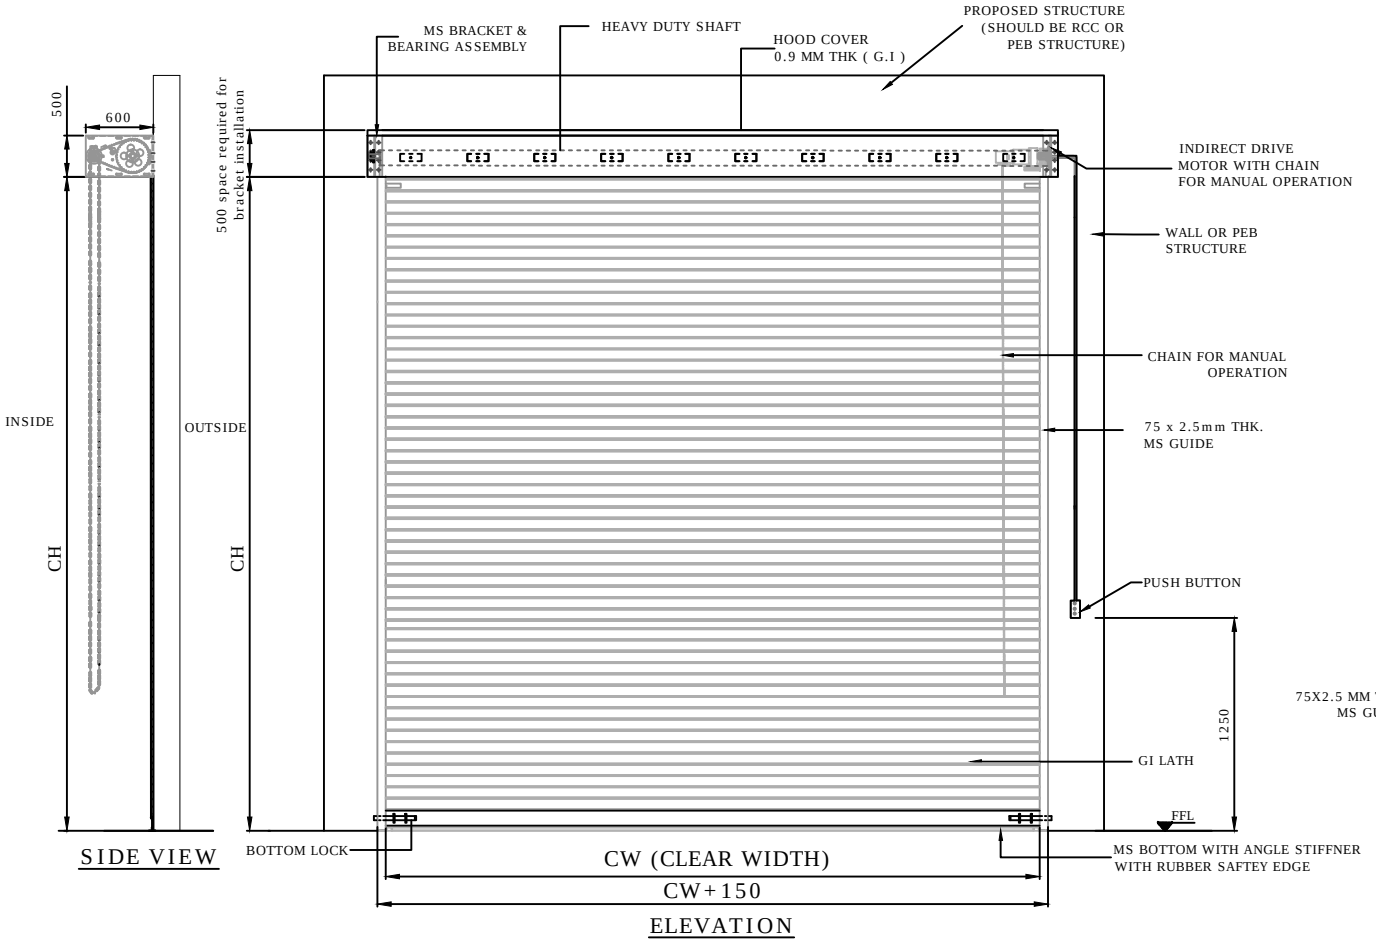


SIDE VIEW


ELEVATION

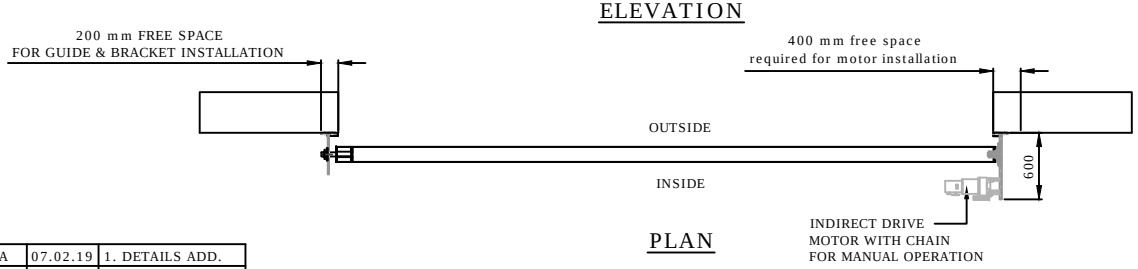

PLAN

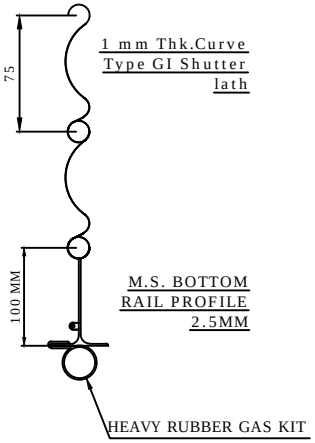

M.S. BOTTOM RAIL PROFILE 2.5MM

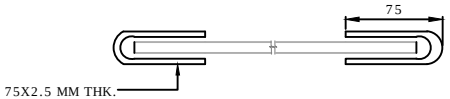

PLEASE TICK RAL CODE IN BOX

RAL 1003	
RAL 2004	
RAL 3000	
RAL 5002	
RAL 6005	
RAL 7035	
RAL 9005	
RAL 9010	

CLEAR WIDTH (CW)	CLEAR HEIGHT (CH)	QUANTITY
2400mm	3000mm	71 NOS

DIMENSION :

CLEAR WIDTH	CLEAR HEIGHT	QUANTITY
2400	3000	71 NOS

MATERIAL:

THICKNESS :

NOTE:
1. REQUIRED STRUCTURE FOR ROLLING SHUTTER WILL BE CLIENT'S SCOPE.
2. SINGLE PHASE. 3 CORE 1.5 SQ. CABLE REQUIRE AT SITE(CLIENT'S SCOPE)
3. IF SHUTTER IS STRUCTURE MOUNTED WE HAVE TO WELD GUIDE WITH STRUCTURE.
4. IF SHUTTER IS WALL MOUNTED PROVIDE HOLE PASS FLATS FOR ANCHORING IN WALL.

NIHVA TECHNOLOGIES PVT. LTD.
NIHVA TECHNOLOGIES PVT. LTD. PUNE
Email:- info@nihva.com
Website:- www.nihva.com

TITLE:

MOTORIZED ROLLING SHUTTER

CLIENT'S APPROVAL :

CLIENT - RELIANCE.

PROJECT -

SITE LOCATION - NILAKOTTAI (TAMILNADU)

DWG. NO. : NIHVA/18-19/0270/R01

SCALE: NTS	WT:	SHEET:1 OF 1

DRAWN BY: P.A	DATE: 07.02.2019
CHECK BY : P.A.	DATE: 07.02.2019
APPROVED BY :	DATE:

If any queries contact : projects@nihva.com

NOTE: ALL DIMENSIONS ARE IN mm

REV NO	DRAWN	DATE	REMARK
R01	P.A	07.02.19	1. DETAILS ADD.

THIS DRAWING & DESIGN IS THE PROPERTY OF NIHVA TECHNOLOGIES. NOT TO BE SOLD OR COPIED TO ANY OTHER CONCERN.