




02 ROOF PLAN
SCALE 1:200

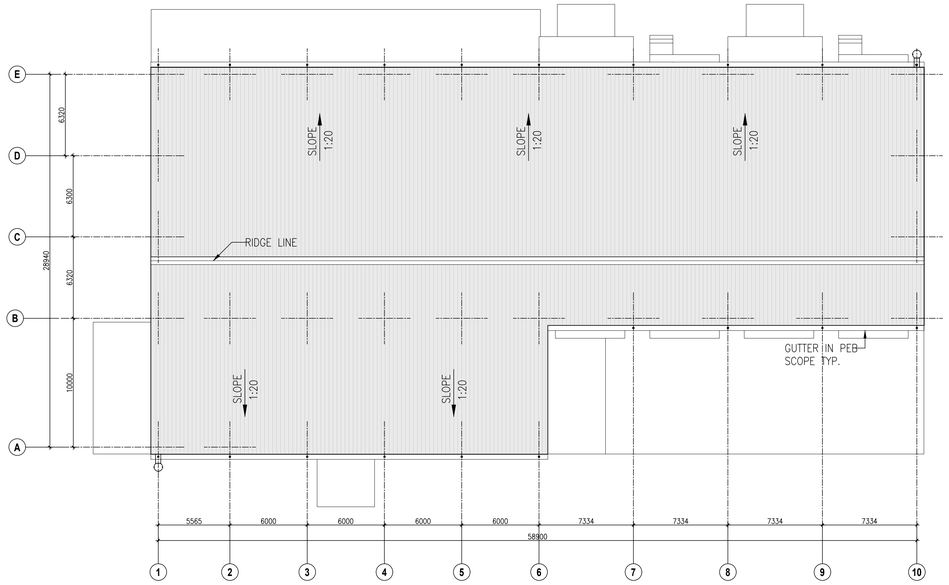


06 ELEVATION
SCALE 1:200

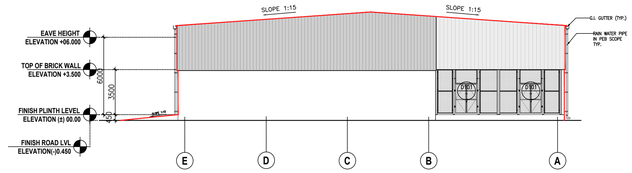


05 ELEVATION
SCALE 1:200

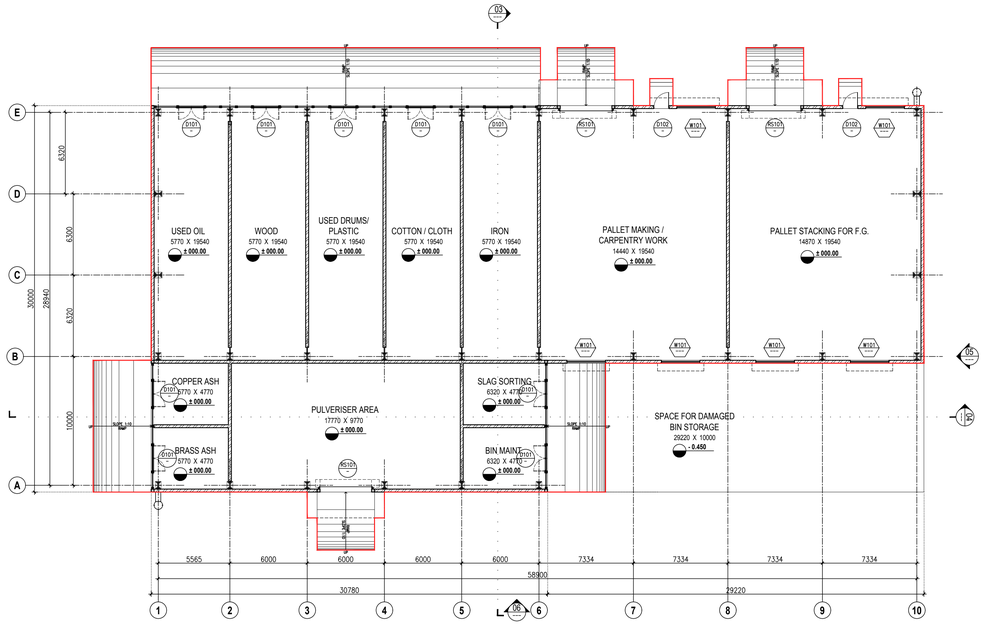

01 GROUND FLOOR PLAN
SCALE 1:200

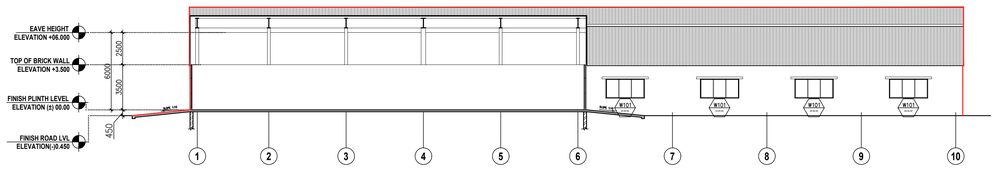

04 SECTION
SCALE 1:200

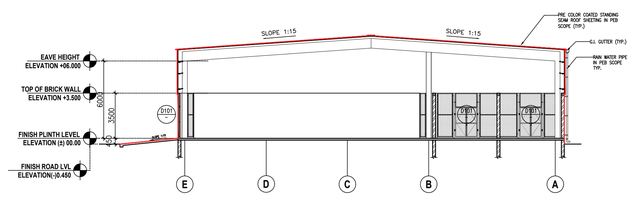

03 SECTION
SCALE 1:200

THIS DRAWING & DESIGN IS THE SOLE PROPERTY OF VMS & SHALL NOT BE COPIED, TRACED OR REPRODUCED BY ANY MEANS WITHOUT PRIOR WRITTEN CONSENT OF THE FIRM.

GENERAL NOTES :

1. ALL THE DIMENSIONS ARE UNFINISHED DIMENSIONS.
2. ALL DIMENSIONS ARE IN MM AND LEVELS ARE IN MT, UNLESS OTHERWISE MENTIONED.
3. ALL THE DIMENSIONS SHALL BE READ & NOT TO BE MEASURED.
4. IN CASE OF ANY DISCREPANCY, BRING IT TO THE NOTICE OF THE ARCHITECT IMMEDIATELY.
5. DETAIL DRAWING PRECEDES THE GENERAL DRAWING

SCHEDULE OF OPENINGS:


MKD.	SIZE	SILL HT.	LINTEL HT.	TOTAL NO.	REMARKS
D101	2050x2400	-----	2400	9	CHAIN LINK DOOR
D102	1200x2400	-----	2400	2	FIRE DOOR
RS101	4000x4500	-----	4500	2	ROLLING SHUTTER
W101	3000x1500	900	2400	06	ALU. FRAME WITH FIXED GLASS & LOUVERS WINDOW

FOR TENDER

NO.	DATE	DESCRIPTION	DRAWN BY	CHECKED BY
R0	-	-	-	-

REVISION HISTORY

KEY PLAN
SCALE : N.T.S.

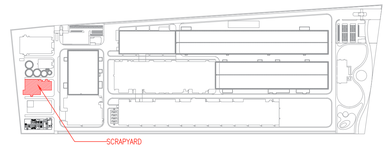

REFERENCE DRAWINGS :

01. ARCHITECTURAL :	-
02. STRUCTURAL :	-
03. HVAC :	-
04. ELECTRICAL :	-
05. UTILITIES :	-

GROUND FLOOR PLAN, SECTIONS & ELEVATIONS

SCRAPYARD

AGRAWAL METAL WORKS(P) LTD.

PROJECT NO.	SCALE :	DRAWN :	BHAKTI B.
3824	AS SHOWN	CHECKED:	BHAKTI B.
	DATE : 03-12-24	APPROVED:	DARSH D.
		COORDINATION CHECKED:	DARSH D.

VMS ENGINEERING & DESIGN SERVICES (P) LTD.
CHITRAKOOT FLATS, B/H TIMES OF INDIA, OFF ASHRAM ROAD,
AHMEDABAD-380 009. PHONE: +91 (079) 2658-8829, 4023-6236
WWW.VMSCONSULTANTS.COM

SHEET SIZE	DRAWING NO.	TENDER	REVISION:
600x 1000	T.A.11.101	T	R0