

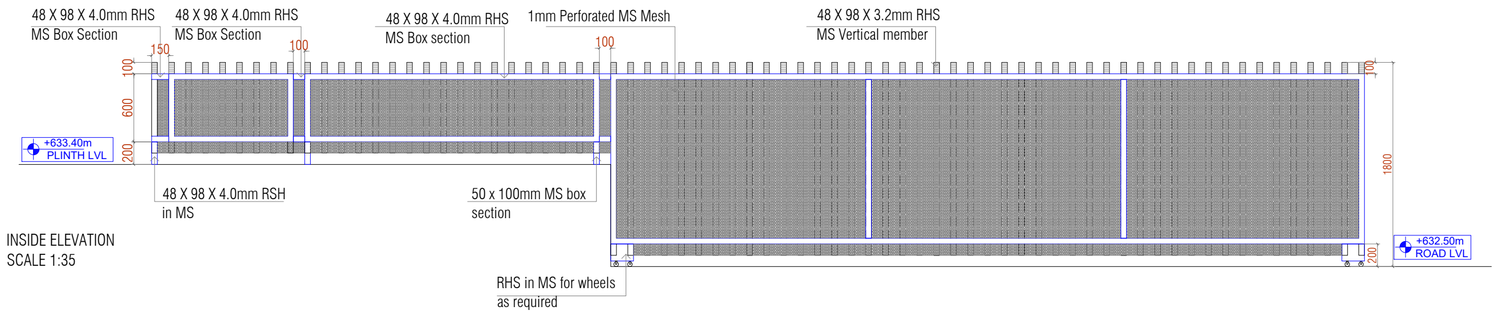



INSIDE ELEVATION
SCALE 1:35

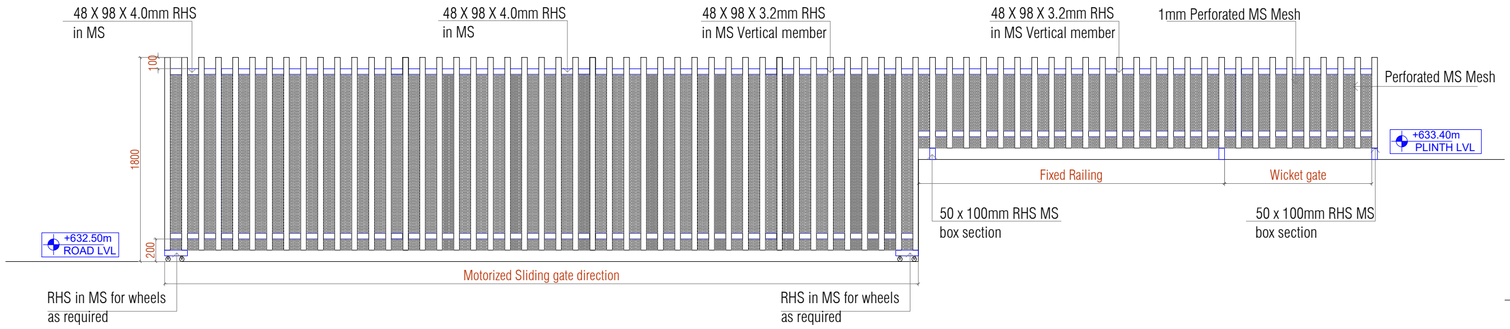


OUTSIDE ELEVATION
SCALE 1:35

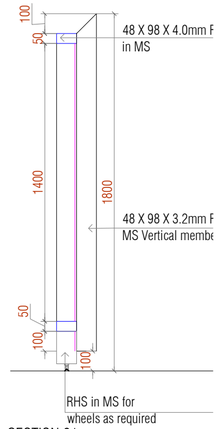


SECTION 01
SCALE 1:20

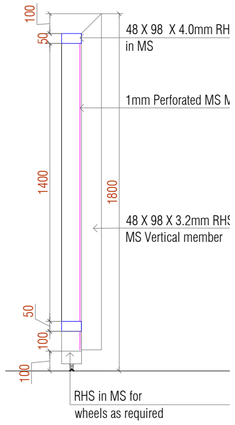


SECTION 02
SCALE 1:20

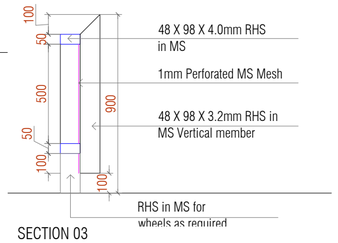


SECTION 03
SCALE 1:20

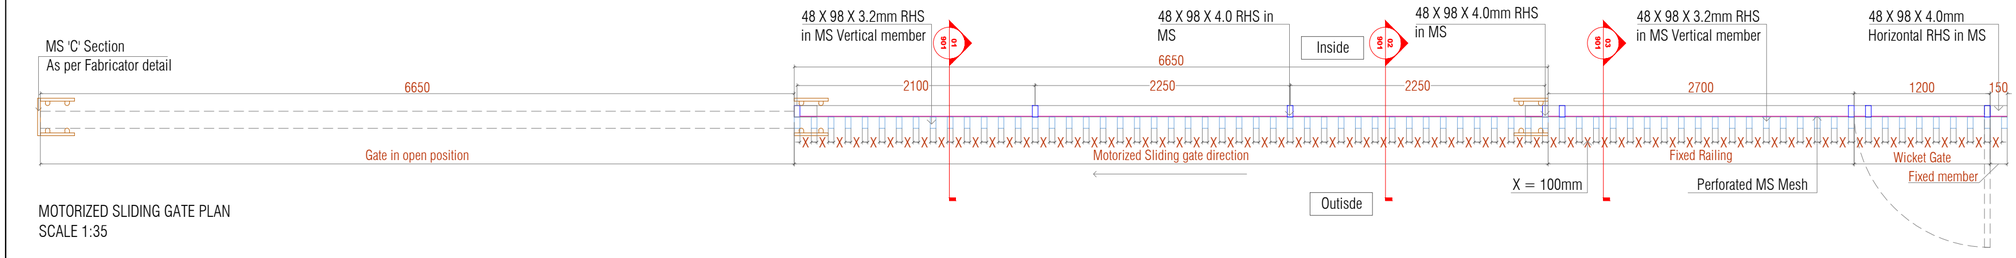

MOTORIZED SLIDING GATE PLAN
SCALE 1:35

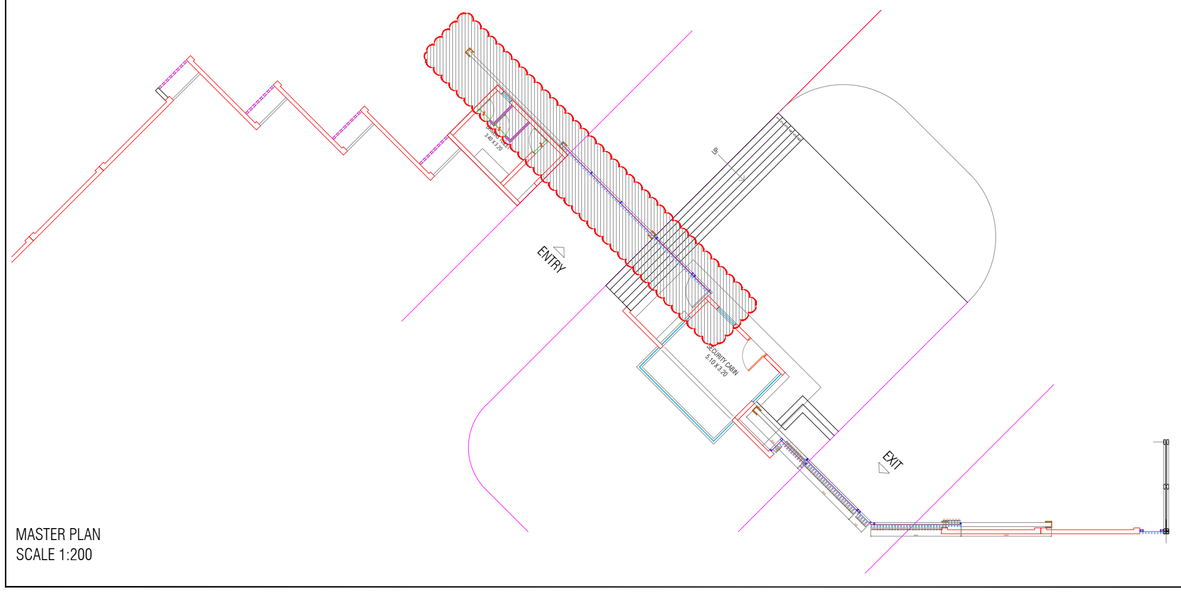

MASTER PLAN
SCALE 1:200

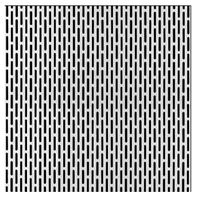




REFERENCE IMAGE OF MS PERFORATED SHEET

NOTE : ALL STANDARD LOCKING SYSTEMS TO BE CONSIDERED

MASTER PLAN- GATE -1

NOTES :

1. ALL DIMENSIONS ARE IN MM UNLESS OTHERWISE MENTIONED
2. ONLY WRITTEN DIMENSIONS SHALL BE FOLLOWED
3. DIMENSIONS SHALL BE CHECKED AND CORRELATED WITH STRUCTURAL DRAWINGS
4. LARGER SCALED DRAWINGS SUPERSEDE SMALLER SCALED DRAWINGS
5. ANY DISCREPANCY IN THE DRAWING SHALL BE IMMEDIATELY BROUGHT TO THE NOTICE OF THE ARCHITECT
6. NO WORK ON SITE SHALL PROCEED WITHOUT THE APPROVAL OF **FOURTH DIMENSION ARCHITECTS PVT. LTD**
7. THIS DRAWING IS THE SOLE PROPERTY OF **FOURTH DIMENSION ARCHITECTS PVT. LTD** AND IS NOT TO BE REPRODUCED OR COPIED IN PART OR WHOLE IN ANY FORM AND ON COMPLETION OF PROJECT SHALL BE RETURNED TO ARCHITECS
8. THIS DRAWING CONTAINS COPYRIGHT MATERIAL AND TRADE SECRET INFORMATION BELONGING TO **FOURTH DIMENSION ARCHITECTS PVT LTD** AND ITS CLIENT AS NOTED ABOVE
9. ANY UNAUTHORIZED USE , DISCLOSURE DISSEMINATION OR DUPLICATION OF ANY OF THE INFORMATION CONTAINED HEREIN MAY RESULT IN LIABILITY UNDER APPLICABLE LAW.

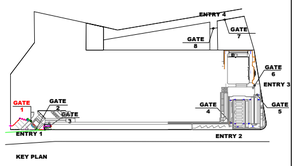

KEY PLAN

NO	REVISION	DATE

LEGEND :

PROJECT :
PROPOSED PLANT FOR WILO MATHER & PLATT Pumps Pvt. Ltd. LIMITED, AT CHORDIA INDUSTRIAL PARK, SHIRWAL, SATARA.

CLIENT :
WILO MATHER & PLATT Pumps Pvt. Ltd.

FOURTH DIMENSION ARCHITECTS PVT. LTD.
FDAPL
ARCHITECTS, PLANNERS, INTERIOR, LANDSCAPE DESIGNERS & LEISURE CONSULTANTS
'FD House', Lane no 8, Opposite Axis Bank,
Prabhat Road, Deccan Gymkhana, Pune-411 004.
Ph. : +91-20-41 000 999, Fax: +91-20-41 000 888

SIGN AND SEAL :

TITLE : GATE 1 AND FIXED RAILING DETAIL AT ENTRY 1

DRAWING STATUS : FOR TENDER

DATE	: 30/11/2021	**NORTH**
SCALE	: As Mentioned	
JOB NO.	: W-IND-0320	
DRAWN BY	: SANSKRUTI S.	
CHECK BY	: KAVITA	

DRAWING NO : SG-A-901

REVISION NO : R0