
Weitergabe sowie Vervielfältigung dieses Dokuments, Verwertung und Mitteilung seines Inhalts sind nur nach vorheriger ausdrücklicher schriftlicher Zustimmung von SMS Meer GmbH gestattet. Das Dokument ist vor unberechtigtem Zugriff Dritter zu schützen. Zuwiderhandlungen verpflichten zu Schadensersatz. Alle Rechte aus Patent-/Gebrauchsmuster-/Markenschutz vorbehalten.

The reproduction, distribution and utilization of this document as well as the disclosure of its content to others without prior explicit written consent of SMS Meer GmbH is prohibited. Holder has to protect this document against unauthorized withdrawal of third parties. Offenders will be held liable for the payment of damages. All rights reserved in case of patent/utility model/trademark protection.

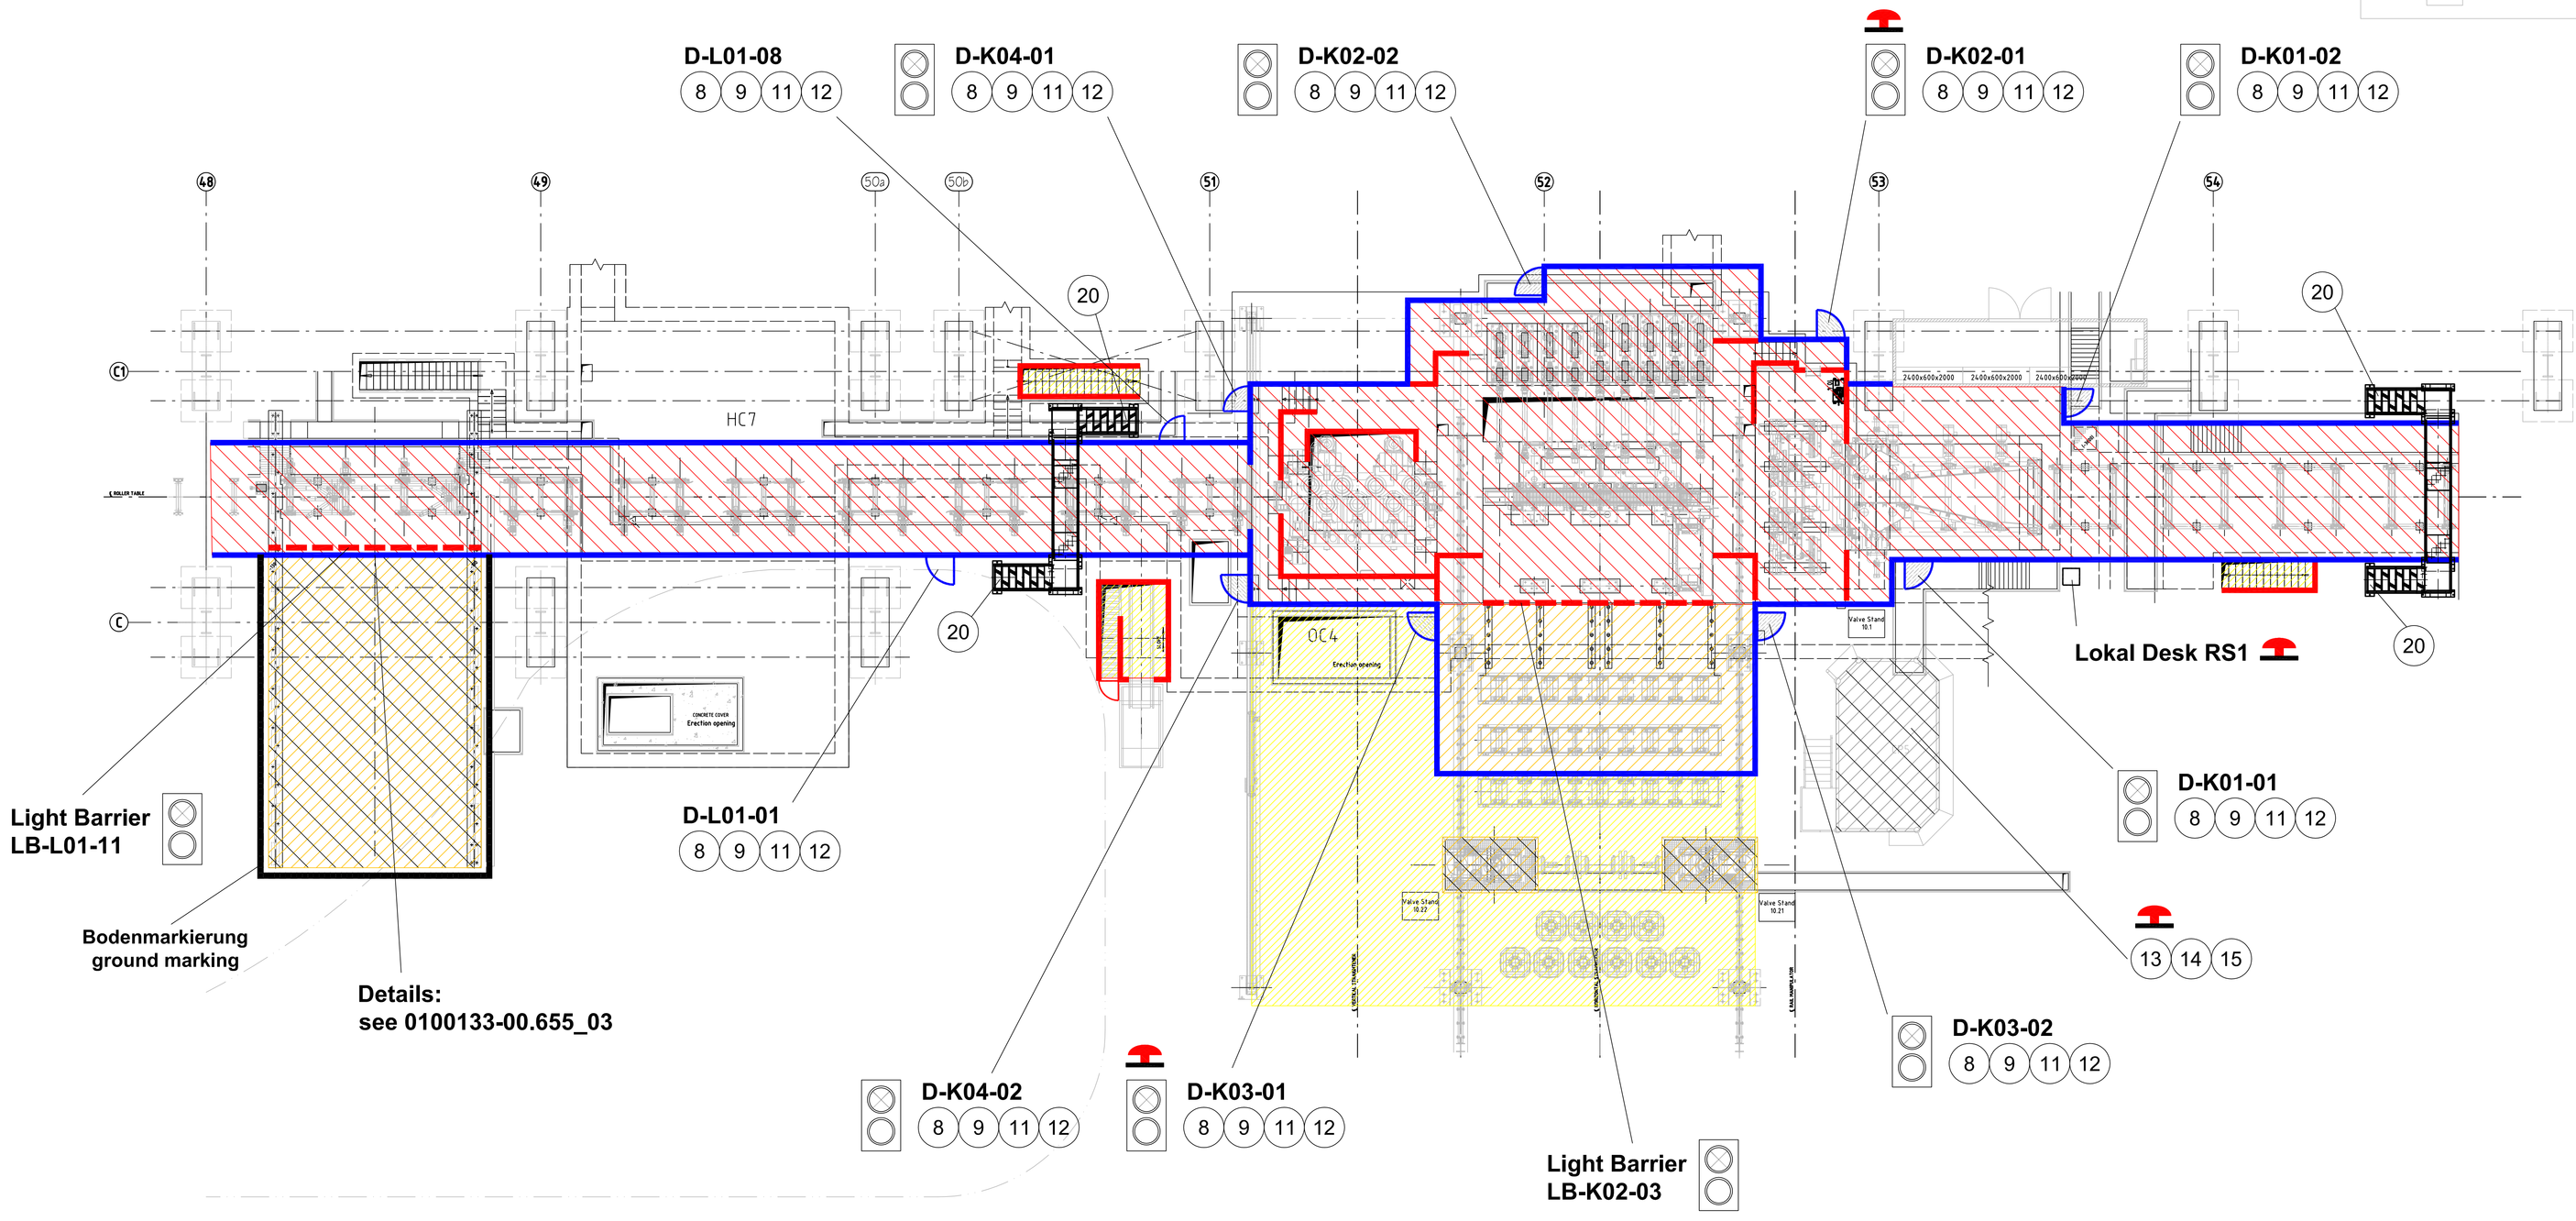

GATE

GATE WITH MECH. LOCKING DEVICE

GATE WITH ELECT. LOCKING DEVICE

DOOR WITH MECH. LOCKING DEVICE

DOOR WITH ELECT. LOCKING DEVICE

DOOR

DOOR WITH MECH. LOCKING DEVICE

DOOR WITH ELECT. LOCKING DEVICE

DANGER ZONE 1
No access while unit is in operation.

DANGER ZONE 2
Access only to qualified and authorized persons possible
in defined operating states.
High Residual Risks
Note safety instructions in operating and maintenance manual.

DANGER ZONE 3
Access only to qualified and authorized persons possible
in defined operating states.
Low Residual Risks
Note safety instructions in operating and maintenance manual.

DANGER ZONE 4
Permanente working place.
Unrestricted access possible while unit is in operation.
Note general safety instructions.

WORKING PLACE
Part of no access zone, that can be entered by trained operators
under particular conditions only
Note safety instructions in operating and maintenance manual.

REQUEST-/ ACKNOWLEDGEMENT BUTTON

EMERGENCY STOP

ACKNOWLEDGEMENT BUTTON

ESCAPE ROUTES

RAILING

REMOVABLE RAILING

FENCE

REMOVABLE FENCE

REMOVABLE CHAIN

LIGHT CURTAIN

9463.0000 / RAILBHIL

CATEGORY OF DRWG.	APPROVAL	INFORMATION	REFERENCE	RECORD	CONSTRUCTION

BHILAI STEEL PLANT, BHILAI, CHATTISGARH
7,0 MTPA EXPANSION

मेकॉन लिमिटेड
MECON LIMITED

VENSDOR'S NAME: SMS Meer/SMS Meer India/ABB
PACKAGE DESCRIPTION: UNIVERSAL RAIL MILL (Pkg No-047)
TITLE OF DRAWING. PARTITION 7,8 SAFETY LAYOUT
SCALE-
VENDOR'S DRG NO.-
PROJECT DRG. NO. BSP-SMS Meer-08-047-21-130-35-BE-06655 REV. –

Fertigungsvorschriften / Manufacturing Instructions: SN 200
Ursprung / Origin
Fertiggewicht / Finished weight
Modell-Nr. / Pattern-No.
Werkstoff / Material
kg
Projektionsmethode 1 / First angle projection method ISO 128

	Datum / Date	Name
Bearb. / Drawn	27.09.11	Pryen
Geprüft / Checked	27.09.11	Prätzel
Norm-Stand		

Typ / Type: Safety Layout
Benennung / Title: Teilbereich, 7,8 — PARTITION 7,8
Maßstab / Scale: 1:100
Sach-Nr. / Drawing-No.: 0100133-00.655
Blatt / Sheet 1 von / Sheets 3
Ersatz für / Supersedes:
Ersetzt durch / Superseded by:

SMS MEER — SMS group

Ausgabe / Issue	Änderung / Revision	Datum / Date	Name

Diese Zeichnung und alle darauf enthaltenen Informationen sind vertraulich. This drawing and all information on it is confidential.

A0