


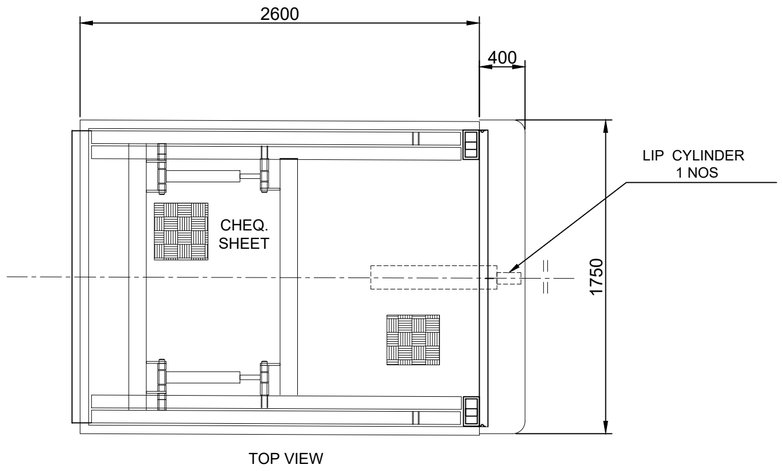


TOP VIEW

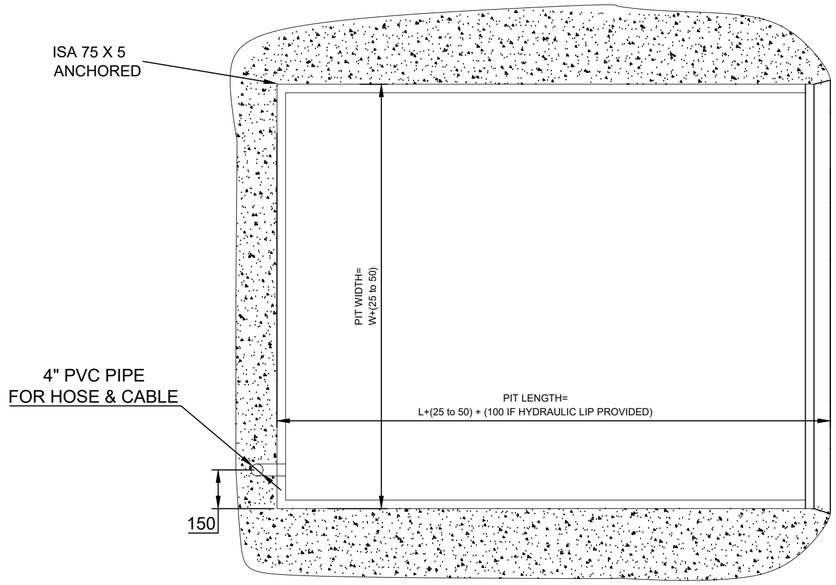


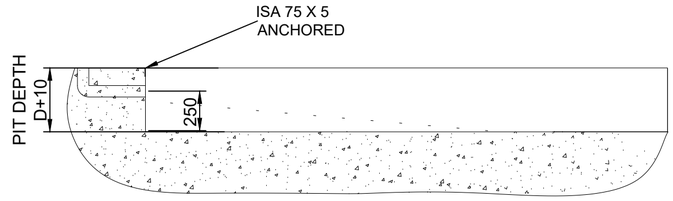

PIT DRAWING

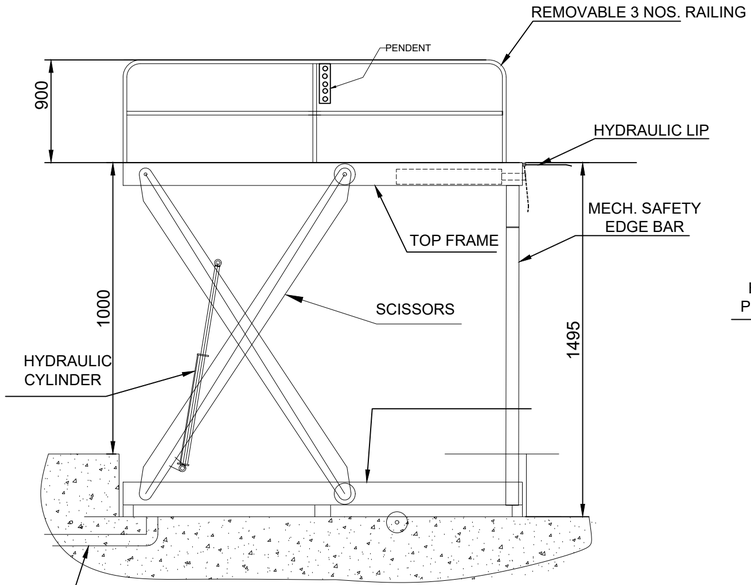

OPEN HEIGHT FRONT VIEW

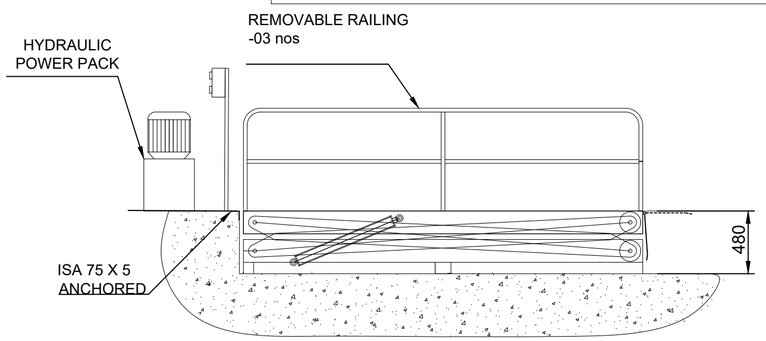

CLOSED HEIGHT FRONT VIEW

SAFETY RAILING	900 MM HT
POWER PACK	01 NO
MAX HT	1480MM
LIFT HT	1000 MM
SHUT HT	480MM
PLATFORM SIZE	2600W x 1750L
CAPACITY	3 TON
PIT LENGTH	2800 MM
PIT WIDTH	1860 MM
SHUT DEPTH	495 MM
MOTOR	5 HP, 3 PH

NOTE
1. ALL DIMENSION ARE IN MM.
2. TOLERANCE ± 10 MM.
3. THIS IS A CONCEPTUAL DRAWING ONLY FOR THE REFERENCE PURPOSE.
4. PIT FOR SCISSORLIFT HAS TO BE DIAGONALLY WITHIN 3-5 MM
5. BASE OF THE PIT HAS TO BE IN WATER LEVEL AND RIGHT ANGLE TO THE VERTICAL SIDE WALLS
6. PROPER ARRANGEMENT FOR ROUTING HOSES AND CABLES HAVE TO BE MADE DEPENDING ON SITE CONDITIONS AND POSITION OF POWER PACK
7. COVERING REQUIRED FOR CABLES AND RELATED CIVIL WORK IS IN CLIENTS SCOPE
8. WATER DRAINAGE AND PIT CLEANING NEEDS TO BE CONSIDERED AND DONE BY CLIENT
9. PIT & ALL CIVIL WORK IS IN CLIENT SCOPE.
10. PUSH BUTTON OF SCISSOR LIFT IS IN INCHING MODE.
11.

	Date	Revised By

This drawing & design is the property of NIHVA TECHNOLOGIES. Not to be sold or copied to any other concern.

TITLE:- SCISSOR LIFT

NIHVA TECHNOLOGIES PVT. LTD.

	NAME	DATE	SIGN
DRAWN	MAHESH S.	17/06/2022	
CHECK	MAHESH S.	17/06/2022	
APPRD.			

If any queries contact : design@nihva.com

ALL DIMENSION ARE IN mm

CLIENT - EMCURE PHARMACEUTICALS LTD

LOCATION -

PRODUCT - SCISSOR LIFT

DWG NO:-NIHVA/22-23/CLT/0060

SCALE: NTS