

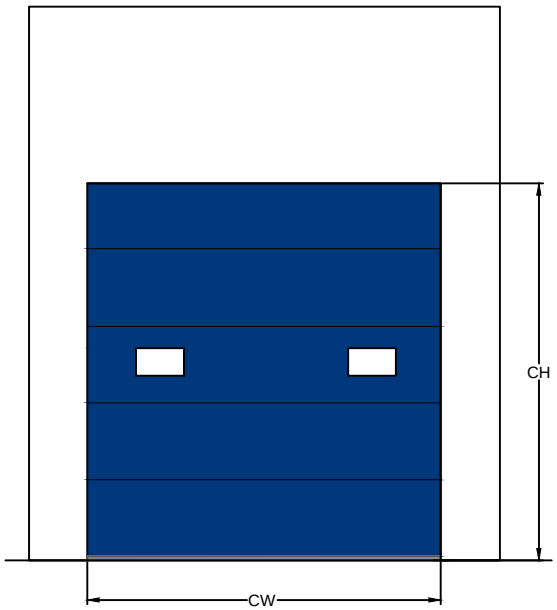


OUTSIDE ELEVATION

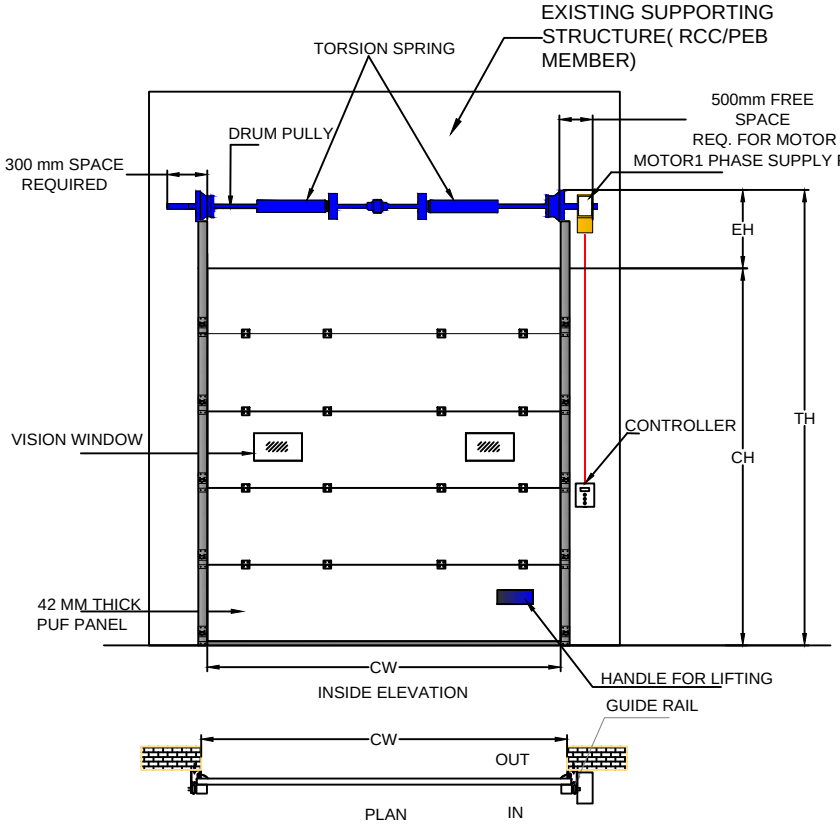


INSIDE ELEVATION

PLAN

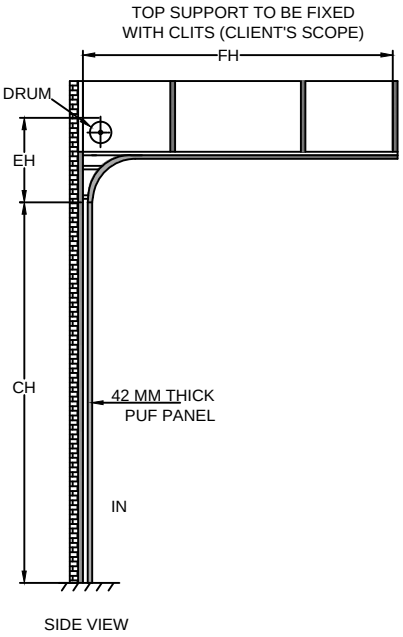

SIDE VIEW

SR NO	CLEAR WIDTH (CW)	CLEAR HEIGHT (CH)	QUANTITY	EH	FH	TH
1	2800	2700	01	600	3400	3400

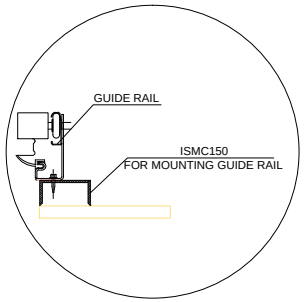

TRACK DETAILS

NOTE- 1. STRUCTURE REQUIRED FOR SECTIONAL DOOR SHALL BE IN CLIENT'S SCOPE.
2.COLOR FOR SECTIONAL DOOR PANEL WOULD BE RAL 5002(Ultramarine blue)

This drawing & design is the property of NIHVA TECHNOLOGIES. Not be sold or copy to any other concern.

TITLE: SECTIONAL DOOR SL (MOTORIZED)

NIHVA TECHNOLOGIES PVT. LTD. PUNE
Tel : 020 66304033
Email:- info@nihva.com
Website:- www.nihva.com

	NAME	SIGN	DATE
DRAWN	SURAJ		29/06/2018
CHECK	PRADEEP		29-06-2018
APPROVAL	R.D		29-06-2018

If any queries contact : design@nihva.com

ALL DIMENSION ARE IN mm

CLIENT - MASTPRO CONSULTING ENGINEERS PVT. LTD.
PROJECT - MANI PROJECT
SITE - PUNE
DWG. NO. : NIHVA/18-19/0074
SCALE: NTS | WT: | SHEET: 01 OF 01