



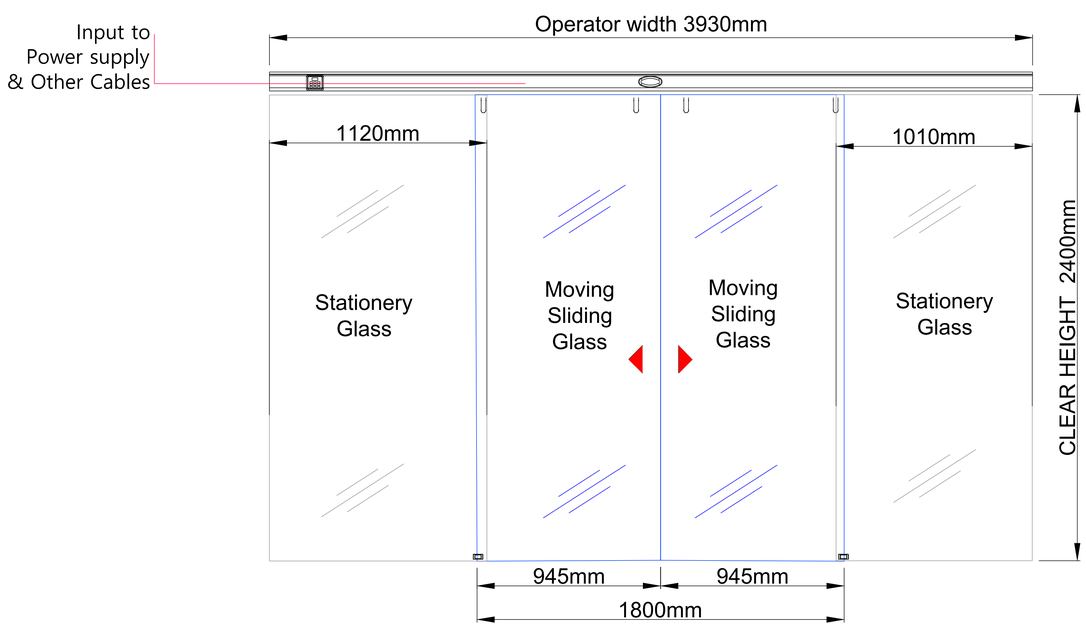

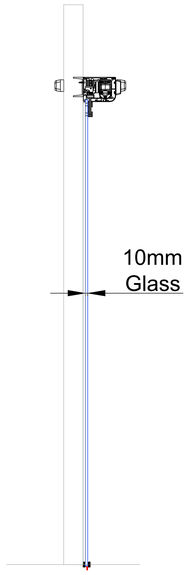

Elevational View A

This drawing & design is the property of NIHVA TECHNOLOGIES. Not to be sold or copied to any other concern.

TITLE:- AUTOMATIC
BI- PARTING GLASS DOOR

NIHVA TECHNOLOGIES PVT. LTD.

NIHVA TECHNOLOGIES
PVT. LTD. PUNE
Tel : 020 66304033
Email:- info@nihva.com
Website:- www.nihva.com

	NAME	DATE	SIGN
DRAWN	SUMIT.J	04-11-2023	
CHECK			
APPRD.			

CLIENT - TATA MOTORS
LOCATION - Pune
PRODUCT - GLASS DOOR
If any queries contact : design@nihva.com
DWG NO:- NIHVA/23-24/CLT/005 REV- 02
ALL DIMENSION ARE IN mm
SCALE: NTS SHEET: 01 OF 01

Rev No.	Revision	Date	Revised By	Qty
				01