




ELEVATION

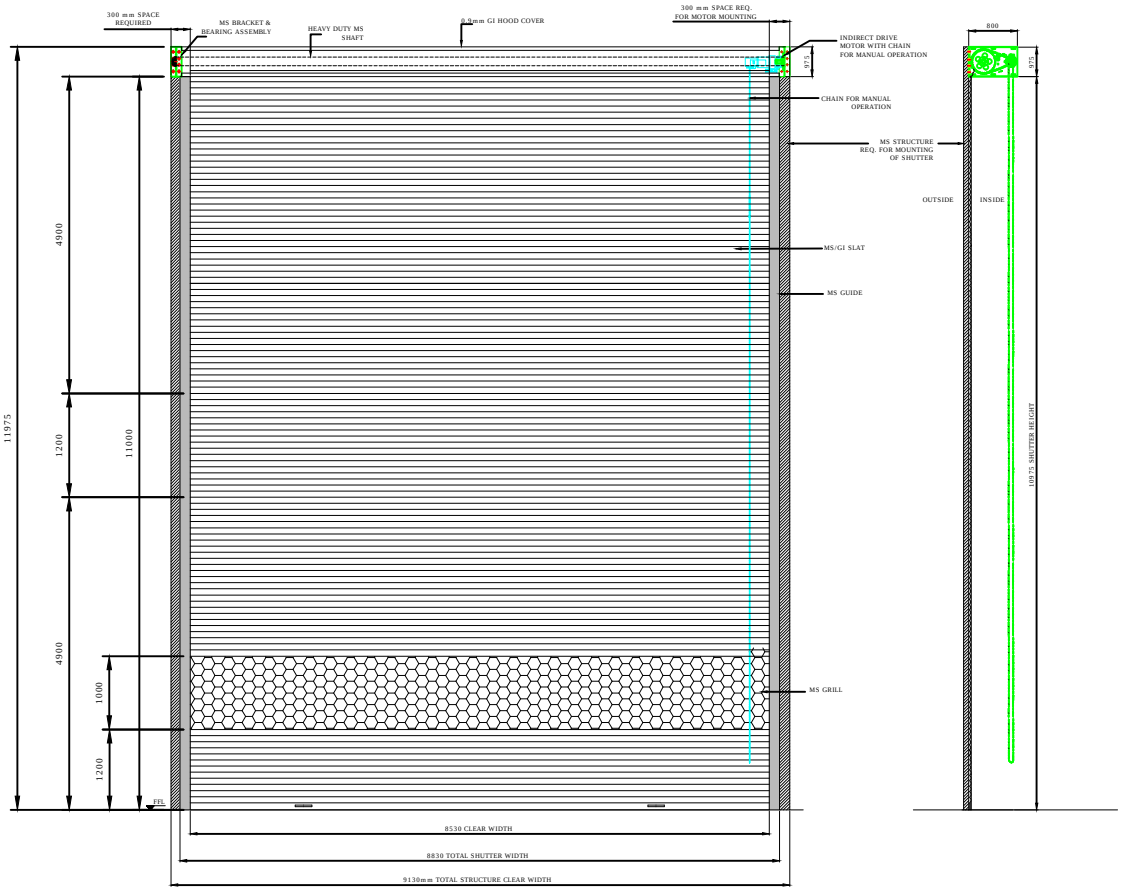


PLAN

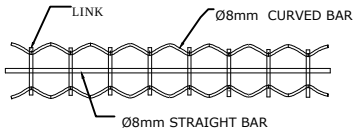


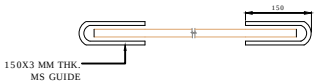

Single Wall Rolling Shutter

Main Slats

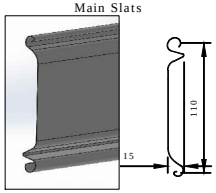

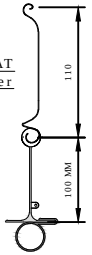

1.2mm Thk.FLAT Type MS Shutter lath AT TOP & BOTTOM

M.S. BOTTOM RAIL PROFILE 2.5MM THK WITH ANGLE STIFFNER & EPDM RUBBER

R02:-SIZE CHANGED
R01:-SIZE CHANGED

CLEAR WIDTH	CLEAR HEIGHT	QUANTITY
8530	11000	1

DIMENSION :

CLEAR WIDTH	CLEAR HEIGHT	QUANTITY
8530	11000	1

MATERIAL :

THICKNESS :

NOTE-
1).ONE COAT OF RED OXIDE WILL BE GIVEN SHUTTER (ONLY MS PART).
2). HOOD COVER WILL BE IN GI.
3).3 PHASE SUPPLY SHOULD BE GIVEN TO THE SHUTTER.
4). REQUIRED STRUCTURE FOR SHUTTER SHALL BE IN CLIENT'S SCOPE.
5). ALL CIVIL WORK WILL BE IN CLIENT'S SCOPE.
6). TOLERANCE FOR GRILL SIZE SHALL BE PLUS/MINUS 15mm

NIHVA TECHNOLOGIES PVT. LTD. PUNE
Email:- info@nihva.com
Website:- www.nihva.com

TITLE:

MOTORIZED ROLLING SHUTTER

CLIENT'S APPROVAL :

CLIENT - JLL

PROJECT - INORBIT MALL

SITE LOCATION -WADGAONSHERI,PUNE

DWG. NO. :NIHVA/17-18/0144/R02

SCALE: NTS	WT:	SHEET:1 OF 1

DRAWN BY: SURAJ	DATE: 25-10-2017
CHECK : SHEKHAR	DATE: 25-10-2017
APPROVED : SHEKHAR	DATE: 25-10-2017

If any queries contact : projects@nihva.com

NOTE: ALL DIMENSIONS ARE IN mm

THIS DRAWING & DESIGN IS THE PROPERTY OF NIHVA TECHNOLOGIES. NOT TO BE SOLD OR COPY TO ANY OTHER CONCERN.