



DRAWING

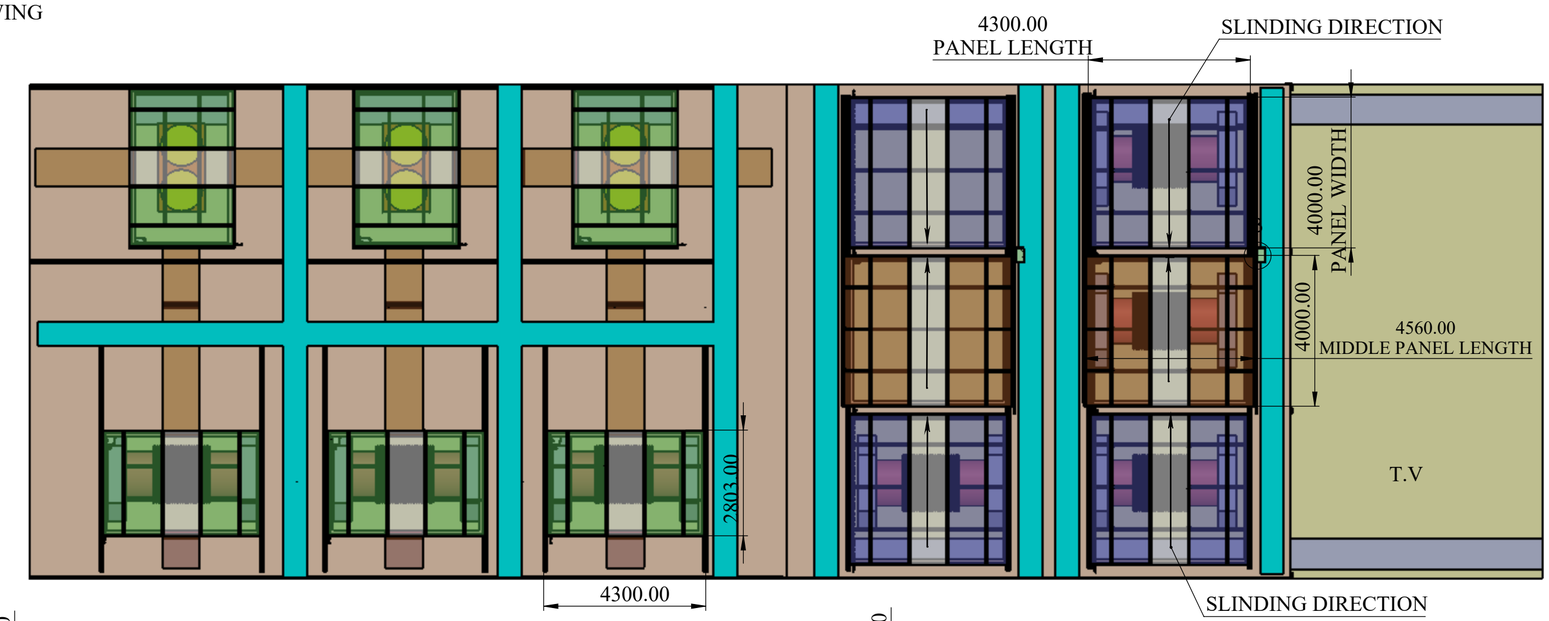

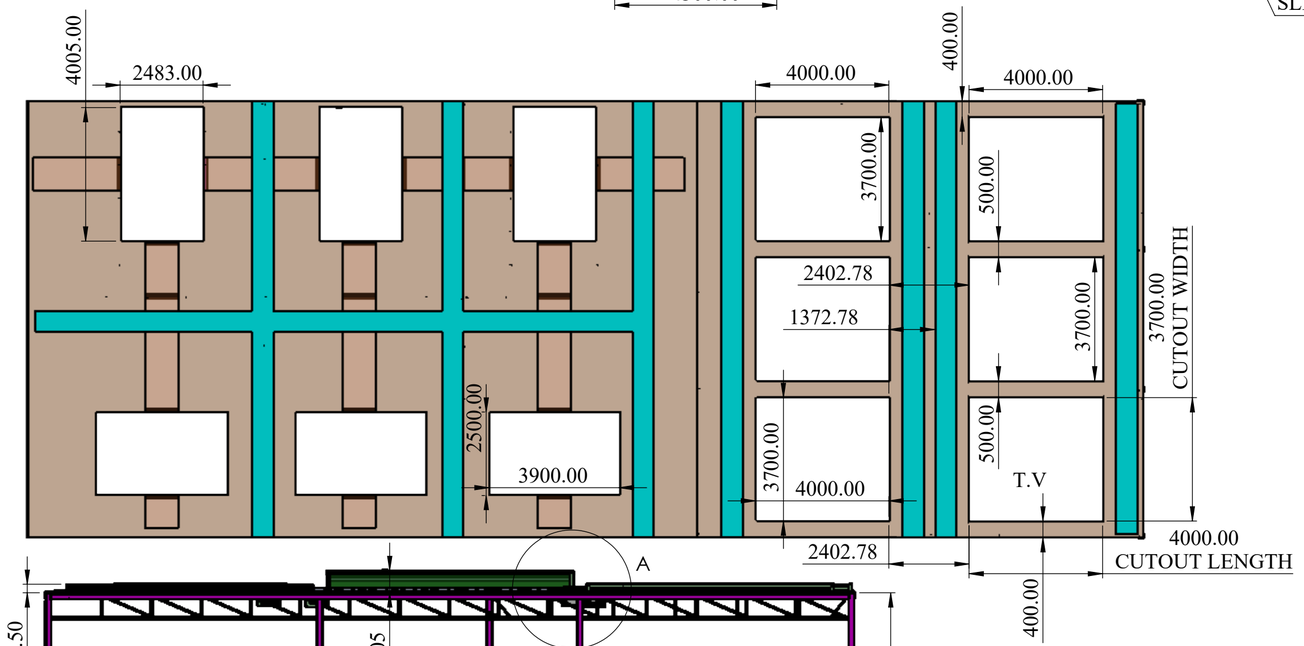

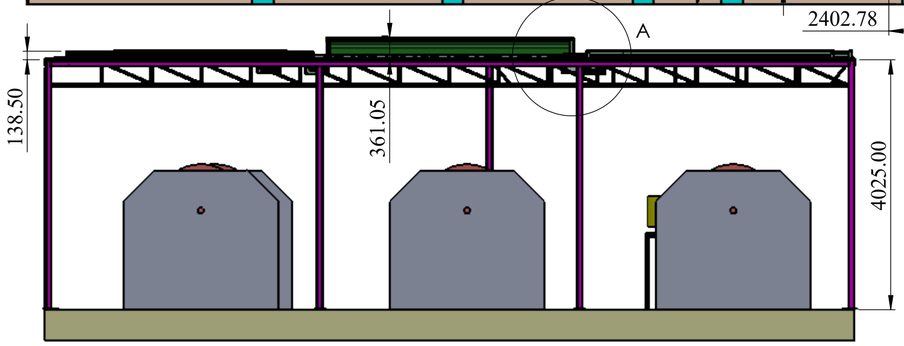


F.V

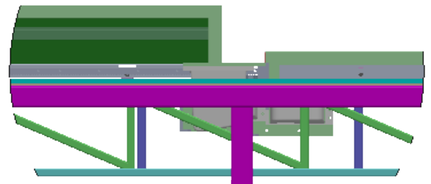

DETAIL A
SCALE 1 : 20

MOTOR SHAFT + PINION

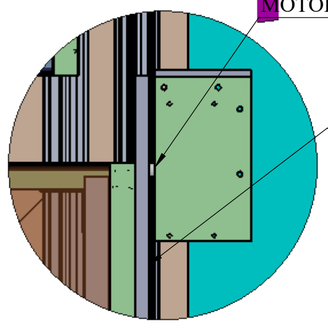

RACK MOUNTING
OUTSIDE THE PANEL

DETAIL B
SCALE 1 : 10

MIDDLE PANEL MOTOR &
RACK ARRANGMRNT

REV DESCRIPTION	DATE	REV NO
03. AIR TIGHTENING & DUST PROOF RUBBERIS ADDED	00-00-2025	REV 03
04. PANEL MODIFICATION	10-07-2025	REV 04
05. SAME UNIT ANTHOER THREE PANEL MODIFICATION	15-07-2025	REV 05

NOTE :

SPECIAL INSTRUCTION'S :

TITLE - ROOF AUTOMATION

DWG NO - NTPL-244-PM-001-00-00-00


NIHVA TECHNOLOGIES PVT.LTD.PUNE
Website - www.nihva.com


	NAME	SIGNATURE	DATE
DRAWN	V.W.		14-07-2025
CHK'D	S.W.		15-07-2025
APPV'D	V.T.		15-07-2025

PRODUCT - RETRACTABLE ROOF
PROJECT NO - NTPL-244-PM
REVISION - 05
SITE LOCATION -AHMADABAD
WEIGHT -
MATRIAL -
QTY - 1
If any queries contact - design.nihva@gmail.com
ALL DIMENSION ARE IN mm
A2
PROJECTION METHOD:
SCALE :
SHEET 1 OF 16

DRAWING

REV DESCRIPTION	DATE	REV NO
	15-07-2025	REV 05
1.		

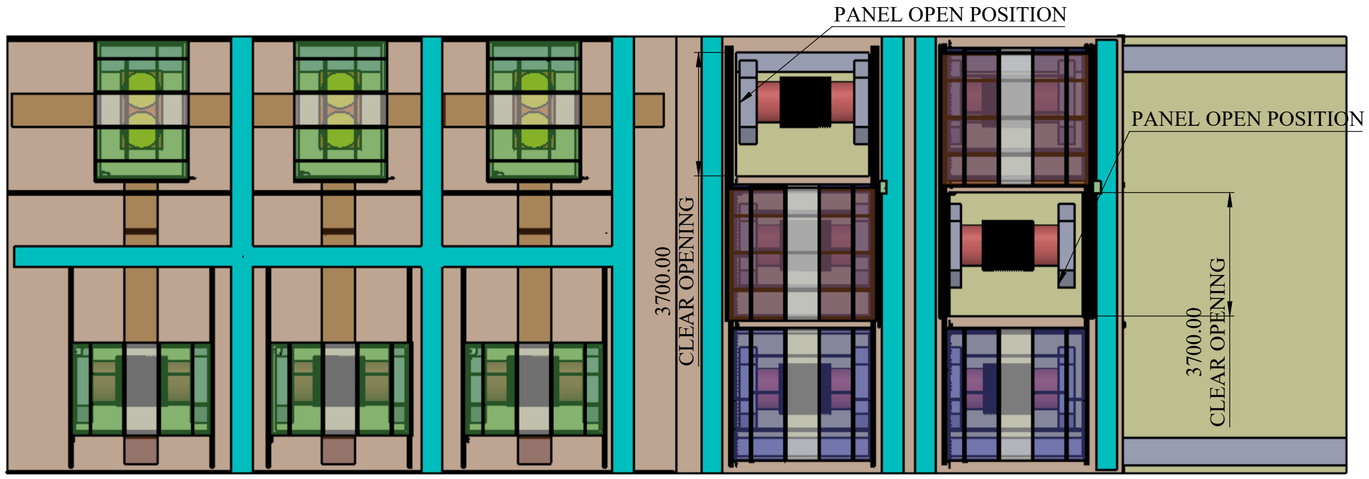

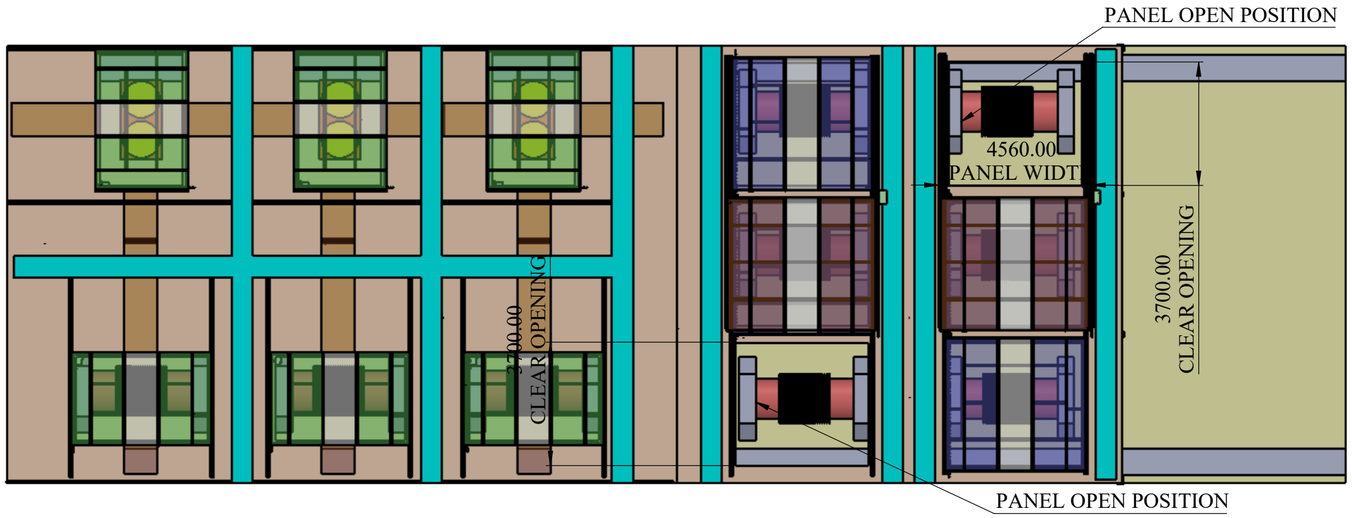

NOTE :

SPECIAL INSTRUCTION'S :

TITLE - ROOF AUTOMATION

DWG NO - NTPL-244-PM-001-00-00-00

NIHVA TECHNOLOGIES PVT.LTD.PUNE
Website - www.nihva.com

	NAME	SIGNATURE	DATE
DRAWN	V.W.		14-07-2025
CHK'D	S.W.		15-07-2025
APPV'D	V.T.		15-07-2025

PRODUCT - RETRACTABLE ROOF

PROJECT NO - NTPL-244-PM | REVISION - 05

SITE LOCATION - | WEIGHT -

MATRIAL - | QTY - 1

If any queries contact - design.nihva@gmail.com


ALL DIMENSION ARE IN mm | A2

PROJECTION METHOD:

SCALE :

DRAWING

REV DESCRIPTION	DATE	REV NO
	04-07-2025	REV 00
REV_05_A : DIMENSION MENTIONED FROM STRUSS MEMBER	21-07-2025	REV_05_A

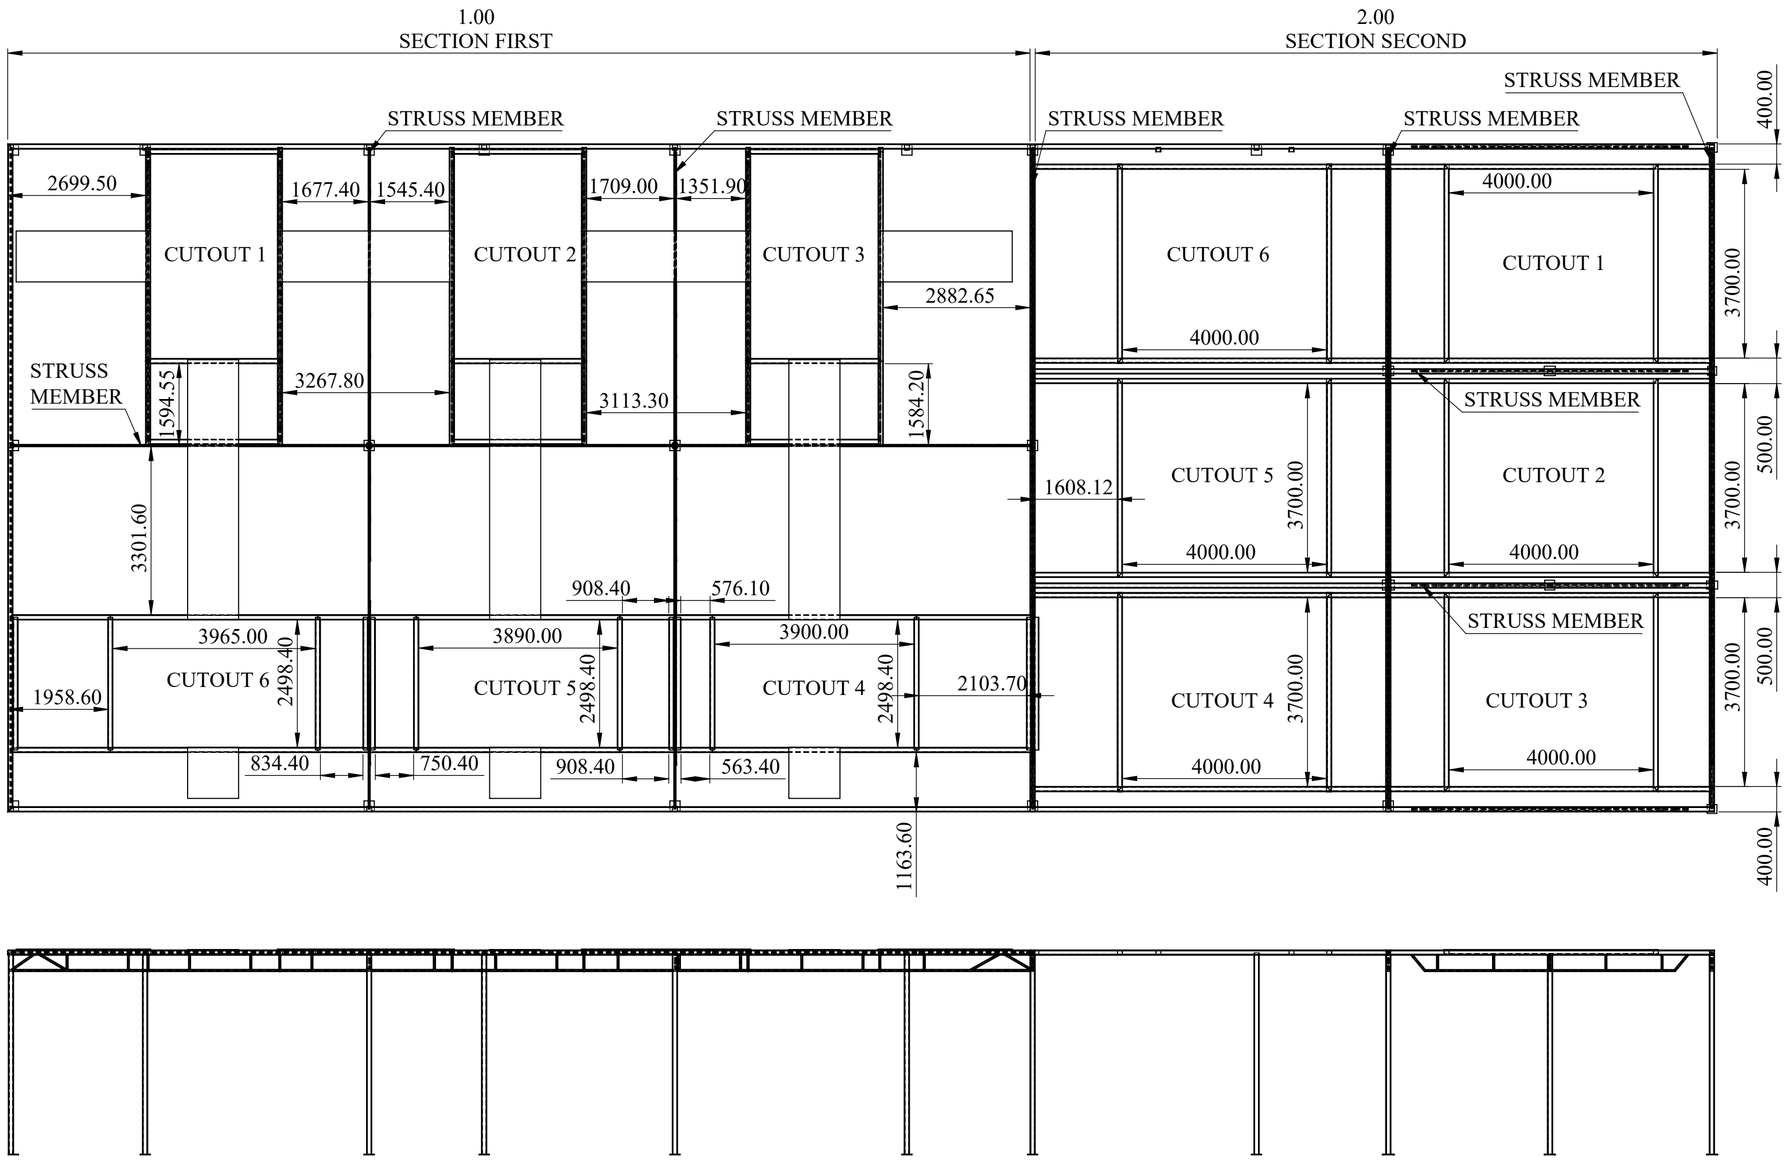



NOTE :

SPECIAL INSTRUCTION'S :


TITLE - ROOF AUTOMATION				NIHVA TECHNOLOGIES PVT.LTD.PUNE Website - www.nihva.com	
DWG NO - NTPL-244-PM-001-00-00-00					
	NAME	SIGNATURE	DATE	PRODUCT - RETRACTABLE ROOF	
DRAWN	V.W.		21-07-2025	PROJECT NO - NTPL-000-PM	REVISION - 05 A
CHK'D	S.W.		22-07-2025	SITE LOCATION -	WEIGHT -
APPV'D	V.T.		22-07-2025	MATRIAL -	QTY - 1
If any queries contact - design.nihva@gmail.com				PROJECTION METHOD:	SCALE :
ALL DIMENSION ARE IN mm			A2		SHEET 3 OF 16

DRAWING

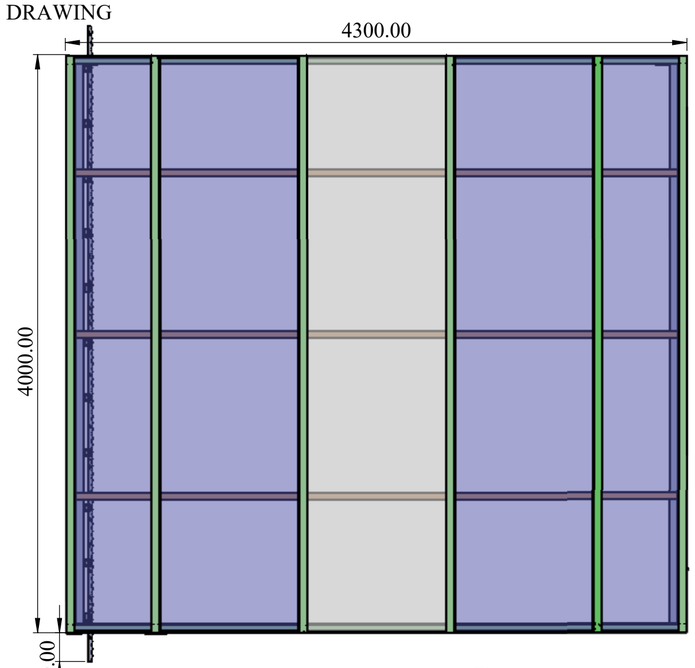


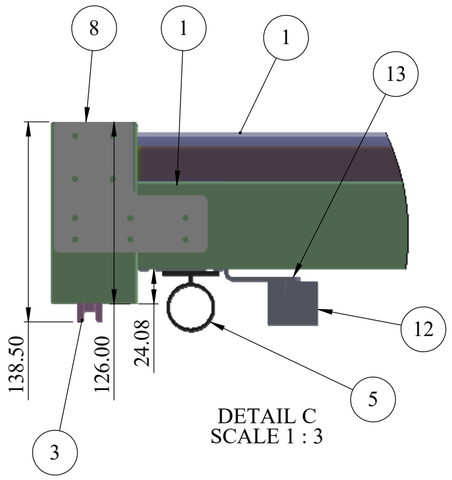



DETAIL C
SCALE 1 : 3

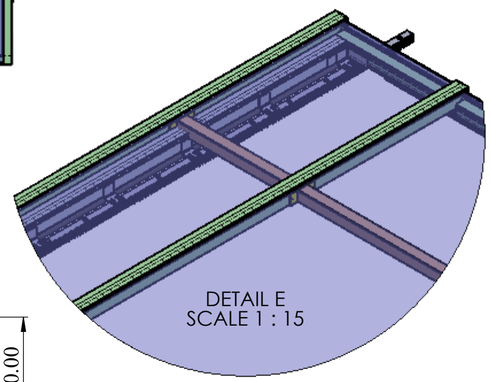

DETAIL E
SCALE 1 : 15

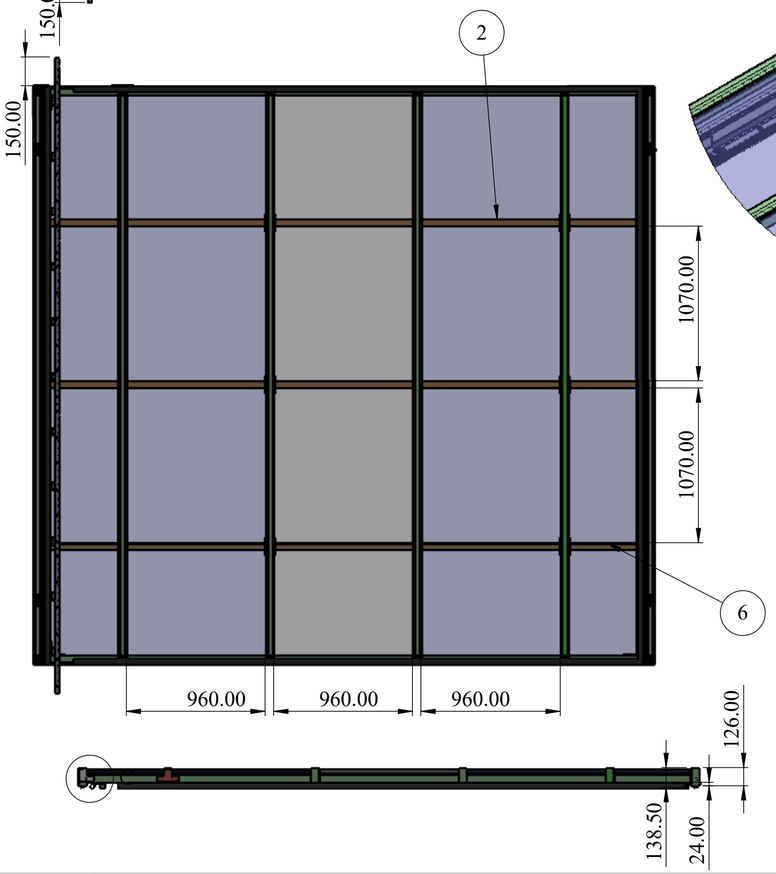

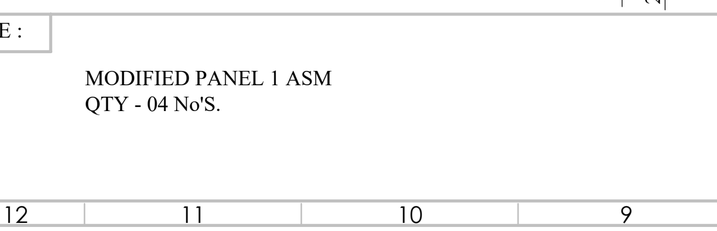

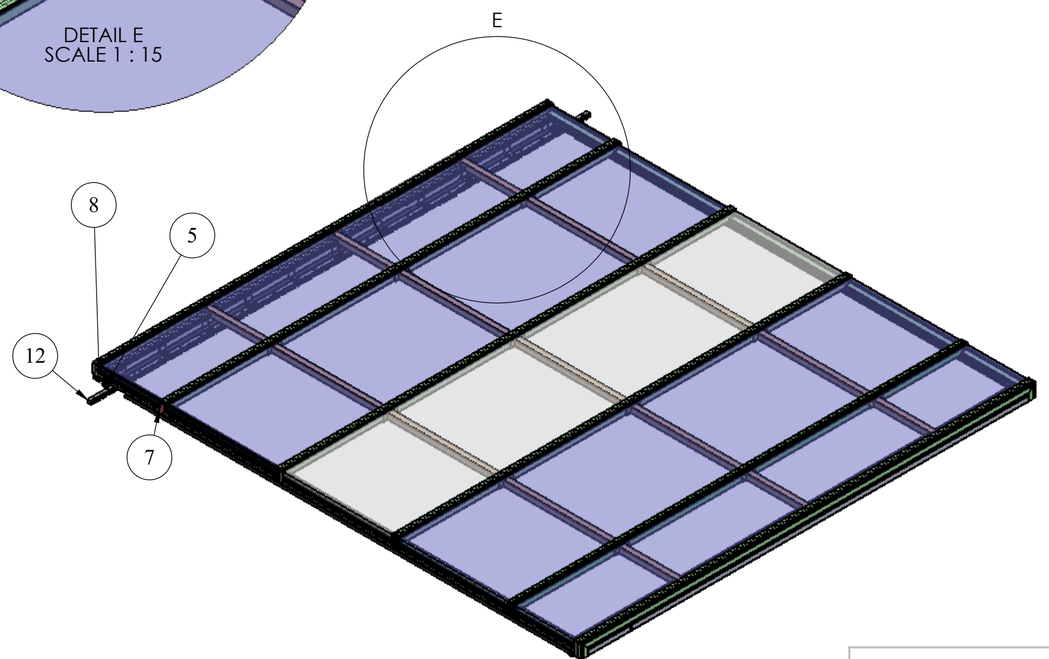

ITEM NO.	PART NUMBER	DESCRIPTION	QTY.
1	.Rev_02_paneel modify-03		1
2	.Rev_02_panel modifiy-03 intermediate support assembly		9
3	.Rev_02_SS WHEEL	SS WHEEL ∅65X18	4
4	NP-PROF01	MS50X50X4T	2
5	NP-PROF01	MS50X50X4T	2
6	.Rev_02_panel modifiy-02 intermediate support assembly		6
7	T PLATE	156X91X3 MM THK	1
8	L PLATE	91X106X3 MM THK	1
9	.Rev_02_AL INSIDE CORNER WELD PLATE	196X40X3 MM THK	4
10	C-MSBL12-35.SLDASM	SHOULDER BOLT	1
11	.rev0202RACK		4
12	RACK CUT 200MM L		1
13	RACK SUPPORT PLATE		12

REV DESCRIPTION	DATE	REV NO
	16-07-2025	REV 05
1.		

NOTE :

MODIFIED PANEL 1 ASM
QTY - 04 No'S.

SPECIAL INSTRUCTION'S :

TITLE - ROOF AUTOMATION

DWG NO - NTPL-244-PM-001-00-00-00

NIHVA TECHNOLOGIES PVT.LTD.PUNE
Website - www.nihva.com

	NAME	SIGNATURE	DATE
DRAWN	V.W.		16-07-2025
CHK'D	S.W.		18-07-2025
APPV'D	V.T.		18-07-2025


PRODUCT - RETRACTABLE ROOF
PROJECT NO - NTPL-244-PM
REVISION - 05
SITE LOCATION -
WEIGHT -
MATRIAL -
QTY - 04
SCALE :
SHEET 4 OF 16


If any queries contact - design.nihva@gmail.com
ALL DIMENSION ARE IN mm
A2
PROJECTION METHOD:

DRAWING


ITEM NO.	PART NUMBER	DESCRIPTION	QTY.
1	.Rev_02_paneel modify-03		4

REV DESCRIPTION	DATE	REV NO
	16-07-2025	REV 05
1.		

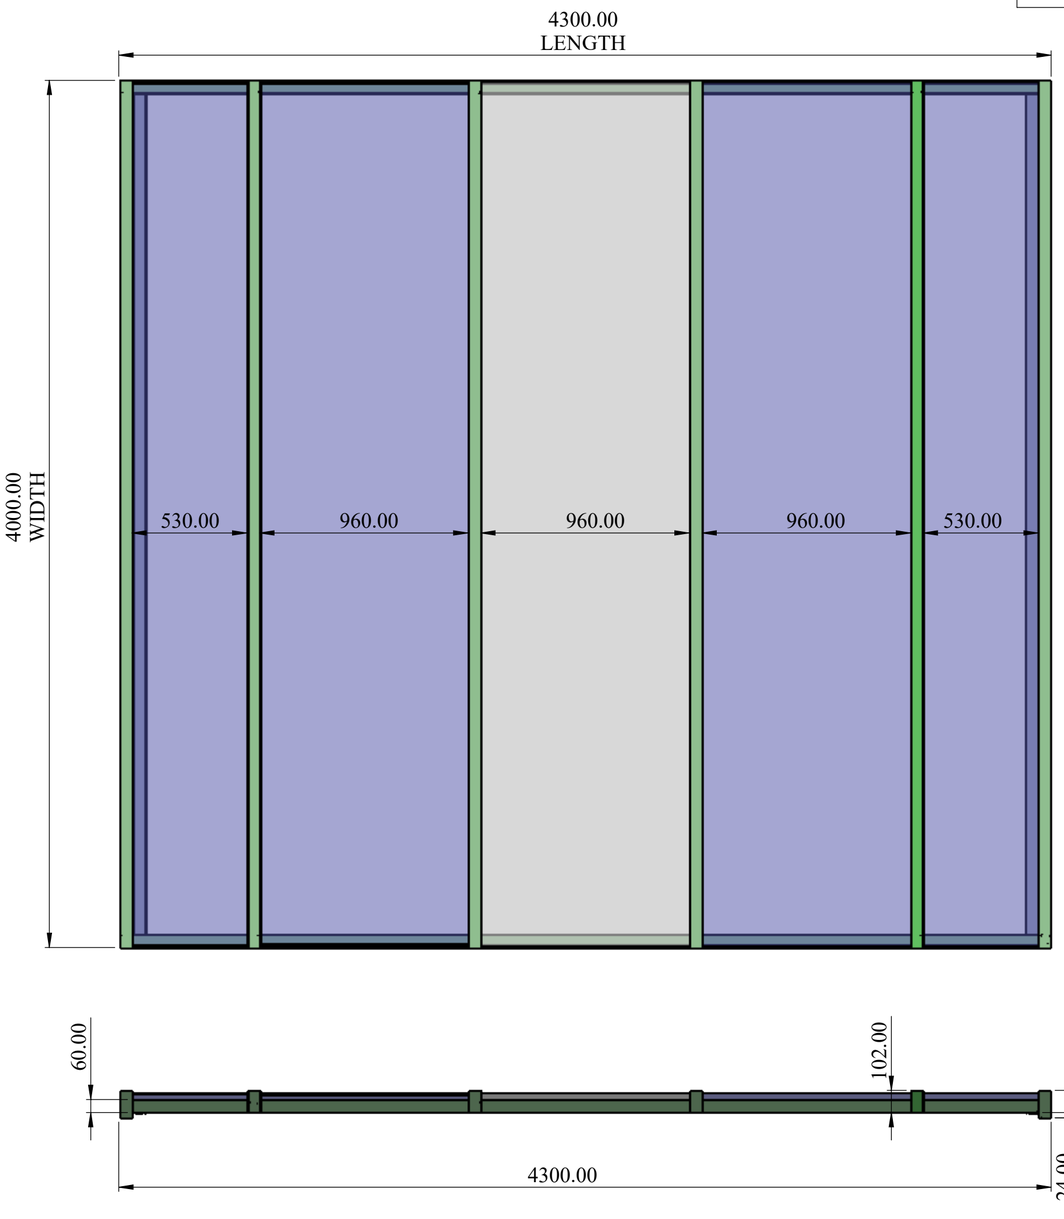

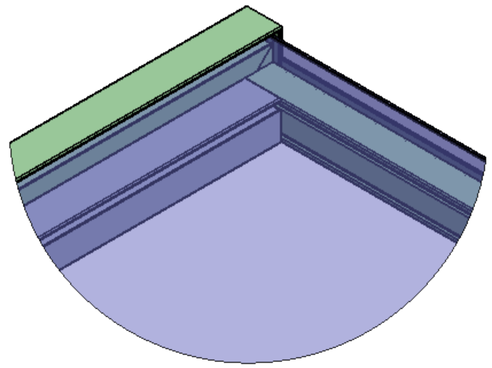

DETAIL F
SCALE 1 : 5

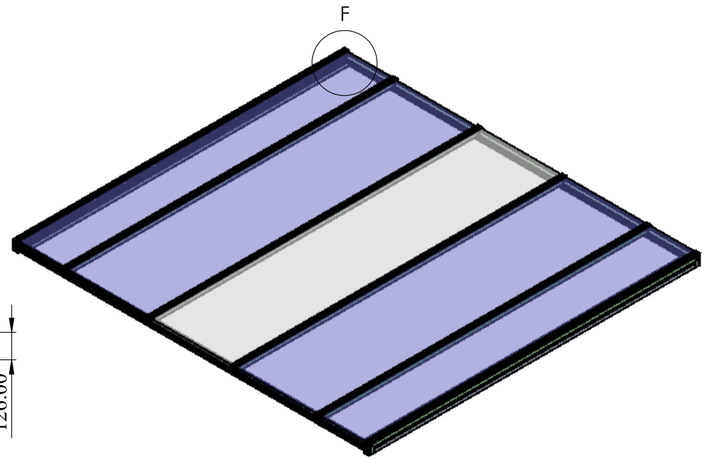

NOTE :

MODIFIED PANEL
ALL PROFILE IN AL GNT-006
QTY - 04 No'S.

SPECIAL INSTRUCTION'S :

ALL PROFILE IN AL GNT 006

TITLE - ROOF AUTOMATION

DWG NO - NTPL-244-PM-001-00-00-00

NIHVA TECHNOLOGIES PVT.LTD.PUNE
Website - www.nihva.com

	NAME	SIGNATURE	DATE
DRAWN	V.W.		16-07-2025
CHK'D	S.W.		18-07-2025
APPV'D	V.T.		18-07-2025


PRODUCT - RETRACTABLE ROOF
PROJECT NO - NTPL-244-PM
REVISION - 05
SITE LOCATION -
WEIGHT -
MATRIAL -
QTY - 04
SCALE :


If any queries contact - design.nihva@gmail.com
ALL DIMENSION ARE IN mm
A2
PROJECTION METHOD:

DRAWING

ITEM NO.	PART NUMBER	DESCRIPTION	QTY.
1	AL PROFILE	SQ - 50X50X1.5 THK	09

REV DESCRIPTION	DATE	REV NO
	16-07-2025	REV 05
1.		

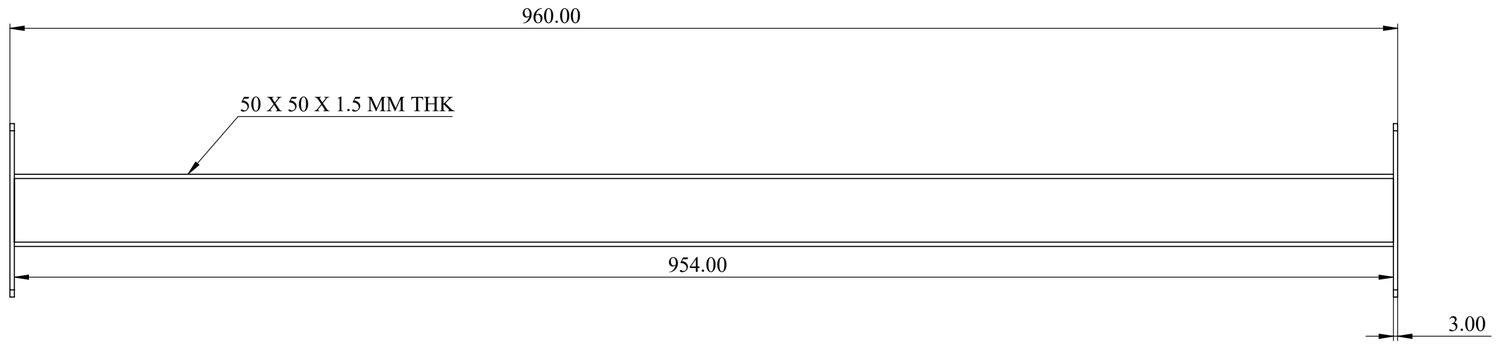

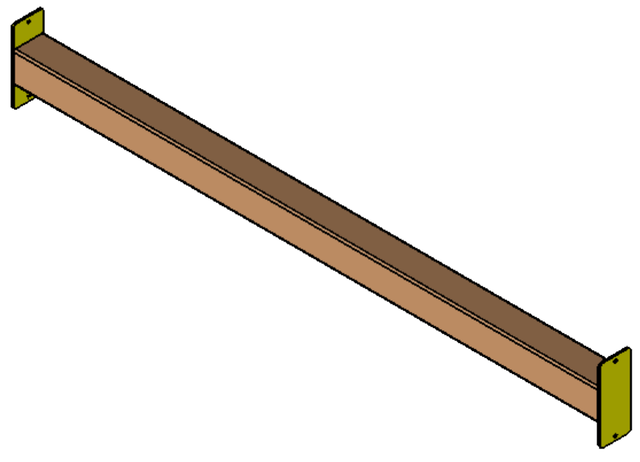

NOTE :

INTERMEDIATE SUPPORT TUBE - 50X50X1.5 MM THK - 960 MM L
ONE PANEL REQ QTY - 9 No'S.
TOTAL REQ - 54 No'S.

SPECIAL INSTRUCTION'S :

MTL - AL

TITLE - ROOF AUTOMATION

DWG NO - NTPL-244-PM-001-00-00-00

NIHVA Technologies Pvt. Ltd.

NIHVA TECHNOLOGIES PVT.LTD.PUNE
Website - www.nihva.com

	NAME	SIGNATURE	DATE
DRAWN	V.W.		16-07-2025
CHK'D	S.W.		18-07-2025
APPV'D	V.T.		18-07-2025

PRODUCT - RETRACTABLE ROOF

PROJECT NO - NTPL-244-PM | REVISION - 05

SITE LOCATION - | WEIGHT -

MATRIAL - | QTY - 1

If any queries contact - design.nihva@gmail.com

PROJECTION METHOD:


SCALE :


ALL DIMENSION ARE IN mm | A2

DRAWING

ITEM NO.	PART NUMBER	DESCRIPTION	QTY.
1	AL PROFILE	REC - 50X50X1.5 THK	06

REV DESCRIPTION	DATE	REV NO
	16-07-2025	REV 05
1.		

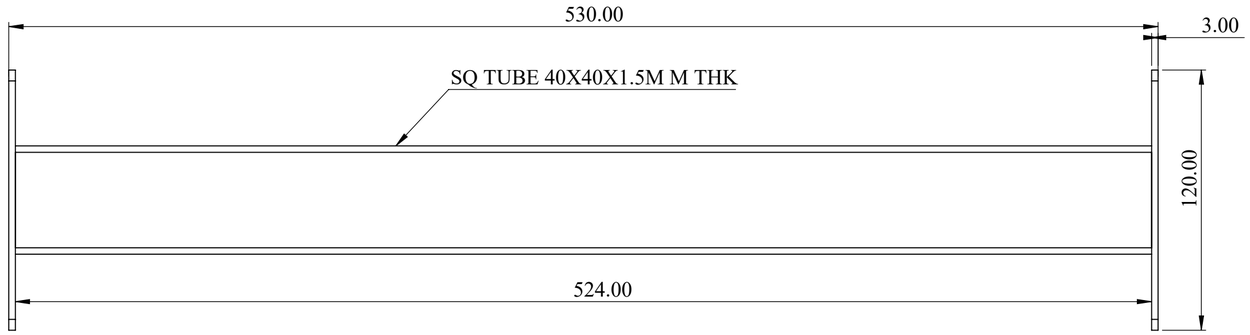

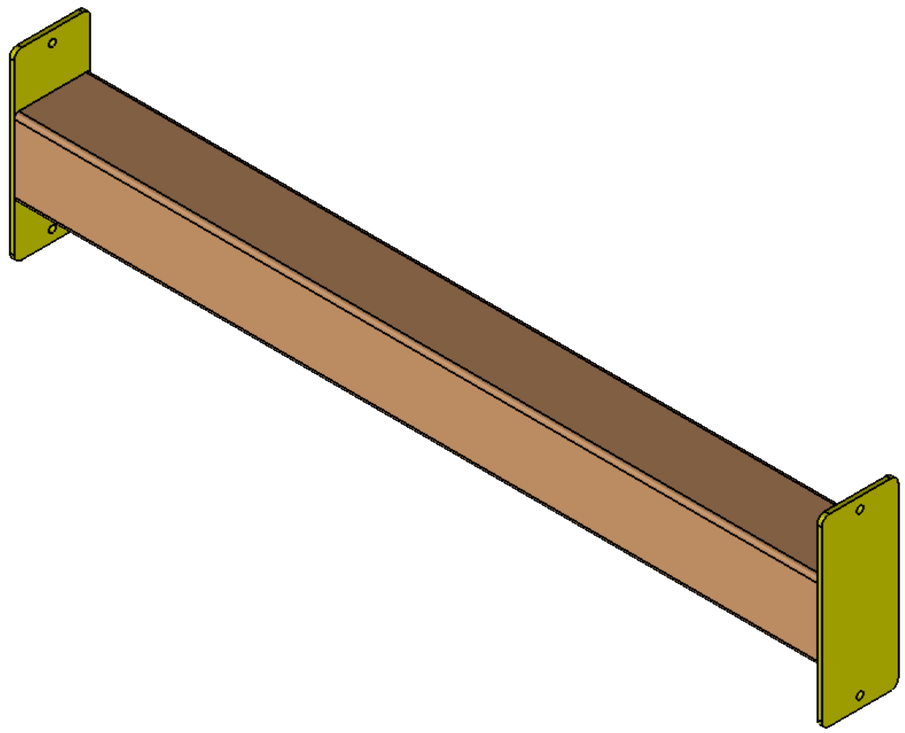

NOTE :

INTERMEDIATE SUPPORT TUBE - 50X50X1.5 MM THK - 530 MM L
ONE PANEL REQ QTY - 06 No'S
TOTAL REQ QTY - 24 No'S.

SPECIAL INSTRUCTION'S :

MTL - AL

TITLE - ROOF AUTOMATION

DWG NO - NTPL-244-PM-001-00-00-00

NIHVA Technologies Pvt. Ltd.

NIHVA TECHNOLOGIES PVT.LTD.PUNE
Website - www.nihva.com

	NAME	SIGNATURE	DATE
DRAWN	V.W.		16-07-2025
CHK'D	S.W.		18-07-2025
APPV'D	V.T.		18-07-2025

PRODUCT - RETRACTABLE ROOF

PROJECT NO - NTPL-244-PM | REVISION - 05

SITE LOCATION - | WEIGHT -

MATRIAL - | QTY - 1

If any queries contact - design.nihva@gmail.com

ALL DIMENSION ARE IN mm | A2


PROJECTION METHOD:


SCALE :


DRAWING

ITEM NO.	PART NUMBER	DESCRIPTION	QTY.
1	.rev0202SS WHEEL	NYLON WHEEL ∅65X18	24

REV DESCRIPTION	DATE	REV NO
	16-07-2025	REV 05
1.		

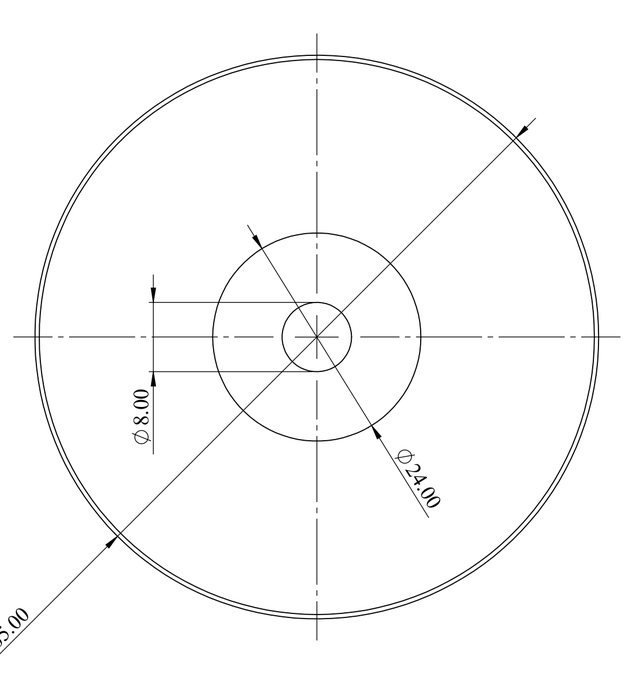

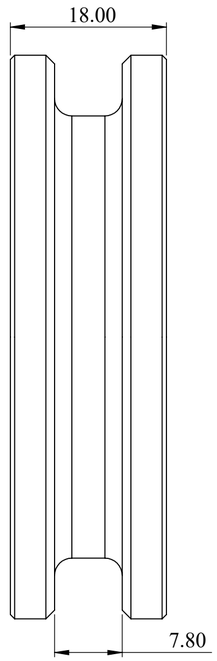

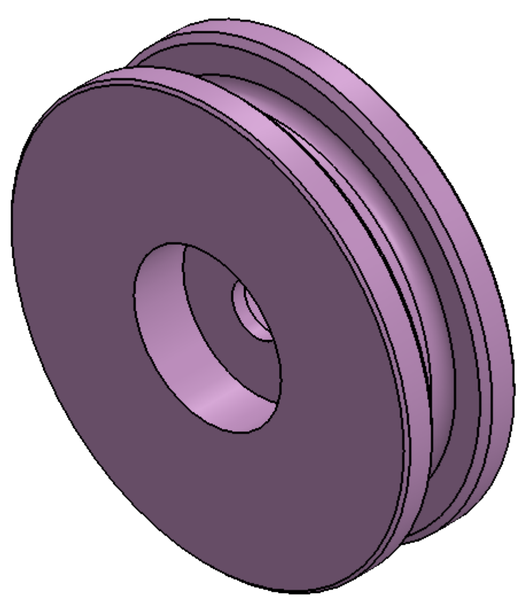

NOTE :

WHEEL
QTY - 24 No'S
MTL - NYLON

SPECIAL INSTRUCTION'S :

TITLE - ROOF AUTOMATION

DWG NO - NTPL-244-PM-001-00-00-00


NIHVA TECHNOLOGIES PVT.LTD.PUNE
Website - www.nihva.com


	NAME	SIGNATURE	DATE
DRAWN	V.W.		16-07-2025
CHK'D	S.W.		18-07-2025
APPV'D	V.T.		18-07-2025

PRODUCT - RETRACTABLE ROOF
PROJECT NO - NTPL-244-PM
REVISION - 05
SITE LOCATION -
WEIGHT -
MATRIAL -
QTY - 1
SCALE :
PROJECTION METHOD:
If any queries contact - design.nihva@gmail.com
ALL DIMENSION ARE IN mm
A2

DRAWING

ITEM NO.	PART NUMBER	DESCRIPTION	QTY.
1	L PLATE	91X106X3 MM THK	04

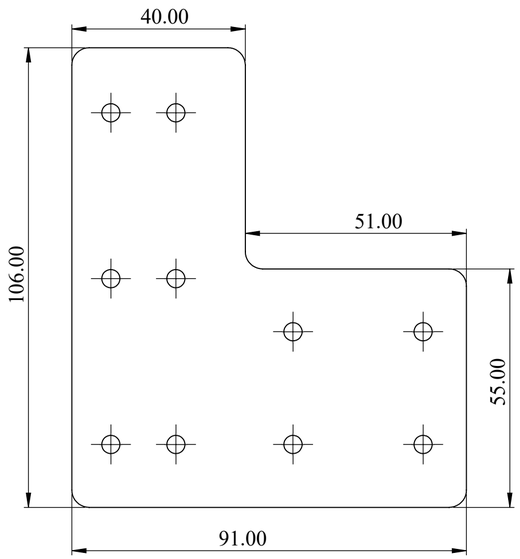

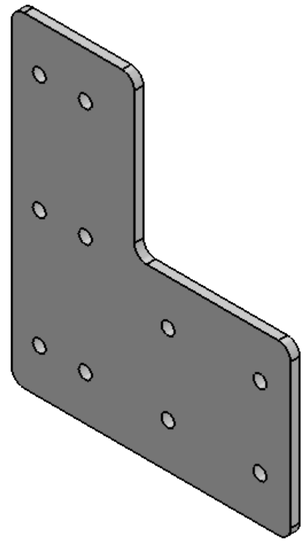

REV DESCRIPTION	DATE	REV NO
	16-07-2025	REV 05
1.		

NOTE :

L PLATE
MTL - SS
THK - 3MM
ONE PANEL REQ QTY - 04 No'S.
TOTAL REQ QTY - 24 No'S.

SPECIAL INSTRUCTION'S :

TITLE - ROOF AUTOMATION

DWG NO - NTPL-244-PM-001-00-00-00

NIHVA Technologies Pvt. Ltd.

NIHVA TECHNOLOGIES PVT.LTD.PUNE
Website - www.nihva.com

	NAME	SIGNATURE	DATE
DRAWN	V.W.		16-07-2025
CHK'D	S.W.		18-07-2025
APPV'D	V.T.		18-07-2025


PRODUCT - RETRACTABLE ROOF
PROJECT NO - NTPL-244-PM
REVISION - 05
SITE LOCATION -
WEIGHT -
MATRIAL -
QTY - 1
SCALE :
PROJECTION METHOD:


If any queries contact - design.nihva@gmail.com
ALL DIMENSION ARE IN mm
A2

DRAWING

ITEM NO.	PART NUMBER	DESCRIPTION	QTY.
1	T PLATE	156X91X3 MM THK	08

REV DESCRIPTION	DATE	REV NO
	17-07-2025	REV 05
1. Xyz		

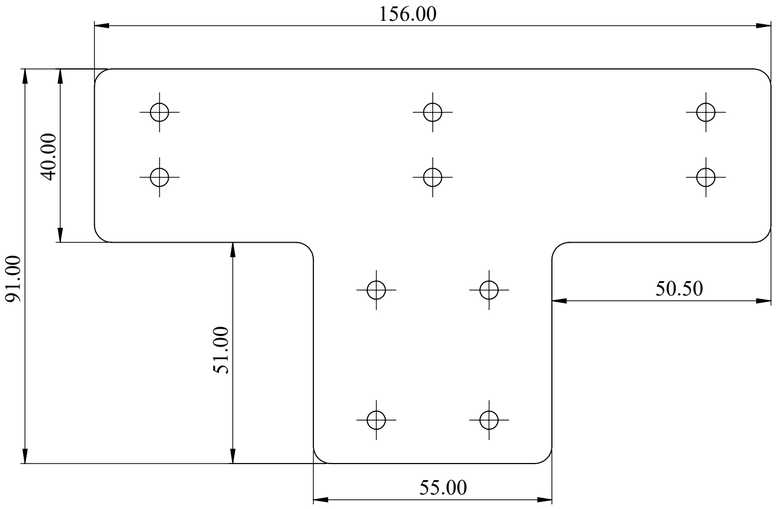

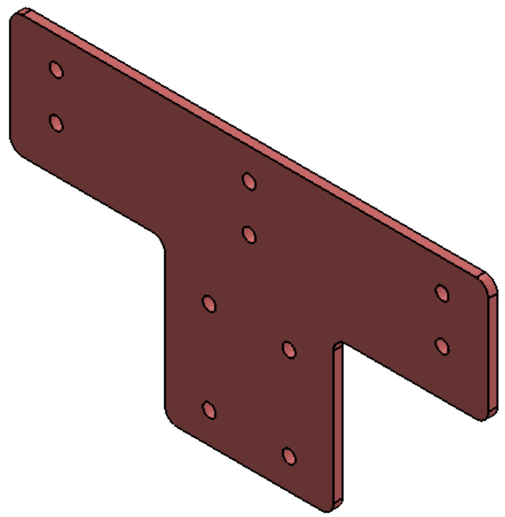

NOTE :

T PLATE
MTL - SS
THK - 3 MM
ONE PANEL QTY REQ - 08 No'S.
TOTAL QTY REQ - 48 No'S.

SPECIAL INSTRUCTION'S :

TITLE - ROOF AUTOMATION

DWG NO - NTPL-244-PM-001-00-00-00

NIHVA Technologies Pvt. Ltd.

NIHVA TECHNOLOGIES PVT.LTD.PUNE
Website - www.nihva.com

	NAME	SIGNATURE	DATE		
DRAWN	V.W.		17-07-2025	PRODUCT - RETRACTABLE ROOF	
CHK'D	S.W.		18-07-2025	PROJECT NO - NTPL-244-PM	REVISION - 05
APPV'D	V.T.		18-07-2025	SITE LOCATION -	WEIGHT -
				MATRIAL -	QTY - 1

If any queries contact - design.nihva@gmail.com

ALL DIMENSION ARE IN mm | A2


PROJECTION METHOD:


SCALE :


DRAWING

ITEM NO.	PART NUMBER	DESCRIPTION	QTY.
1	.rev0202AL INSIDE CORNER WELD PLATE	196X40X3 MM THK	1

REV DESCRIPTION	DATE	REV NO
	17-07-2025	REV 05
1.		

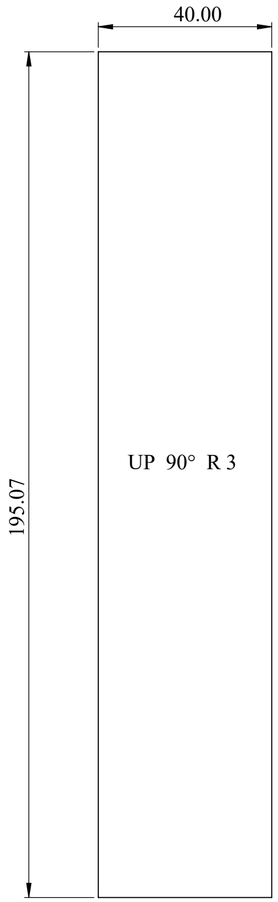

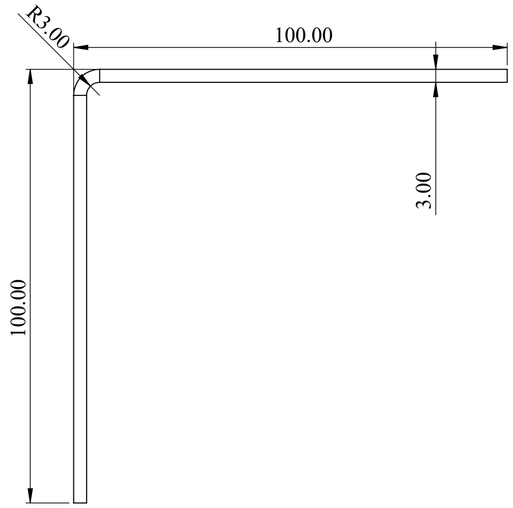

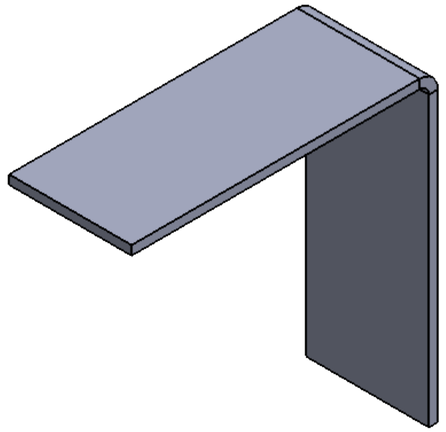

NOTE :

L ANGLE CORNER WELDING PLATE
MTL - ALUMINIUM
THK - 3 MM
ONE PANEL QTY REQ - 4 No'S
TOTAL QTY REQ - 24 No'S.

SPECIAL INSTRUCTION'S :

TITLE - ROOF AUTOMATION

DWG NO - NTPL-244-PM-001-00-00-00

NIHVA Technologies Pvt. Ltd.


NIHVA TECHNOLOGIES PVT.LTD.PUNE
Website - www.nihva.com


	NAME	SIGNATURE	DATE
DRAWN	V.W.		17-07-2025
CHK'D	S.W.		18-07-2025
APPV'D	V.T.		18-07-2025


PRODUCT - RETRACTABLE ROOF
PROJECT NO - NTPL-244-PM | REVISION - 05
SITE LOCATION - | WEIGHT -
MATRIAL - | QTY - 1
If any queries contact - design.nihva@gmail.com
PROJECTION METHOD:
SCALE :
ALL DIMENSION ARE IN mm | A2
SHEET 11 OF 16


DRAWING

REV DESCRIPTION	DATE	REV NO
	17-07-2025	REV 05
1.		

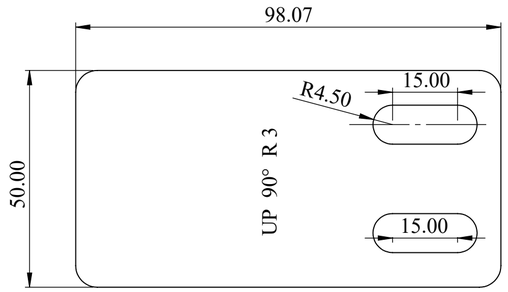

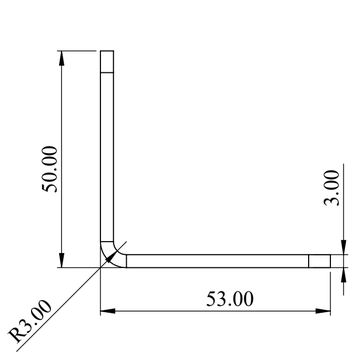

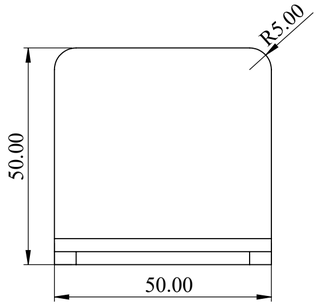

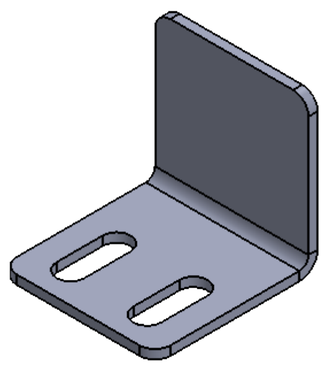

NOTE :

RACK SUPPORT PLATE
MTL - AL
THK - 3 MM
ONE PANEL QTY REQ - 12
TOTAL QTY REQ - 48

SPECIAL INSTRUCTION'S :

TITLE - ROOF AUTOMATION

DWG NO - NTPL-244-PM-001-00-00-00

NIHVA TECHNOLOGIES PVT.LTD.PUNE
Website - www.nihva.com

	NAME	SIGNATURE	DATE	
DRAWN	V.W.		17-07-2025	PRODUCT - RETRACTABLE ROOF
CHK'D	S.W.		18-07-2025	PROJECT NO - NTPL-244-PM / REVISION - 05
APPV'D	V.T.		18-07-2025	SITE LOCATION - / WEIGHT -
				MATRIAL - / QTY - 1

If any queries contact - design.nihva@gmail.com


ALL DIMENSION ARE IN mm | A2


PROJECTION METHOD:


SCALE :

DRAWING

REV DESCRIPTION	DATE	REV NO
	17-07-2025	REV 05
1.		

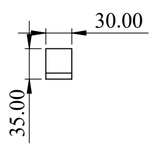

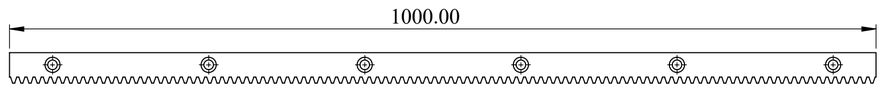

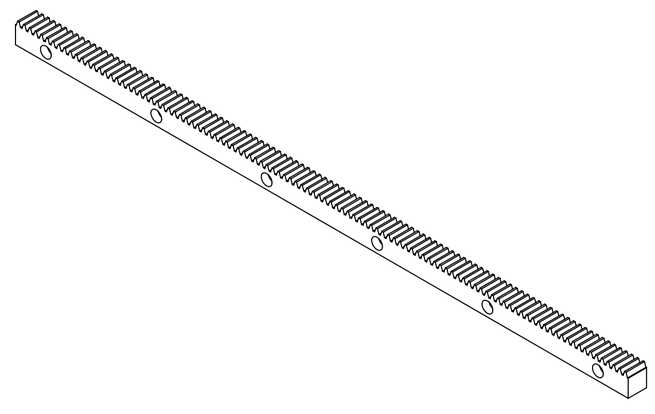

NOTE :

RACK
QTY - 30 No'S.

SPECIAL INSTRUCTION'S :

TITLE - ROOF AUTOMATION

DWG NO - NTPL-244-PM-001-00-00-00

NIHVA TECHNOLOGIES PVT.LTD.PUNE
Website - www.nihva.com

	NAME	SIGNATURE	DATE
DRAWN	V.W.		17-07-2025
CHK'D	S.W.		18-07-2025
APPV'D	V.T.		18-07-2025

PRODUCT - RETRACTABLE ROOF

PROJECT NO - NTPL-244-PM | REVISION - 05

SITE LOCATION - | WEIGHT -

MATRIAL - | QTY - 1


If any queries contact - design.nihva@gmail.com

PROJECTION METHOD:


SCALE :

ALL DIMENSION ARE IN mm | A2


DRAWING

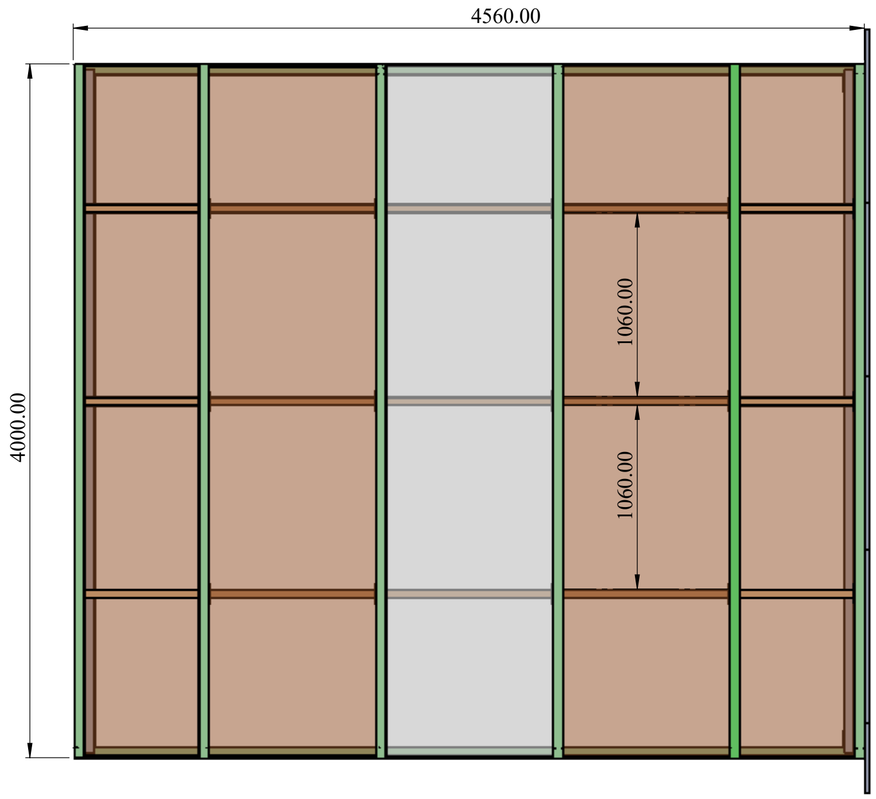


ITEM NO.	PART NUMBER	DESCRIPTION	QTY.
1	.Rev_02_paneel modify-03.		1
2	.Rev_02_panel modifiy-03 intermediate support assembly.		9
3	.Rev_02_SS WHEEL.	SS WHEEL ∅65X18	4
4	.Rev_02_panel modifiy-02 intermediate support assembly.		6
5	L ANGLE PLATE	17X52X3 MM THK	1
6	L PLATE	91X106X3 MM THK	1
7	.Rev_02_AL INSIDE CORNER WELD PLATE.	196X40X3 MM THK	4
8	C-MSBL12-35.SLDASM	SHOULDER BOLT	4
9	.Rev_02_RACK.		4
10	RACK CUT 200MM L		1

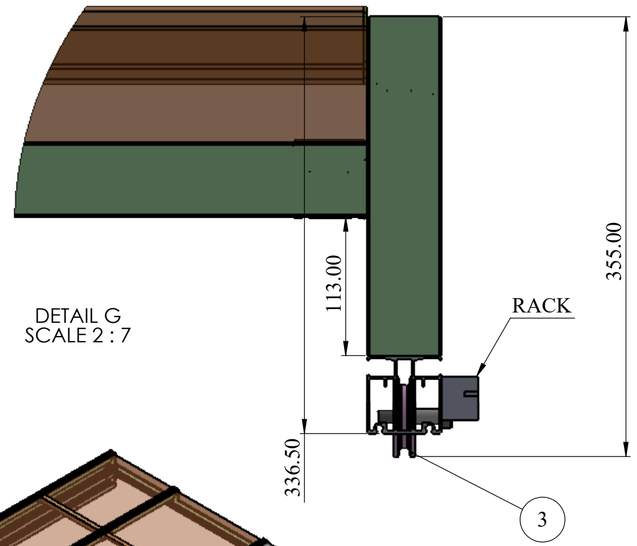

DETAIL G
SCALE 2 : 7

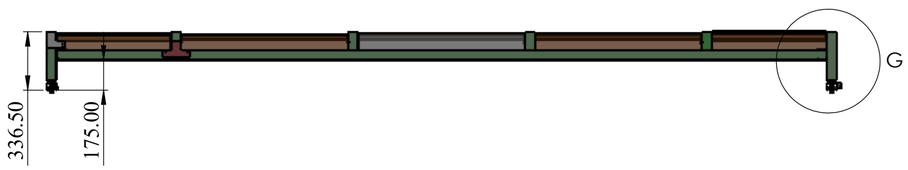

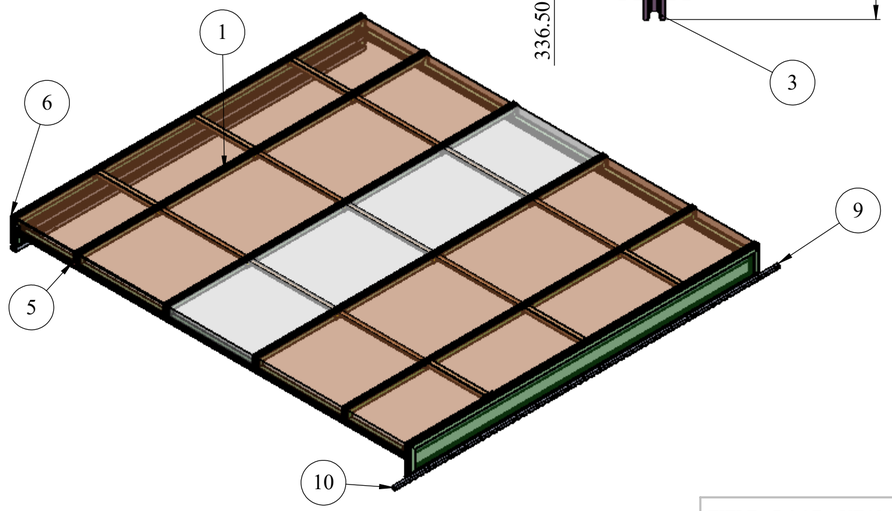

REV DESCRIPTION	DATE	REV NO
	17-07-2025	REV 05
1.		

NOTE :

MODIFIED MIDDLE PANEL
QTY - 02 No'S.

SPECIAL INSTRUCTION'S :

TITLE - ROOF AUTOMATION

DWG NO - NTPL-244-PM-001-00-00-00

NIHVA TECHNOLOGIES PVT.LTD.PUNE
Website - www.nihva.com


	NAME	SIGNATURE	DATE
DRAWN	V.W.		17-07-2025
CHK'D	S.W.		18-07-2025
APPV'D	V.T.		18-07-2025

PRODUCT - RETRACTABLE ROOF
PROJECT NO - NTPL-244-PM | REVISION - 05
SITE LOCATION - | WEIGHT -
MATRIAL - | QTY - 1
If any queries contact - design.nihva@gmail.com | PROJECTION METHOD: | SCALE :
ALL DIMENSION ARE IN mm | A2 | SHEET 14 OF 16


DRAWING


ITEM NO.	PART NUMBER	DESCRIPTION	QTY.
1	.Rev_02_paneel modify-03.		1

REV DESCRIPTION	DATE	REV NO
	17-07-2025	REV 05
1.		

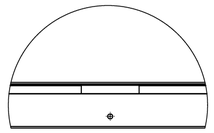



DETAIL I
SCALE 1 : 6

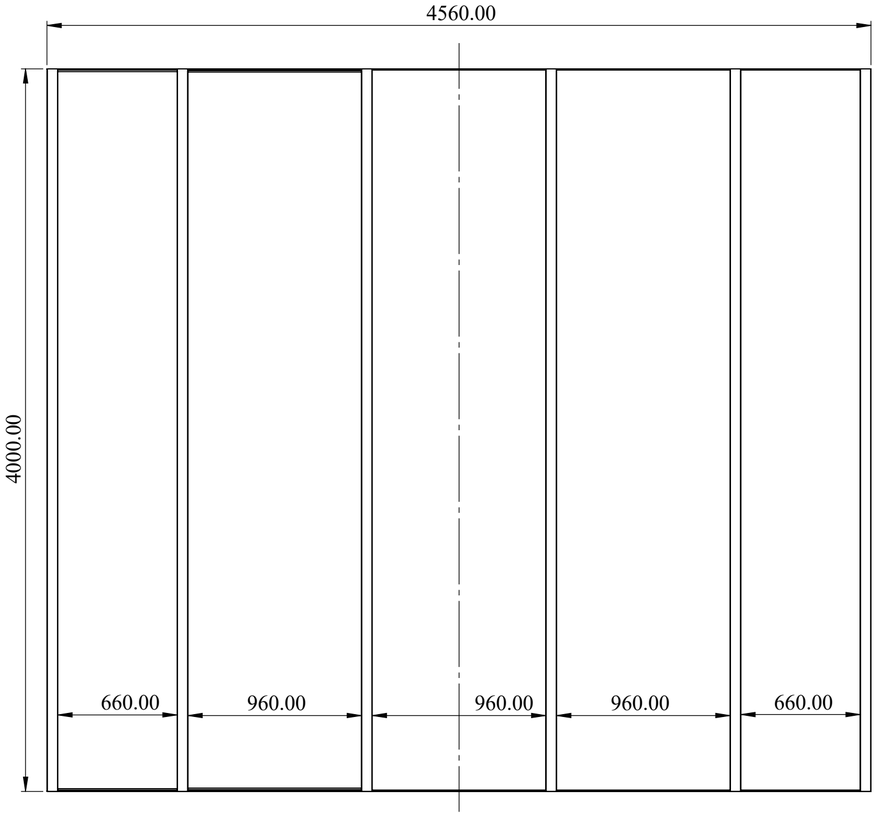


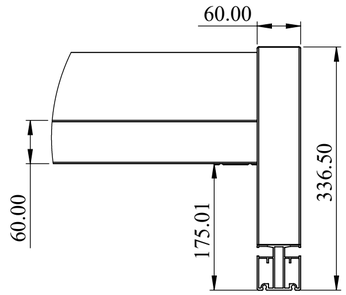

DETAIL H
SCALE 1 : 6

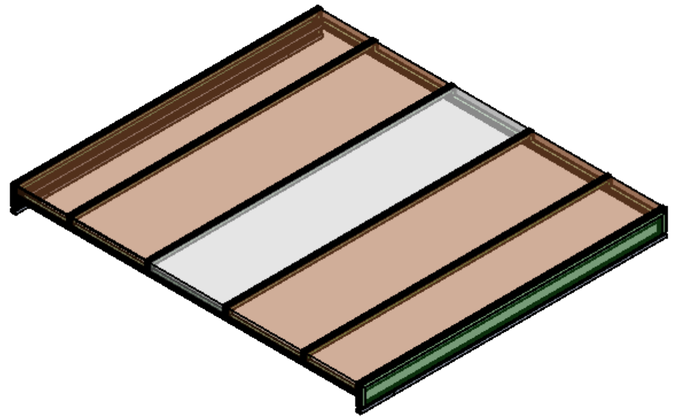

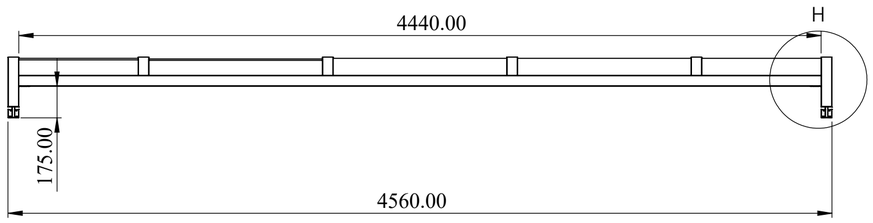

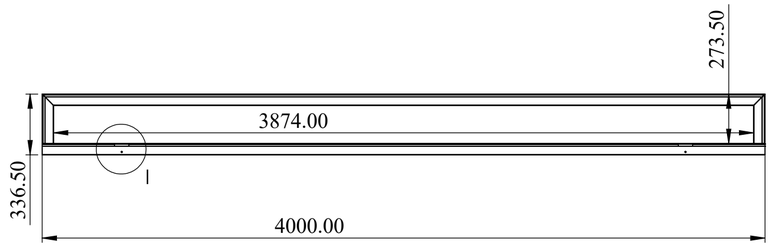

NOTE :

MIDDLE MODIFIED PANEL
QTY - 02 No'S.

SPECIAL INSTRUCTION'S :

ALL PROFILE IN GNT - 006

TITLE - ROOF AUTOMATION

DWG NO - NTPL-244-PM-001-00-00-00

NIHVA Technologies Pvt. Ltd.

NIHVA TECHNOLOGIES PVT.LTD.PUNE
Website - www.nihva.com


	NAME	SIGNATURE	DATE
DRAWN	V.W.		17-07-2025
CHK'D	S.W.		18-07-2025
APPV'D	V.T.		18-07-2025


PRODUCT - RETRACTABLE ROOF
PROJECT NO - NTPL-244-PM
REVISION - 05
SITE LOCATION -
WEIGHT -
MATRIAL -
QTY - 2

If any queries contact - design.nihva@gmail.com
ALL DIMENSION ARE IN mm
A2
PROJECTION METHOD:
SCALE :
SHEET 15 OF 16

DRAWING

REV DESCRIPTION	DATE	REV NO
	17-07-2025	REV 05
1.		

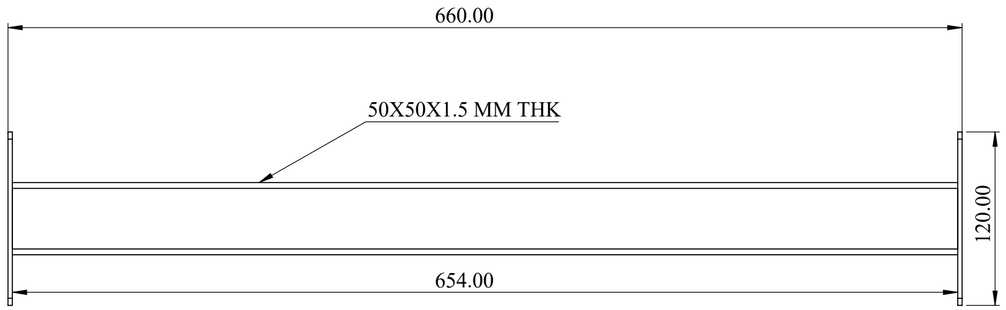

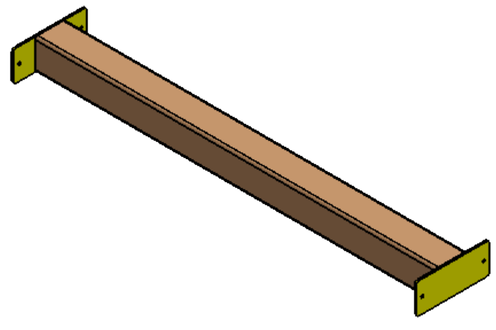

NOTE :

INTERMEDIATE SUPPORT TUBE- 50X50X1.5 MM THK - 660 MM L
MTL - AL
ONE PANEL QTY REQ - 06 No'S
TOTAL QTY REQ - 12 No'S.

SPECIAL INSTRUCTION'S :

TITLE - ROOF AUTOMATION

DWG NO - NTPL-244-PM-001-00-00-00

NIHVA Technologies Pvt. Ltd.

NIHVA TECHNOLOGIES PVT.LTD.PUNE
Website - www.nihva.com

	NAME	SIGNATURE	DATE
DRAWN	V.W.		17-07-2025
CHK'D	S.W.		18-07-2025
APPV'D	V.T.		18-07-2025

PRODUCT - RETRACTABLE ROOF

PROJECT NO - NTPL-000-PM | REVISION - 05

SITE LOCATION - | WEIGHT -

MATRIAL - | QTY - 1

If any queries contact - design.nihva@gmail.com

PROJECTION METHOD:

SCALE :

ALL DIMENSION ARE IN mm | A2