



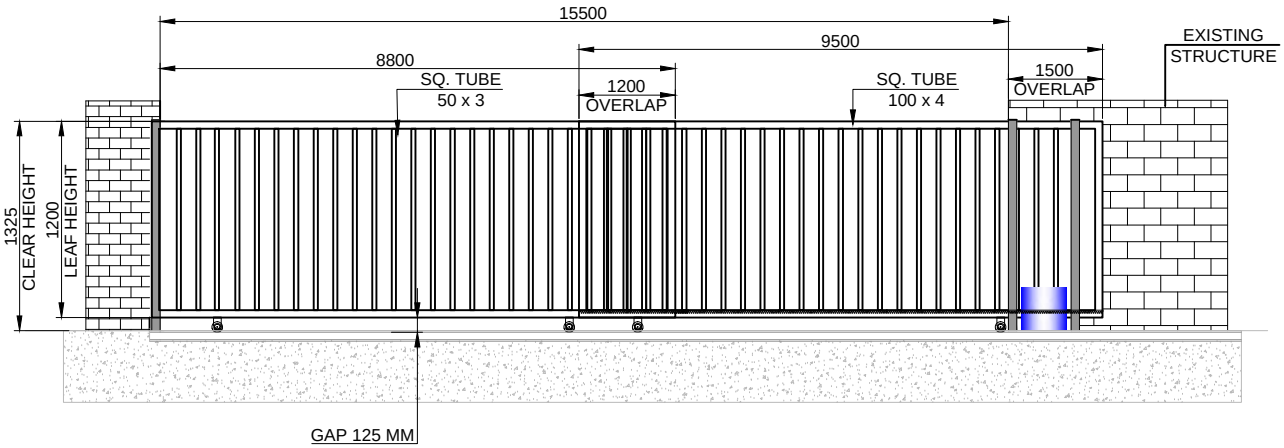


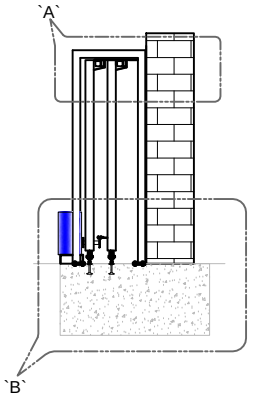

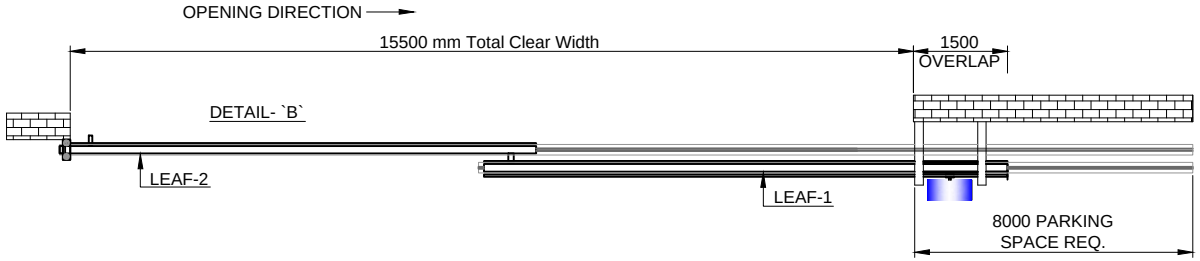

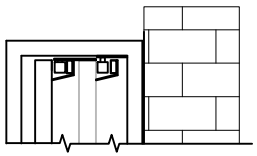

DETAIL -`A`

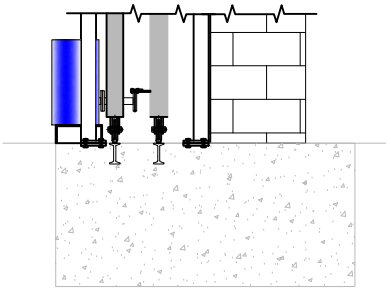

DETAIL- `B`

NOTE-
1. ALL REQUIRED CIVIL WORK WILL BE IN CLIENTS SCOPE.
2.GATE LEAF WILL BE IN TWO PARTS FOR TRANSPORTATION & WILL BE WELD TOGETHER ON SITE.
3.FLASHING LIGHT WITH ALARM.
4.VERTICAL ELE. SAFETY EDGE SENSOR(PHOTOCELL).
5.EXTRA PUSH BUTTON.
6.REMOTE CONTROL WITH RECEIVER.
7.EXTRA REMOTE UNIT.
8.KEY SWITCH.

TOLERANCE - ±10mm

CLEAR WIDTH	CLEAR HEIGHT	QUANTITY
15500	1200	01 NO

This drawing & design is the property of NIHVA TECHNOLOGIES. Not to be sold or copied to any other concern.

TITLE
2 LEAF TELESCOPIC SLIDING GATE

NIHVA TECHNOLOGIES PVT. LTD.

NIHVA TECHNOLOGIES PVT. LTD. PUNE
Tel : 020 66304033
Email:- info@nihva.com
Website:- www.nihva.com

	NAME	SIGN	DATE
DRAWN	P.V.A		18.07.2019
CHECK	V.M.T		18.07.2019
APPRD.			

CLIENT - LM WIND POWER BLADES
PROJECT -
SITE LOCATION - DABASPETH, BANGLORE
If any queries contact : design@nihva.com
DWG. NO. : NIHVA/19-20/0058 REV- R00
ALL DIMENSION ARE IN mm
SCALE: NTS WT: SHEET: 01 OF 01