

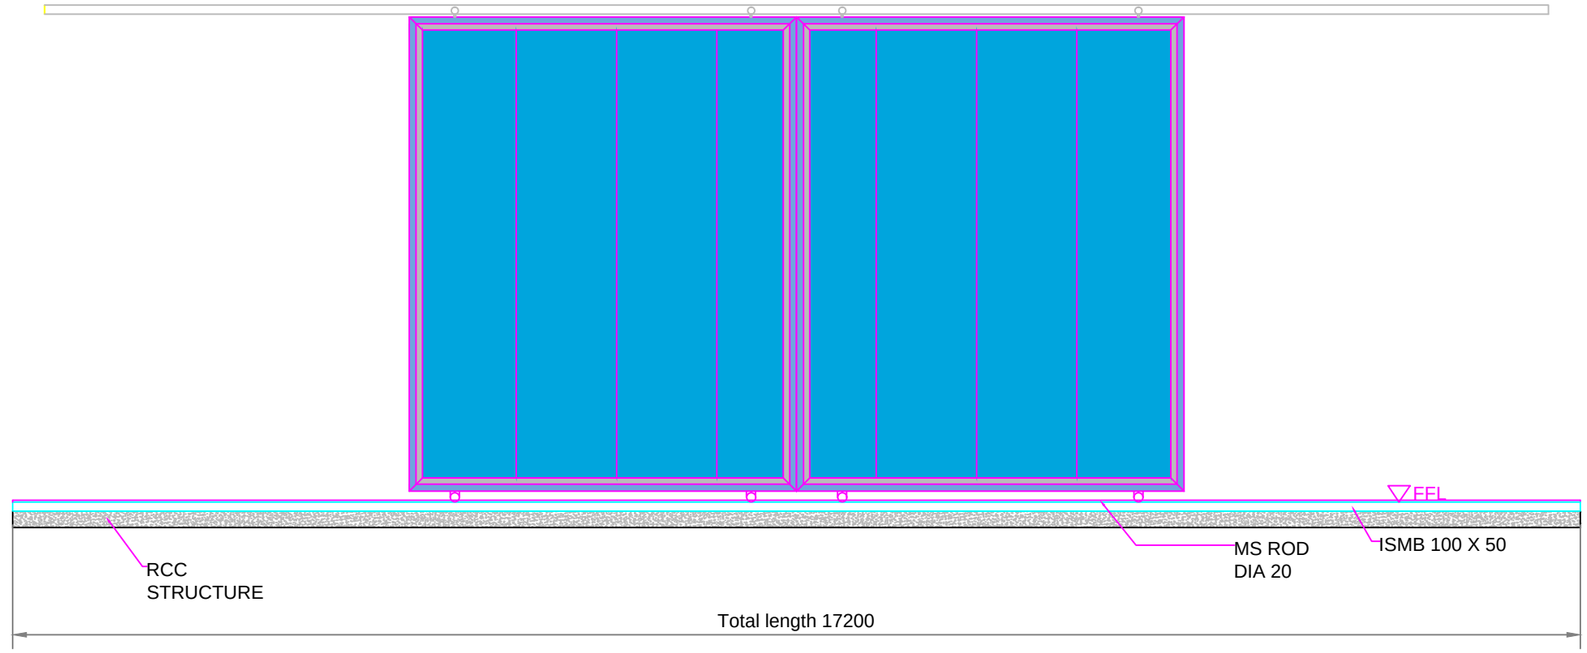


OUTSIDE ELEVATION

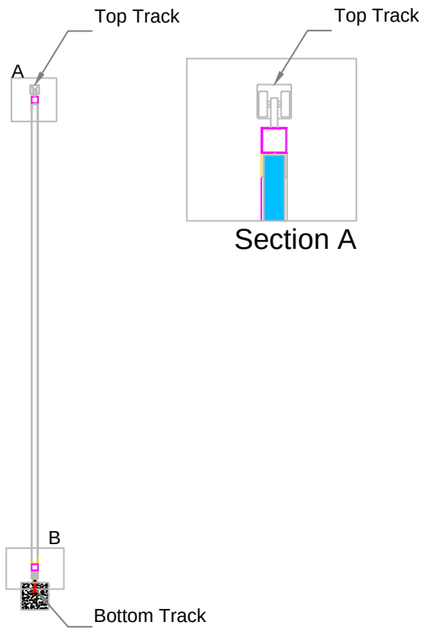

Section A

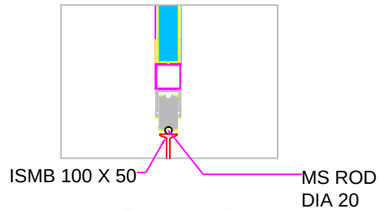

Section B

This drawing & design is the property of NIHVA TECHNOLOGIES. Not to be sold or copied to any other concern.

TITLE	SLIDING DOOR WITH FOUNDATION			NIHVA TECHNOLOGIES PVT. LTD. PUNE Tel : 020 66304033 Email:- info@nihva.com Website:- www.nihva.com
	NAME	SIGN	DATE	
DRAWN	G.P.		11.11.21	CLIENT :- Lestech Engineering India Pvt. Ltd.
CHECK	A.K.		11.11.21	PROJECT :- POSCO
				LOCATION :- Mangaon
If any queries contact : design@nihva.com				DWG. NO. :- NIHVA/21-22/0262 / REV:- R00
ALL DIMENSION ARE IN mm				SCALE:NTS / WT: / SHEET:01 OF 02