
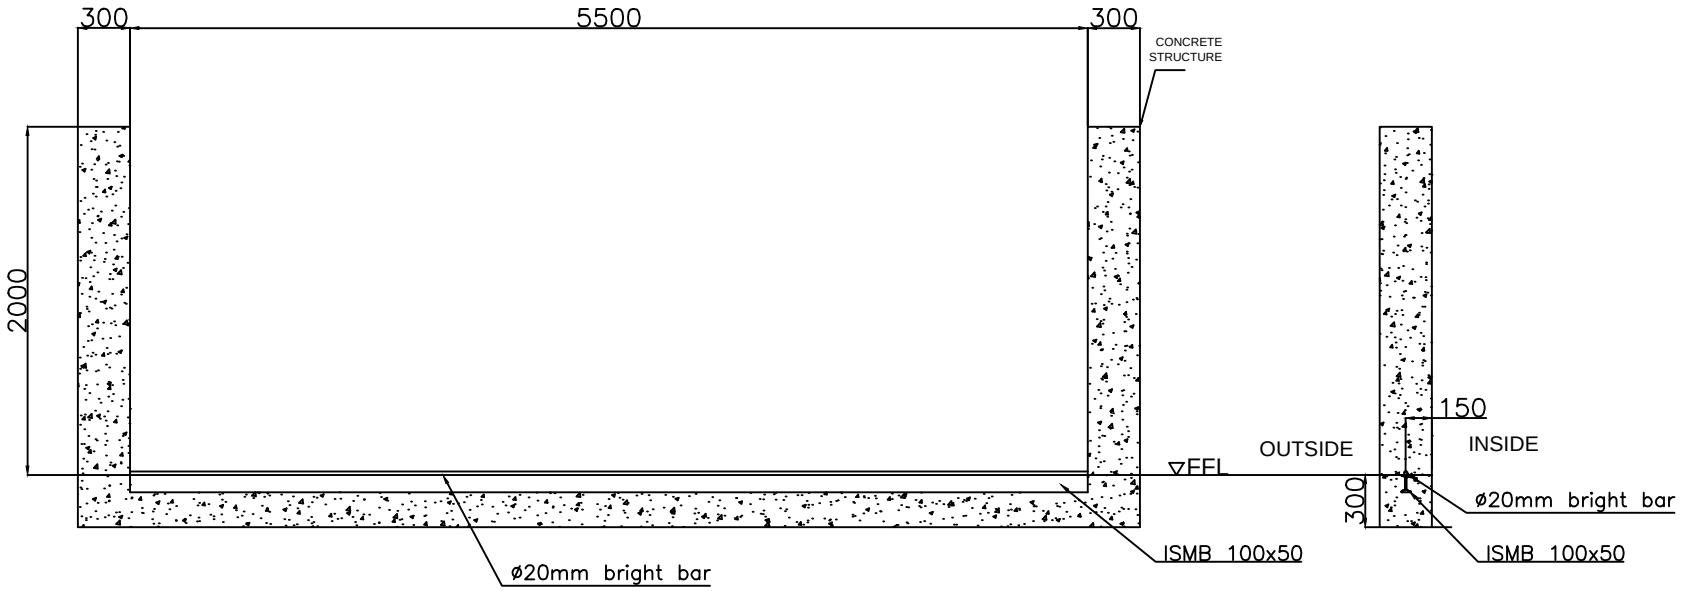


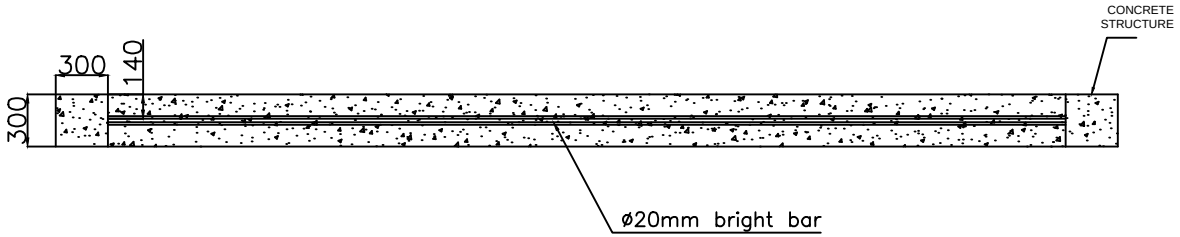

Technical Specs of Swing Gate

1. Total leaf weight ≈900 kg
2. Bottom Rail - Bright bar Ø20mm
3. ISMB 100 X 50 positioned in the foundation.

Note-

1. All dimension are in mm.
2. All civil work is under client scope.

This drawing & design is the property of NIHVA TECHNOLOGIES. Not to be sold or copied to any other concern.

TITLE
SLIDING AND FOLDING GATE FOUNDATION DRAWING

	NAME	SIGN	DATE
DRAWN	G.P.		08.09.21
CHECK	A.K.		08.09.21
APPRD.	V.T.		08.09.21

If any queries contact : design@nihva.com

ALL DIMENSION ARE IN mm

NIHVA
NIHVA TECHNOLOGIES PVT. LTD.

NIHVA TECHNOLOGIES PVT. LTD. PUNE
Tel : 020 66304033
Email:- info@nihva.com
Website:- www.nihva.com

CLIENT -HAIMAVATHY PROPERTIES PVT. LTD.

LOCATION - MUMBAI

PRODUCT - SLIDING & FOLDING GATE 5500 X 2000

NIHVA\21-22\0226 | REV- 02

SCALE: NTS | SHEET: 01 OF 02